

構造設計標準仕様

適用は■印を記入する。

1. 設計図書の優先順位

(1) 設計図書の優先順位

設計図書の優先順位は下記による。

1. 質問回答書(②)から⑤までに対するもの

2. 現場説明書

3. 特記仕様書

4. 図面

5. 標準仕様書

2. 建築物の構造内容

(1) 工事名称 森田厚史邸新築工事

建築場所 鳥取県鳥取市岩倉477-3

(2) 工事種別 ■新築 □増築 □増改築 □改築

(3) 構造種別 ■木造(W) □補強コンクリートブロック造(CB) □鉄骨造(S) □鉄筋コンクリート造(RC) □壁式鉄筋コンクリート造(WRC) □鉄骨鉄筋コンクリート造(SRC) □壁式プレキャスト鉄筋コンクリート造(WPRC) □プレキャスト鉄筋コンクリート造(PRC) □

(4) 階数 地下 0 階 地上 2 階 塔屋 0 階

(5) 主要用途 一戸建ての住宅

(6) 屋上付属物 ■太陽光設備 kN □キュービクル kN □広告塔 □煙突

(7) 特別な荷重 □エレベーター 11人乗り(ロープ式 油圧式) □リフト kN □ホイスト kN □倉庫積載床用 N/m² □

(8) 付帯工事 □RC塼 □擁壁 □ □ □ □

(9) 増築計画 □有() □無

(10) 構造計算ルート X方向ルート 1-() Y方向ルート 1-()

3. 地盤

(1) 地盤調査資料 □有(□敷地内 □近隣) □SWS調査 □ボーリング調査 □水平地盤反力係数の測定 □平板載荷試験 □液状化判定 □現場透水試験 □土質試験 □無(調査予定 □有 □無)

(2) 地盤調査計画 □ボーリング調査 □静的貫入試験 □標準貫入試験 □水平地盤反力係数の測定 □土質試験 □物理探査 □平板載荷試験 □試験堀(支持層の確認)

(3) 地盤調査及び試験杭の結果により、杭長、杭径、直接基礎の深さ、形状を変更する場合もある

4. 地業工事

(1) 直接基礎 ■ベタ基礎 □布基礎 □独立基礎 試験堀 □有 □無

深さ GL-0.100 m

長期許容支持力度 20 kN/m² 載荷試験 □有 □無

5. 鉄筋コンクリート工事

(1) コンクリート ■コンクリートはJIS認定工場の製品とし、施工に関してはJASS5による。

□耐久設計基準強度 Fd □一般 □標準 □長期

■セメントは、JIS R5210の普通ポルトランドセメントを標準とする。

■調合計画は、工事開始前に工事監理者の承認を得ること。

■寒中、暑中、その他特殊コンクリートの適用を受ける期間に当たる場合は、調合、打ち込み、養生、管理方法など必要事項について、工事監理者の承認を得ること。

■フレッシュコンクリートの塩化物測定は、原則として工事現場で(財)国土開発技術センターの技術評価をうけた測定器を用いて行い、試験結果の記録及び測定器の表示部を一回の測定ごとに撮影した写真(カラー)を保管し承認を得る。

測定検査の回数は、通常の場合、1日1回以上とし、1回の検査における測定試験は、同一試料から取り分けて3回行い、その平均値を試験値とする。

■構造体コンクリートについて、現場の圧縮強度試験供試体(JASS5T-603)は、現場水中養生、または現場封かん養生とし、採取は打ち込み区ごと、打ち込み日ごととする。

また、打ち込み量が150mを越える場合は、150mごとまたは、その端数ごとに1回を標準とする。1回に採取する供試体は、適当な間隔をおいた3台の運搬車からその必要本数を採取する。なお、供試体の数量は、特別指示なき場合は、1回当たり6本以上とし、そのうち4適用に3本を用いる。

■ポンプ打ちコンクリートは、打ち込む位置にできるだけ近づけて垂直に打ち、コンクリートの自由落下高さは、コンクリートが分離しない範囲とする。ポンプ圧送に際しては、コンクリート圧送技士または同等以上の技能を有する者が従事すること。なお、打ち込み継続中における打継ぎ時間間隔の限度は、外気温が25℃未満の場合は150分、25℃以上の場合には120分以内とする。

(2) 鉄筋 ■鉄筋は、JIS G3112の規格品を標準とする。施工はJASS5による。

□高強度せん断補強筋は、JIS G3137に規定されるD種1号適合品とする。

■鉄筋の加工寸法、形状、かぶり厚さ、鉄筋の継手位置、継手の重ね長さ、定着長さは「鉄筋コンクリート構造配筋標準図(1)(2)」または「壁式鉄筋コンクリート構造配筋標準図(1)(2)」による。

■D19未満は、すべて重ね継手とする。継手(D19以上)をガス圧接とする場合は、日本継手協会「鉄筋のガス圧接工事標準仕様書」による。

■ガス圧接部の抜き取り検査は、同一作業班が同一日に施工した圧接箇所ごと(200箇所を越えるときには、200箇所ごと)に1回行い、1回の試験は5本以上とする。

外観検査 ■有 □無、引張試験 ■有 □無、超音波試験 □有 □無

■柱の帯筋(HOOP)の加工方法は、■H型(タガ型) □W型(溶接型) □S型(スパイラル型)とする。

□コンクリート及び鉄筋の試験は、「建築物の工事における試験及び検査に関する東京都取扱要綱」第4条の試験機関で行うこと。

試験機関名
代行業者名
代行業者名とは、試験、検査に伴う業務を代行する者をいう。

(3) 型枠 ■材料 合板厚 12m/mを標準とする。 ■施工はJASS5による。

■型枠存置期間

種類 部 位	せき板				支柱		
	基礎、はり側、柱、壁		スラブ下、はり下		スラブ下		はり下
セメント の 積 累 の 方 法	単強ポルトランドセメント	普通ポルトランドセメント 高炉セメントA種 シリカセメントA種	単強ポルトランドセメント	普通ポルトランドセメント 高炉セメントA種 シリカセメントA種	単強ポルトランドセメント	普通ポルトランドセメント 高炉セメントA種 シリカセメントA種	単強ポルトランドセメント 普通ポルトランドセメント 高炉セメントA種 シリカセメントA種
	2	3	4	6	8	17	28
	3	5	6	10	12	25	28
	5	8	10	16	15	28	28
コンクリートの 圧縮強度	5.0N/mm ²		設計基準強度の50%		設計基準強度の		
					85%		100%

注) 1 片持はり、庇、スパン9.0m以上のはり下は、工事監理者の指示による。

注) 2 大ばりの支柱の盛りかえは行わない、また、その他のはりの場合も原則として行わない。

注) 3 支柱の盛りかえは、必ず直上階のコンクリート打ち後とする。

注) 4 盛りかえ後の支柱頂部には、厚い受板、角材または、これに代わるものを置く。

注) 5 支柱の盛りかえは、小ばりが終わってから、スラブを行う。

一時に全部の支柱を取り払って、盛りかえをしてはならない。

注) 6 上表以外のセメントを使用する場合は、工事監理者の指示による。

6. 設備関係

令第129条の2の3の事項 ※ 設計が該当する場合には、□にチェックを記入する。

・建築物に設ける建築設備にあつては、構造耐力上安全なものとして、以下の構造方法による。

■建築設備(昇降機を除く。)、建築設備の支持構造部及び緊結金物は、腐食又は腐朽のおそれがないものとする。

■屋上から突出する水槽、煙突、冷却塔その他これらに類するものは、支持構造部又は建築物の構造耐力上主要な部分に、支持構造部は、建築物の構造耐力上主要な部分に、緊結すること。

■給湯設備等は、建築物の構造耐力上主要な部分に適切な方法で緊結すること。

□煙突の屋上突出部の高さは、れんが造、石造、コンクリートブロック造又は無筋コンクリート造の場合は鉄製の支柱を設けたものを除き、90cm以下とすること。

□煙突で屋内にある部分は、鉄筋に対するコンクリートのかぶり厚さを5cm以上とした鉄筋コンクリート造又は厚さが25cm以上の無筋コンクリート造、れんが造、石造若しくはコンクリートブロック造とすること。

■建築物に設ける給水、排水その他の配管設備は、

■風圧、土圧及び水圧並びに地震その他の震動及び衝撃に対して安全上支障のない構造とすること。

■建築物の部分貫通して配管する場合においては、当該貫通部分に配管スリーブを設ける等有効な管の損傷防止のための措置を講ずること。

■管の伸縮その他の変形により当該管に損傷が生ずるおそれがある場合において、伸縮継手又は可撓継手を設ける等有効な損傷防止のための措置を講ずること。

■管を支持し、又は固定する場合においては、つり金物又は防振ゴムを用いる等有効な地震その他の震動及び衝撃の緩和のための措置を講ずること。

■法第20条第一号から第三号までの建築物に設ける屋上から突出する水槽、煙突その他これらに類するものにあつては、建設省告示第1389号により、風圧並びに地震その他の震動及び衝撃に対して構造耐力上安全なものとする。

■構造耐力上主要な部分となる部材に設ける開口部の大きさ及び形状、ならびに手摺等は、風圧、土圧及び水圧ならびに地震その他の震動及び衝撃に対して安全上支障のない構造とすること。

■床スラブ内に設備配管等を埋込む場合はスラブ厚さの1/3以下とし管の間隔を管径の3倍以上かつ5cm以上を原則とする。

■梁貫通孔は梁端部をさけて設けること。

位置については、使用補強工法の認定条件を遵守し、適切な検討を行うこと。

株式会社 Rbe architects 二級建築士事務所

二級 東京都知事登録 第 16330 号

二級 建築士登録 第 83516 号

渡 辺 隆 一

森田厚史邸新築工事

構造設計標準仕様書

藤田 撰 建築設計事務所

-

S-01

OSAMU FUJITA ARCHITECT+ASSOCIATES

一級建築士事務所 第2520号 / 一級建築士 第300013号 藤 田 撰

鉄筋コンクリート構造配筋標準図

1-1
基本事項

§ 1 一般事項

1. 使用材料、工法等は設計図による。
2. 設計図に記載なき場合は本標準図に従うものとする。
3. 本標準図は異形鉄筋を対象とし、d は呼び名に用いた数値とする。
4. 本標準図に示す単位は特記なき限りすべてmmとする。

2-1
材 料

§ 2 共通事項

コンクリート

規格番号	JIS A 5308	N/mm ²		
位置	種類	設計基準強度 F _c	比重	スラブ
主梁構全般	普通コンクリート	21	2.3	18
土間コンクリート	普通コンクリート	18	2.3	18
捨てコンクリート	普通コンクリート	18	2.3	18

鉄筋

規格番号	径	表示	種類	継手
JIS G 3112	10～16mm	D ₋	SD295A	重ね継手
	19～25mm	D ₋	SD345	かゝス圧接

2-2
基礎形式

ベタ基礎

2-3
鉄筋の表示記号

鉄筋の表示記号及び最外径は下表による。

記 号	＊	×	φ			
呼び径 d	D10	D13	D16	D19	D22	D25
最外径 D	11	14	18	21	25	28

・フックのない場合
・フックのある場合
・本型に差がある場合
・機械式継手表示
・溶接継手表示
(ガス圧接、突き合せ溶接)

2-4
鉄筋の折り曲げ

鉄筋末端部

曲 げ 角 度	図	鉄筋の種類	折り曲げ内法直径 (D)	
180°		SD295A SD345	D16以下 D19以上	3d以上 4d以上
135°				
90°				

鉄筋中間部

折り曲げ角度	図	鉄筋の使用箇所による呼称	鉄筋の種類	鉄筋の径による区分	折り曲げ内法直径 (D)
90°以下		帯筋 あばら筋 スパイラル筋 スラブ筋	SD295A SD345	D16以下 D19以上	3d以上 4d以上
		スラブ 基礎梁 などの主筋	SD295A SD345	D16以下 D19以上	4d以上 6d以上

2-5
鉄筋の定着及び重ね継手の長さ

鉄筋の種類	コンクリートの設計基準強度 (N/mm ²)	重ね継手の長さ (L1)	定着の長さ (L2)		
			一般 (L2)	下端筋 (L3)	
SD295A	18	45d 又は 35dフック付き	40d 又は 30dフック付き	20d 又は 10dフック付き	10d かつ 150mm 以上
	21	40d 又は 30dフック付き	35d 又は 25dフック付き		
	24	35d 又は 25dフック付き	30d 又は 20dフック付き		
SD345	18	50d 又は 35dフック付き	40d 又は 30dフック付き	10dフック付き	150mm 以上
	21	45d 又は 30dフック付き	35d 又は 25dフック付き		
	24	40d 又は 30dフック付き	35d 又は 25dフック付き		

コンクリートの割製のおそれのある部分への定着はL1とする。

1. 末端のフックは、定着及び重ねの長さには含まない。
2. 直径の異なる鉄筋の重ね継手の長さは、細いほうの鉄筋の継手長さによる。
3. 耐圧スラブの下端筋の定着長さは一般定着 (L2)、上端筋は25dとする。
4. 軽微な箇所については、工事監督者の承諾を得て定着長さを20d程度とすることができる。

2-6
継手一般

1. 重ね継手 (下記のいずれかとする)

1. 5L1 以上

約0. 5L1

2. 溶接継手を行う場合は原則として同一鋼種とし、鉄筋径の差はガス圧接の場合は2サイズ、突き合せ溶接の場合は1サイズまでとする。

2-7
鉄筋のあき

・鉄筋のあきaは原則として下記による。
呼び名の数値dの1. 5倍以上
粗骨材の最大寸法の1. 25倍以上
※溶接継手、機械式継手の場合のDはスリーブ又はカップラーの径とする。
・鉄筋径が異なる場合は大きい方による。

2-8
かぶり厚さ

鉄筋に対するコンクリートの最小かぶり厚さと設計かぶり厚さ

部 位		かぶり厚さ	
		仕上げあり	仕上げなし
土に接しない部分	屋根スラブ		
	床スラブ	20 (30)	30 (30)
	柱		
	耐力壁	屋 内 30 (40)	30 (40)
土に接する部分	擁壁・耐圧スラブ	40 (50)	40 (50)
	柱・梁・床スラブ・壁		
	布基礎の立上り	40 (50)	
基礎・擁壁・耐圧スラブ		60 (70)	

1. () 内の数値は設計かぶり厚さを示す。
2. 仕上げあり とは、鉄筋の耐久性上有効な仕上げのある場合とする。

3-1
基礎梁の継手及び定着

基礎梁の継手
重ね継手長さは、L1とし、継手位置は下図とする。

最下階 独立基礎でスラブ付きの場合

最下階 独立基礎でスラブが付かない場合

最下階 布基礎、べた基礎で地反力を受ける場合

(注) 〓〓は、継手の好ましい位置を示す。

定着要領

最下階 独立基礎の場合

最下階 布基礎、べた基礎の場合

(注) 破線は、柱内定着を示す。

3-2
あばら筋

あばら筋の加工は下図による。同時打込みのスラブ付の場合に限る。
※ねじれ応力を受ける腹筋は定着長さL2とする。

3-3
補強筋

交差部

L型 補強筋 D13

L型 補強筋 D10

※L型 交差部も同様に、L型補強筋を入れる

3-4
増打要領

増打要領 70≦a (a<70の時鉄筋補強は不要)

梁 貫通補強 φ>D/10又は、φ≧150の時、下の鉄筋補強を施す事。

梁巾	梁底	100φ	150φ	200φ	250φ	300φ	350φ	400φ

梁 貫通補強φ>D/10又は、φ≧150の時、下の鉄筋補強を施す事。

梁巾	梁底	100φ	150φ	200φ	250φ	300φ	350φ	400φ

梁 貫通補強φ>D/10又は、φ≧150の時、下の鉄筋補強を施す事。

種類	斜め筋	縦筋	横筋	上下縦筋	配筋図
H1	なし	なし	なし	なし	
H2	2-2-D13	2-2-D13	なし	なし	
H3	4-2-D13	2-2-D13	2-2-D13	2-2-D13	
H4	4-2-D16	2-2-D13	2-2-D13	2-2-D13	
H5	4-2-D16	2-2-D13	2-2-D13	3-2-D13	
H6	4-2-D19	4-2-D13	2-2-D13	3-2-D13	
H7	4-2-D22	4-2-D13	2-2-D13	3-2-D13	

(注) - は、一般部分のあばら筋を示す。

500≦D<700 a≧175
700≦D<900 a≧200
900≦D a≧250

(φ1+φ2)/2×3以上

4-1
鉄筋の折り曲げ及び定着

4-2
継 手

下向き荷重を受けるスラブの継手位置は下表による。
上向き荷重を受けるべた基礎(耐圧スラブ)の継手位置は下表の上端筋と下端筋を逆に読む。

		標 準 継 手 位 置	
上 端 筋	短 辺 方 向	B	D
	長 辺 方 向	A	B
下 端 筋	短辺・長辺方向	A	C D

4-3
片 持 ち ス ラ ブ

片持ちスラブ隅角部補強は設計図による。

先端に荷重のある場合。

4-4
補 強 筋

段造床

R/C壁・C/B壁が床にのる場合

5-1
階 段

スラブ階段

5-2
土間コンクリート

土間スラブの打継ぎ補強筋 (土間コンクリート、構造スラブ 共)

スラブ配筋	中間部	端部
シングル		
ダブル		

a≦300mm b:スラブ上端筋と同径、同じ仕様とする。

R/C壁・C/B壁の補強

500以上

株式会社 Rbe architects 二級建築士事務所

二級 東京都知事登録 第 16330 号

二級 建築士登録 第 83516 号

渡 辺 隆 一

森田厚史邸新築工事

鉄筋コンクリート構造配筋標準図

藤田 拱建築設計事務所

OSAMU FUJITA ARCHITECT+ASSOCIATES

一級建築士事務所 第2520号 ノー級建築士 第300013号 藤 田 拱

S-02

木工事・軸組工法工事 標準仕様書1	
1. 一般事項					2.2 ファスナー	
(1) 適用範囲 本仕様書は、建築物及び工作物の構造上主要な部分における木質構造工事に適用する。 ■ は、適用項目を示す。					ここに示すファスナーや接合金物などは、木質構造の接合部に適用する。ファスナーや接合金物等に錆を生じるおそれのある場合は適切な防錆処理を施す。鋼材の表面処理は特記による。 標準メッキ処理は、溶融亜鉛メッキ:MFZn -C、電気メッキ:EP-Fe/Zn 5/CM2とする。	
(2) 設計図書 設計図書とは本仕様書、設計図、指示書（現場説明書および質疑回答書を含む）をいう。					(1) くぎ、木ネジ、特殊ネジ	
(3) 標準仕様書 設計図書に記載無きものは「住宅金融公庫監修・木造住宅工事共通仕様書」及び「国土交通大臣官庁官庁営繕部監修・木造建築工事共通仕様書」に準ずる。 上記の仕様書に記載無き場合は、公共規格かこれに準ずる規格を適用する。					<table><tr><th>種 類</th><th>材 質</th><th>適 用 径</th><th>使用箇所</th><th>頭部/胴部の形状</th></tr><tr><td>■ N釘</td><td>・鉄 ・ステンレス鋼 ・鉄</td><td>N19～N150</td><td></td><td></td></tr><tr><td>■ C N釘 ■ B N釘 ■ Z N釘 ■ G N釘 □ S N釘</td><td></td><td>CN25～CN150 BN25～BN125 Z N 4 5 ～9 0 GNF25～GNF125 3.05 mm</td><td>耐力壁、床板、屋根</td><td></td></tr><tr><td>□ 木ネジ □ 特殊ネジ □ コースレッド</td><td>・軟鋼線材 ・真鍮</td><td></td><td>石膏ボード用 シージングインシュレーション ファイバーボード</td><td></td></tr></table>					種 類	材 質	適 用 径	使用箇所	頭部/胴部の形状	■ N釘	・鉄 ・ステンレス鋼 ・鉄	N19～N150			■ C N釘 ■ B N釘 ■ Z N釘 ■ G N釘 □ S N釘		CN25～CN150 BN25～BN125 Z N 4 5 ～9 0 GNF25～GNF125 3.05 mm	耐力壁、床板、屋根		□ 木ネジ □ 特殊ネジ □ コースレッド	・軟鋼線材 ・真鍮		石膏ボード用 シージングインシュレーション ファイバーボード																																					
種 類	材 質	適 用 径	使用箇所	頭部/胴部の形状	
■ N釘	・鉄 ・ステンレス鋼 ・鉄	N19～N150	
■ C N釘 ■ B N釘 ■ Z N釘 ■ G N釘 □ S N釘		CN25～CN150 BN25～BN125 Z N 4 5 ～9 0 GNF25～GNF125 3.05 mm	耐力壁、床板、屋根	
□ 木ネジ □ 特殊ネジ □ コースレッド	・軟鋼線材 ・真鍮		石膏ボード用 シージングインシュレーション ファイバーボード	
(4) 設計図書の優先順位 設計図書の優先順位は S-01構造設計標準仕様 1. 設計図書の優先順位による。					(2) ボルト、ナット	
(5) 疑義 疑義を生じた場合や工法の提案を行いたい場合には監理者に申し出、その処理方法について協議する。					<table><tr><th>種 類</th><th>材 質</th><th>適 用 径</th><th>表面処理、部品等級など</th></tr><tr><td>■ 呼び径六角ボルト</td><td>・SS400</td><td>M3～M36</td><td>・電気メッキ</td></tr><tr><td>□ 有効径六角ボルト</td><td>・SS400</td><td>M3～M20</td><td></td></tr><tr><td>□ 全ネジ六角ボルト</td><td>・SS400</td><td>M3～M36</td><td></td></tr><tr><td>□ ステンレスボルト</td><td>・SUS304</td><td></td><td></td></tr><tr><td>■ アンカーボルト</td><td>・SS400</td><td>M12、M16</td><td></td></tr><tr><td></td><td></td><td></td><td></td></tr></table>					種 類	材 質	適 用 径	表面処理、部品等級など	■ 呼び径六角ボルト	・SS400	M3～M36	・電気メッキ	□ 有効径六角ボルト	・SS400	M3～M20		□ 全ネジ六角ボルト	・SS400	M3～M36		□ ステンレスボルト	・SUS304			■ アンカーボルト	・SS400	M12、M16																																	
種 類	材 質	適 用 径	表面処理、部品等級など	
■ 呼び径六角ボルト	・SS400	M3～M36	・電気メッキ	
□ 有効径六角ボルト	・SS400	M3～M20	
□ 全ネジ六角ボルト	・SS400	M3～M36	
□ ステンレスボルト	・SUS304	
■ アンカーボルト	・SS400	M12、M16	
(6) 各種試験・検査報告書の提出 施工者は、各種工事の試験・検査結果ならびに施工記録を提出する。					・材質は鋼、ステンレス鋼、非金属。径と長さの組み合わせは「JIS B 1180」参照。	
(7) 製作要領書及び施工計画書の作成・提出 工事に先立ち、製作要領書や施工計画書を作成し、監督職員の承諾を受ける。					(3) 座金	
(8) 施工図等の提出 工事に先立ち各種の施工図等を作成し、監督職員の承諾を受ける。また、必要に応じて接合部のモックアップの作成を行う。プレカット工場を使用する場合には、プレカット図を施工図と位置づける。					<table><tr><th>適 用</th><th>材 質</th><th>適 用 径</th><th>形状・表面処理</th><th>その他</th></tr><tr><td>■ 座金</td><td>・SPCC (JIS G 3131)</td><td>M8～M24</td><td></td><td>・角座金・丸座金</td></tr><tr><td>□</td><td>・SPHC (JIS G 3141)</td><td></td><td></td><td>・電気メッキ</td></tr></table>					適 用	材 質	適 用 径	形状・表面処理	その他	■ 座金	・SPCC (JIS G 3131)	M8～M24		・角座金・丸座金	□	・SPHC (JIS G 3141)			・電気メッキ	
適 用	材 質	適 用 径	形状・表面処理	その他	
■ 座金	・SPCC (JIS G 3131)	M8～M24		・角座金・丸座金	
□	・SPHC (JIS G 3141)			・電気メッキ	
(9) 製作工場の選定、承諾 設計図書に基づき、工事の規模、加工内容に応じた技術と設備を備え、かつ自主管理能力を有する工場を選定し、監督職員の承諾を受ける。					・座金は用途ごと（引張、せん断）下表により使い分ける。	
(10) 各種試験・検査報告書の提出 施工者は、各種工事の試験・検査結果ならびに施工記録を提出する。					<table><tr><th colspan="2">ボルト径に対する座金の大きさ</th><th>8</th><th>10</th><th>12</th><th>16</th><th>20</th><th>24</th></tr><tr><td rowspan="4">引張を受けるボルト</td><td>厚さ</td><td>4.5</td><td>4.5</td><td>6</td><td>9</td><td>9</td><td>13</td></tr><tr><td>角座金の一辺</td><td>40</td><td>50</td><td>60</td><td>80</td><td>105</td><td>125</td></tr><tr><td>丸座金の直径</td><td>45</td><td>60</td><td>70</td><td>90</td><td>120</td><td>140</td></tr><tr><td>厚さ</td><td>3.2</td><td>3.2</td><td>3.2</td><td>4.5</td><td>6</td><td>6</td></tr><tr><td rowspan="2">せん断を受けるボルト</td><td>角座金の一辺</td><td>25</td><td>30</td><td>35</td><td>50</td><td>60</td><td>70</td></tr><tr><td>丸座金の直径</td><td>30</td><td>35</td><td>40</td><td>60</td><td>70</td><td>80</td></tr></table>					ボルト径に対する座金の大きさ		8	10	12	16	20	24	引張を受けるボルト	厚さ	4.5	4.5	6	9	9	13	角座金の一辺	40	50	60	80	105	125	丸座金の直径	45	60	70	90	120	140	厚さ	3.2	3.2	3.2	4.5	6	6	せん断を受けるボルト	角座金の一辺	25	30	35	50	60	70	丸座金の直径	30	35	40	60	70	80				
ボルト径に対する座金の大きさ		8	10	12	16	20	24	
引張を受けるボルト	厚さ	4.5	4.5	6	9	9	13	
	角座金の一辺	40	50	60	80	105	125	
	丸座金の直径	45	60	70	90	120	140	
	厚さ	3.2	3.2	3.2	4.5	6	6	
せん断を受けるボルト	角座金の一辺	25	30	35	50	60	70	
	丸座金の直径	30	35	40	60	70	80	
2. 材料の品質					(4) ドリフトピン、コーチスクリューボルト、ジベル、シアプレート、木栓	
2.1 木質材料					<table><tr><th>種 類</th><th>材 質</th><th>適用径・長さ</th><th>表面処理、その他</th></tr><tr><td>□ ドリフトピン(寸胴)</td><td>・S10C(JIS G4051)</td><td>φ12</td><td>・クロートメッキ</td></tr><tr><td>□ ドリフトピン(全ネジ)</td><td>・SS400、SNIW8～12</td><td>φ16～φ24</td><td>・電気メッキ</td></tr><tr><td>□ コーチスクリューボルト(ラグスクリュー)</td><td>・SWRCH10R (JIS G 3507)</td><td>φ9～φ19</td><td>・電気メッキ</td></tr><tr><td>□ スプリットリング</td><td>・SS400</td><td>φ64、φ102</td><td></td></tr><tr><td>□ シアプレート</td><td></td><td></td><td>・電気メッキ</td></tr><tr><td>□ 木栓</td><td>・堅木</td><td>M12～M24</td><td></td></tr></table>					種 類	材 質	適用径・長さ	表面処理、その他	□ ドリフトピン(寸胴)	・S10C(JIS G4051)	φ12	・クロートメッキ	□ ドリフトピン(全ネジ)	・SS400、SNIW8～12	φ16～φ24	・電気メッキ	□ コーチスクリューボルト(ラグスクリュー)	・SWRCH10R (JIS G 3507)	φ9～φ19	・電気メッキ	□ スプリットリング	・SS400	φ64、φ102		□ シアプレート			・電気メッキ	□ 木栓	・堅木	M12～M24																													
種 類	材 質	適用径・長さ	表面処理、その他	
□ ドリフトピン(寸胴)	・S10C(JIS G4051)	φ12	・クロートメッキ	
□ ドリフトピン(全ネジ)	・SS400、SNIW8～12	φ16～φ24	・電気メッキ	
□ コーチスクリューボルト(ラグスクリュー)	・SWRCH10R (JIS G 3507)	φ9～φ19	・電気メッキ	
□ スプリットリング	・SS400	φ64、φ102	
□ シアプレート			・電気メッキ	
□ 木栓	・堅木	M12～M24	
□ 記入無き梁桁、母屋、タル木等の曲げ材のうち、見えがかり材は目視等級材の甲種2級、見えない部分の木材は甲種3級とする。その他は乙種2級とする。					・木栓はナラ・ケヤキ・カシ等で気乾比重0.6以上の広葉樹とし、節や目切れ等の欠点の無いものとする。	
□ 主要構造部には機械等級区分製材を用いることを原則とする。					(5) 接合金物、鋼材	
□ 乾燥の腐食割りを行う。但し見えがかり部・相欠き部材・構造用合板の釘接合面には行わない。					■ 在来金物	
□ 含水率は平均含水率とし下地材等に用いる場合でも含水率D25以下であることを確認する。					□ 特殊金物（ピン工法等）	
■ 強度等級を指定した材料は特に、材料の欠点の節、目切れ等にご注意して材料を選定し、仕口や接合部に欠点が当たらないように加工する。					<table><tr><th>種 別</th><th>材 質</th><th>表面処理</th><th>適用、形状、その他</th></tr><tr><td>■ Zマーク</td><td></td><td></td><td></td></tr><tr><td>□ Cマーク</td><td></td><td></td><td></td></tr><tr><td>■ 引寄せ金物</td><td></td><td></td><td></td></tr><tr><td>■ その他の金物</td><td></td><td></td><td></td></tr><tr><td>■ 鋼材</td><td>・SS400</td><td></td><td>形状は詳細図</td></tr></table>					種 別	材 質	表面処理	適用、形状、その他	■ Zマーク				□ Cマーク				■ 引寄せ金物				■ その他の金物				■ 鋼材	・SS400		形状は詳細図																																
種 別	材 質	表面処理	適用、形状、その他	
■ Zマーク	
□ Cマーク	
■ 引寄せ金物	
■ その他の金物	
■ 鋼材	・SS400		形状は詳細図	
■ 材の曲がりについては、上記にかかわらず目視等級1級相当とする。					(6) 接着剤（接着接合）	
(2) 構造用集成材、構造用単板積層材 (LVL) 本項の内容は特記無きかぎり構造用集成材及び構造用単板積層材の日本農林規格に準ずること。					ここでいう接着接合とは、建設現場で用いるものを対象とし、内容は特記による。	
※リスト内は設計基準強度が同等以上の樹種に変更可能です。 設計基準強度は、（圧縮・引張・曲げ・せん断・ヤング係数）を示す。					3. 材料品質の検査方法	
<table><tr><th>部 位</th><th>品 名</th><th>樹 種</th><th>曲げヤング係数区分</th><th>材 質</th><th>接 着</th><th>材の70°ビ</th></tr><tr><td>柱(一部)</td><td>構造用集成材 E95F315(同一等級)</td><td>ひのき</td><td></td><td>2種</td><td>環境C</td><td>F☆☆☆☆</td></tr><tr><td>梁(hg)</td><td>構造用集成材 E105F300(対称異等級)</td><td>欧州707</td><td></td><td>2種</td><td>環境C</td><td>F☆☆☆☆</td></tr><tr><td>梁(hhg)</td><td>構造用集成材 E120F330(対称異等級)</td><td>米松</td><td></td><td>2種</td><td>環境C</td><td>F☆☆☆☆</td></tr><tr><td></td><td></td><td></td><td></td><td></td><td></td><td></td></tr><tr><td></td><td></td><td></td><td></td><td></td><td></td><td></td></tr><tr><td></td><td></td><td></td><td></td><td></td><td></td><td></td></tr><tr><td></td><td></td><td></td><td></td><td></td><td></td><td></td></tr></table>					部 位	品 名	樹 種	曲げヤング係数区分	材 質	接 着	材の70°ビ	柱(一部)	構造用集成材 E95F315(同一等級)	ひのき		2種	環境C	F☆☆☆☆	梁(hg)	構造用集成材 E105F300(対称異等級)	欧州707		2種	環境C	F☆☆☆☆	梁(hhg)	構造用集成材 E120F330(対称異等級)	米松		2種	環境C	F☆☆☆☆																																	
部 位	品 名	樹 種	曲げヤング係数区分	材 質	接 着	材の70°ビ	
柱(一部)	構造用集成材 E95F315(同一等級)	ひのき		2種	環境C	F☆☆☆☆	
梁(hg)	構造用集成材 E105F300(対称異等級)	欧州707		2種	環境C	F☆☆☆☆	
梁(hhg)	構造用集成材 E120F330(対称異等級)	米松		2種	環境C	F☆☆☆☆	
(3) 構造用合板、構造用パネル 本項の内容は特記無きかぎり構造用合板及び構造用パネルの日本農林規格に準ずること。	
<table><tr><th>部 位</th><th>品 名</th><th>強度等級</th><th>曲げ性能基準</th><th>板面品質</th><th>接 着</th><th>寸法(mm)</th><th>材の70°ビ</th></tr><tr><td>屋根</td><td>構造用合板</td><td>2級</td><td>—</td><td>C～D</td><td>特類</td><td>12mm</td><td>F☆☆☆☆</td></tr><tr><td>床</td><td>構造用合板</td><td>2級</td><td>—</td><td>C～D</td><td>特類</td><td>24mm</td><td>F☆☆☆☆</td></tr></table>					部 位	品 名	強度等級	曲げ性能基準	板面品質	接 着	寸法(mm)	材の70°ビ	屋根	構造用合板	2級	—	C～D	特類	12mm	F☆☆☆☆	床	構造用合板	2級	—	C～D	特類	24mm	F☆☆☆☆	・構造用合板はできるだけ大きい寸法のものを用いる。																																				
部 位	品 名	強度等級	曲げ性能基準	板面品質	接 着	寸法(mm)	材の70°ビ	
屋根	構造用合板	2級	—	C～D	特類	12mm	F☆☆☆☆	
床	構造用合板	2級	—	C～D	特類	24mm	F☆☆☆☆	
株式会社 Rbe architects 二級建築士事務所 二級 東京都知事登録 第 16330 号 二級 建築士登録 第 83516 号 渡 辺 隆 一	

木工事・軸組工法工事 標準仕様書2	
(7) ジベル接合 ・木部材は接合部付近の割れ、節、目切れなどの欠点に注意し、彫込み・打ち込みまたは圧入に際して割れを生じないよう、ジベルの種類に応じた断面と余長をもたせる。 ・接合材は十分圧着させる。木材の収縮によるボルトの緩みをチェックし、緩んだものについては再度締め直しを行う。 (8) 既成金物の接合 ・羽子板ボルト、ひら金物、短冊金物、かね折り金物および箱金物などの取り付けは、それぞれの仕様に基づき、接合両材の間に密着するように締め付ける。 (9) 接着接合 ・接合部の耐力は、使用材料および使用方法に適した接着性能の試験を行い確認する。 ・接着剤を用いた接合を行う手順は、接着剤製造業者の推奨する接着仕様に従うとし、実験によって接合部に要求される耐力と耐久性が立証された場合はその際の作業条件を標準とする。 (10) その他の方法による接合 ・使用材料および使用方法は構造図によるものとし、監督職員の承諾を得る。 7. 運搬・建て方 (1) 輸送計画 製品の輸送に当たっては、建方計画に支障がないように、道路状況、現場作業手順等を考慮し十分な検討を行う。また、輸送時に製品の品質を損なわないようにする。 □ 輸送計画書の提出 [] (2) 集積・保管 集積の際は適当な受け台などを設け、材にねじれや曲がりの損傷を与えないように注意する。降雪や降雨に対する保護としてシート養生を行う。ただし、エアコンの効いた室内は乾燥による割れが発生するため避ける。 □ 集積場の確認 [] (3) 建方計画 ■ 建方計画書の提出 アンカーボルトの施工方法、建方スペース、建方機械、搬入・仕分け、地組み、足場計画、建方、養生、安全対策などについて検討し、建方計画書としてまとめる。 (4) 施工時の安全性 建方作業中および作業後、横架材上に諸材料または機械などの重量物を積載する場合、あるいは柱に大きな引張力を与えるなどの場合は管理者の承諾を受ける。また、強風などによる諸外力に対しては、必要に応じて仮設補強等の処置を施す。 ■ 施工時の安全性に対する検討書の提出 □ 施工時荷重条件の通知 (5) アンカーボルトの施工 ・芯出しは、型板を用いて基準墨に正しく合せて適切な機器等で正確に行う。 ・アンカーボルトは鉄筋等を用いて組立て、適切な補助材で固定しコンクリートの打ち込みを行う。 ・アンカーボルトはダブルナットとする。 □ 適用除外 [] ・土台の穴あけはコンクリート打設後、ボルトの通り芯からのずれを実測してから行う。 ■ 通り芯からの誤差 : ■ ±3mm以下 □ [] ・柱脚部に接合金物（製作金物）を使用する部位については下記の数値を受け入れ基準とする。 ■ 柱据え付け面：基準高さからの誤差 ±2mm以下 ■ 柱隣接間中心距離の誤差e1 ±2mm以下 ■ 通り芯からの誤差e2 ±2mm以下 通り芯 ○ <	


(12) 面材耐力壁

1. 構造用合板・大壁造の場合

2. 構造用合板・真壁造の場合

1. 構造用合板・大壁造の場合


2. 構造用合板・真壁造の場合

 

☐ (床水平構面) 単位長さあたりの許容せん断力 1.96kN/m




□ S1 床仕様(床水平構面) 単位長さあたりの許容せん断力 3.53kN/m

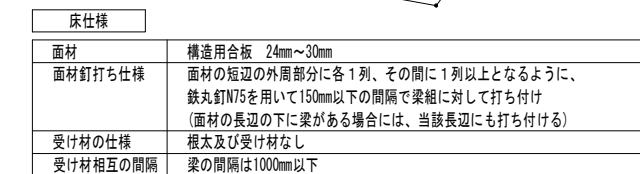

■S2床仕様(床水平構面) 単位長さあたりの許容せん断力 7.84kN/m




■S3勾配屋根仕様（屋根水平構面） 単位長さあたりの許容せん断力 1.37kN/m（屋根勾配30度以下）
0.98kN/m（屋根勾配45度以下）

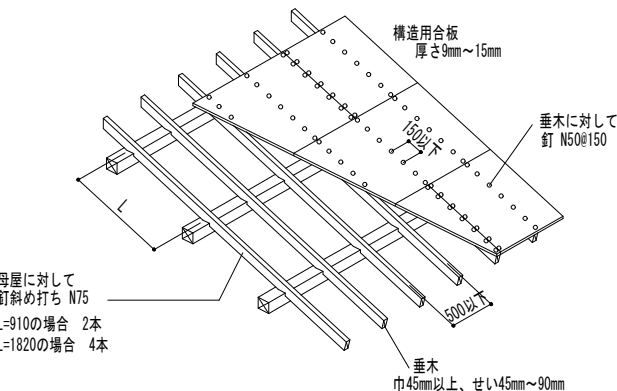






屋根仕様	
面材	構造用合板 9mm～15mm
面材釘打ち仕様	面材を鉄釘N150を用いて150mm以下の間隔で 垂木に対して打ち付け
垂木の仕様	幅45mm以上、せい45mm～90mmの垂木を、相互の間隔 500mm以下で、軒・母屋・棟木の上の傾斜面に並列して設置
垂木と軒・母屋・棟木の接合仕様	軒・母屋・棟木の上に設けられた傾斜面（垂木道）に垂木を載せ、 棟木の側面から軒・母屋・棟木の上面上に対してN75釘2本を斜め打ち

■ 垂木の軒先部接合仕様

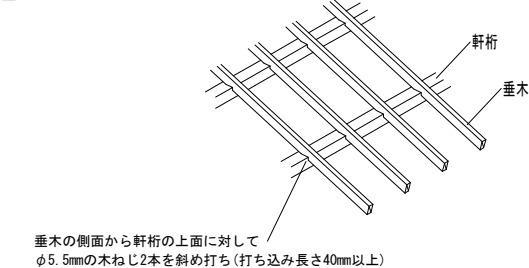


1. 土台用アンカーボルト

- ・M12アンカーボルトは@2,000以内に配置、基礎への埋込長さは250mm以上とする。
- ・耐力壁の部分は、その両端の柱の下部にそれぞれ200mm以内の位置に配置すること。

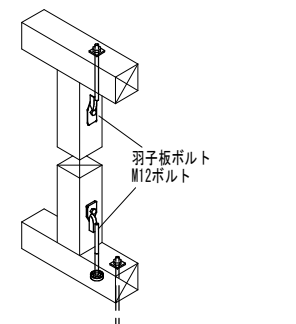    

※(ほ)羽子板ボルト+スクリー釘の場合は
長さ50mm径4.5mmのスクリー釘を
1本追加すること

6. (へ) 10kNホールダウン・引寄金物

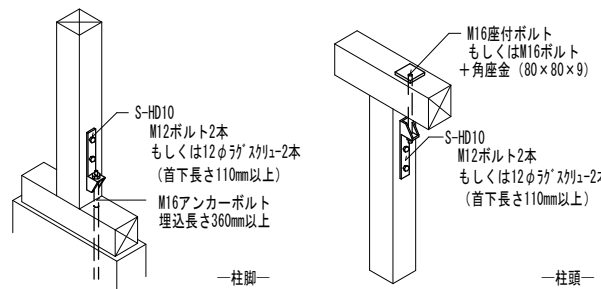


M16 座付ボルト
もしくは M16 ボルト
+ 角座金 (80×80×9)


S-HD15
M12 ボルト 3本
もしくは 12φ ユー スクリュー 3本
(首下長さ110mm以上)

— 柱頭 —

8. (ち) 20kNホールダウン・引寄金物

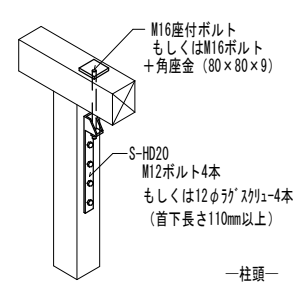

9. (リ) 25kNホールダウン・引寄金物

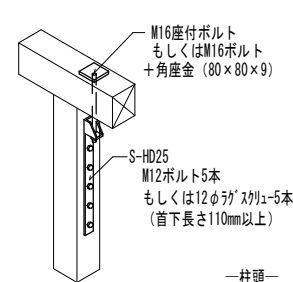

10. (ぬ) 30kNホールダウン・引寄金物 ((と) ×2セット)

金物の短期許容引張耐力は金物図参照。

回	高耐力アンカーボルトM16（り×2以上） 取付位置：金物メーカー仕様による。 埋込：310mm以上
⊗	M16ホールダウンアンカー（ぬ〜り×2未満） 取付位置：金物メーカー仕様による。 埋込：360mm以上
◎	M16ホールダウンアンカー（と〜り） 取付位置：金物メーカー仕様による。 埋込：360mm以上
。	M12アンカーボルト 設置位置：XY方向柱際（柱芯より200mm以内）に1本、 @1000mm以下 C1箇所については柱芯より150mm以内 @1000mm以下 埋め込み深さ：250mm以上 座金：下記の仕様の角座金または 同等以上の面積の座金とする。 全般は厚さ4.5mm、40mm角とする。 柱脚金物仕様が（に）、（ほ）、（へ）の 柱脚部は厚さ6.0mm、60mm角とする。
×	鋼製束

長期地耐力は20kN/m2以上とする。

立上り幅は t150 とする。

外周部地中梁はFG1とする。

内部地中梁はFG2とする。

底版は（FS15）とする。

底版いゝルは（+0.050） とする。（GLより）

は底版いゝルを示す。（GLより）

コンクリート強度はF_c=21N/mm²とする。

鉄筋種別はSD295A（D10〜D16）とする。

金物は同等品以上とする。

底版リスト

FS15 t=150
D13@200シング'ルクロス

基礎伏図 1/75

株式会社 Rbe architects 二級建築士事務所
二級 東京都知事登録 第 16330 号
二級 建築士登録 第 83516 号
渡 辺 隆 一

森田厚史邸新築工事



基礎伏図


1/75

S-06


藤田摂建築設計事務所

OSAMU FUJITA ARCHITECT+ASSOCIATES
一級建築士事務所 第2520号 / 一級建築士 第300013号 藤 田 摂

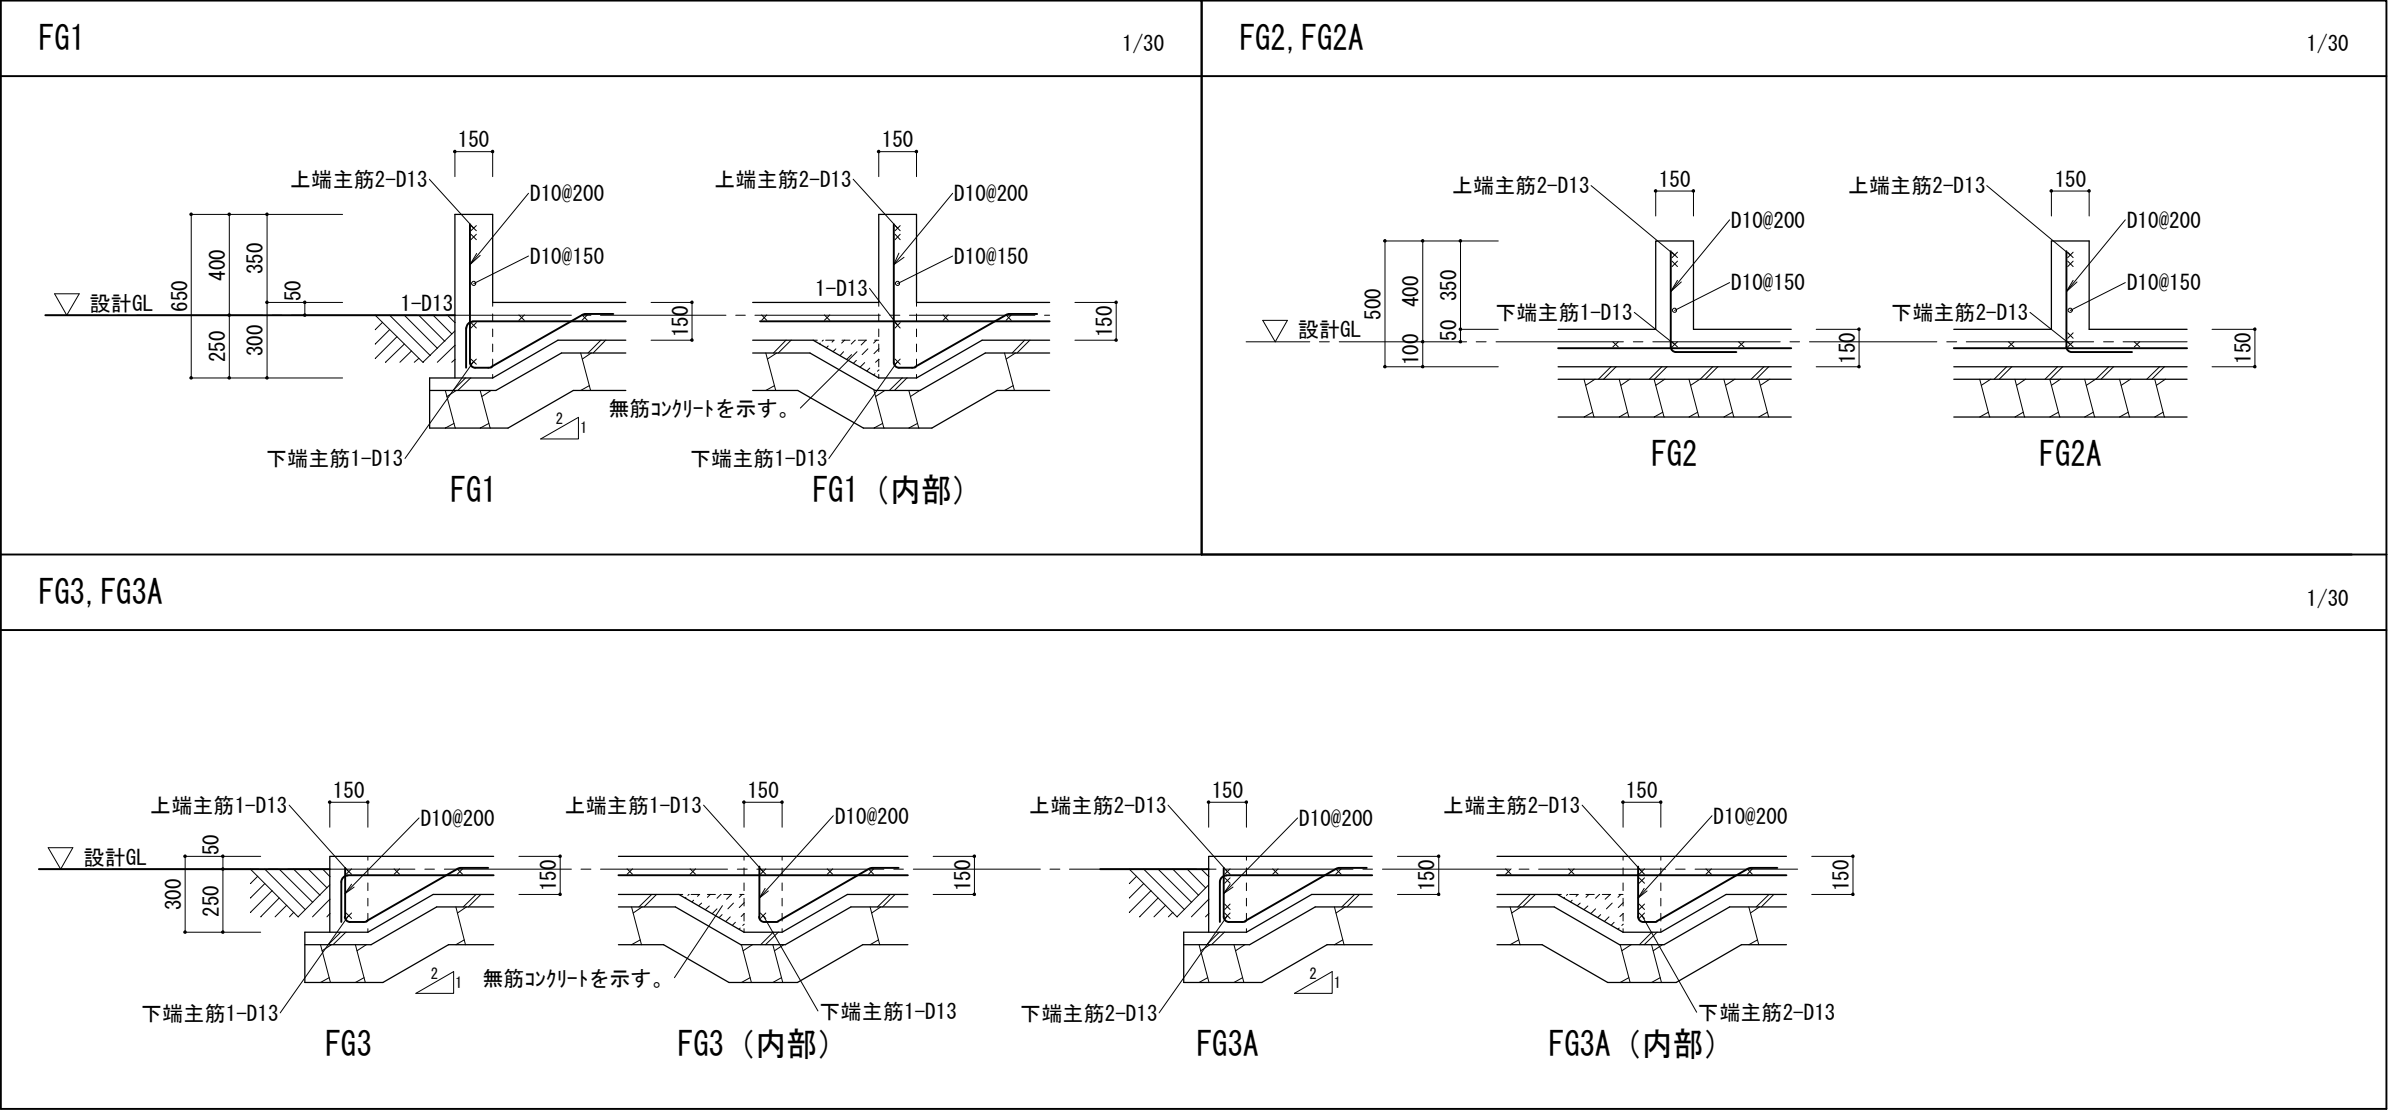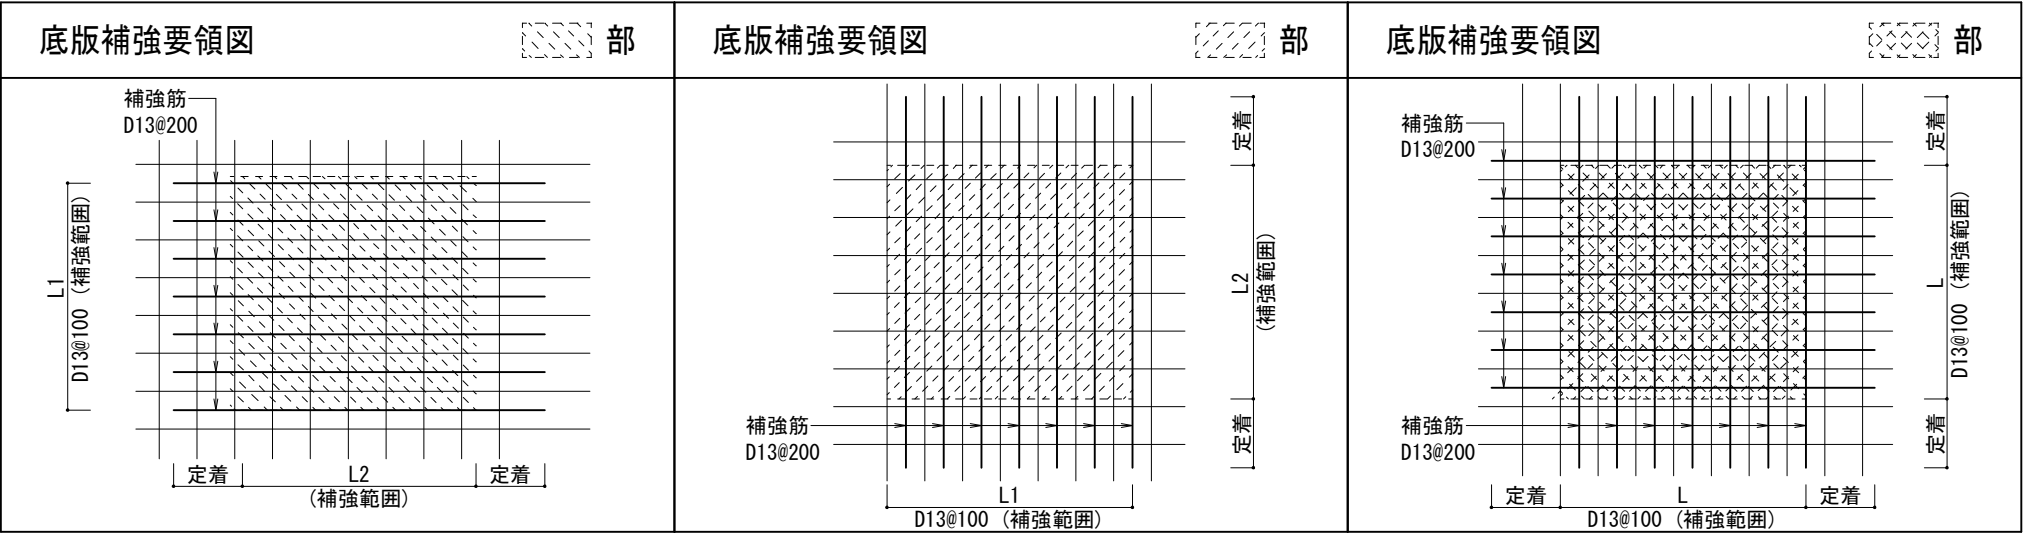

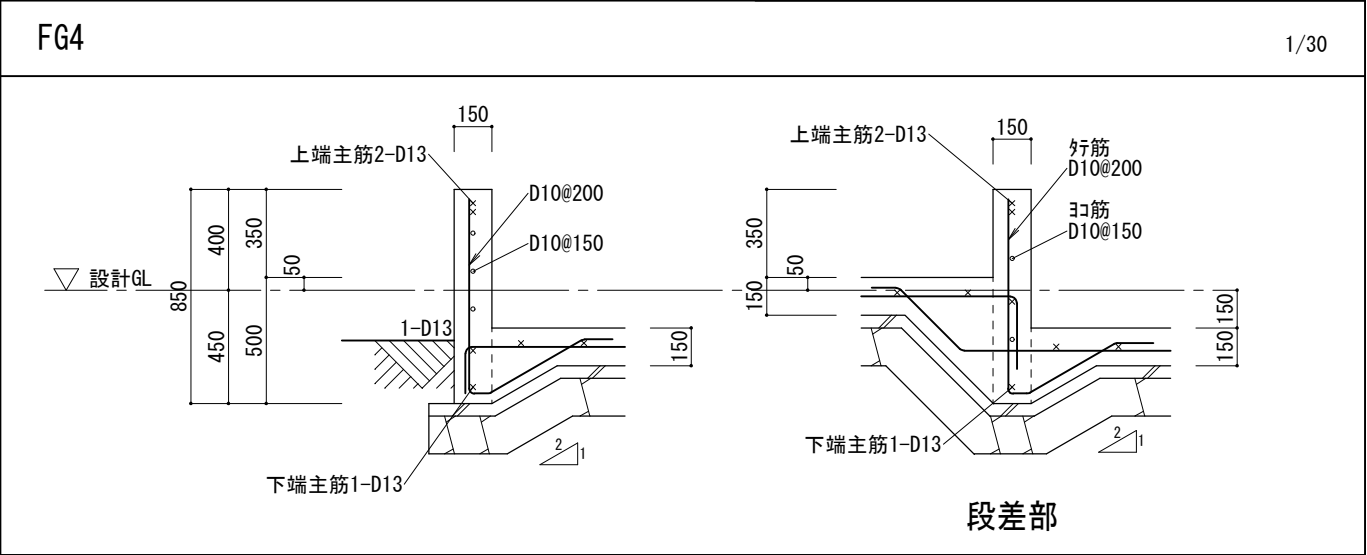



I型基礎リスト				1/30	C1 断面図	1/30	
符 号		C1					
1 階	BxD		450x150				
	全 域	断面					
		縦筋	3-D13(180° フック付き)				
		横筋	D10@200				

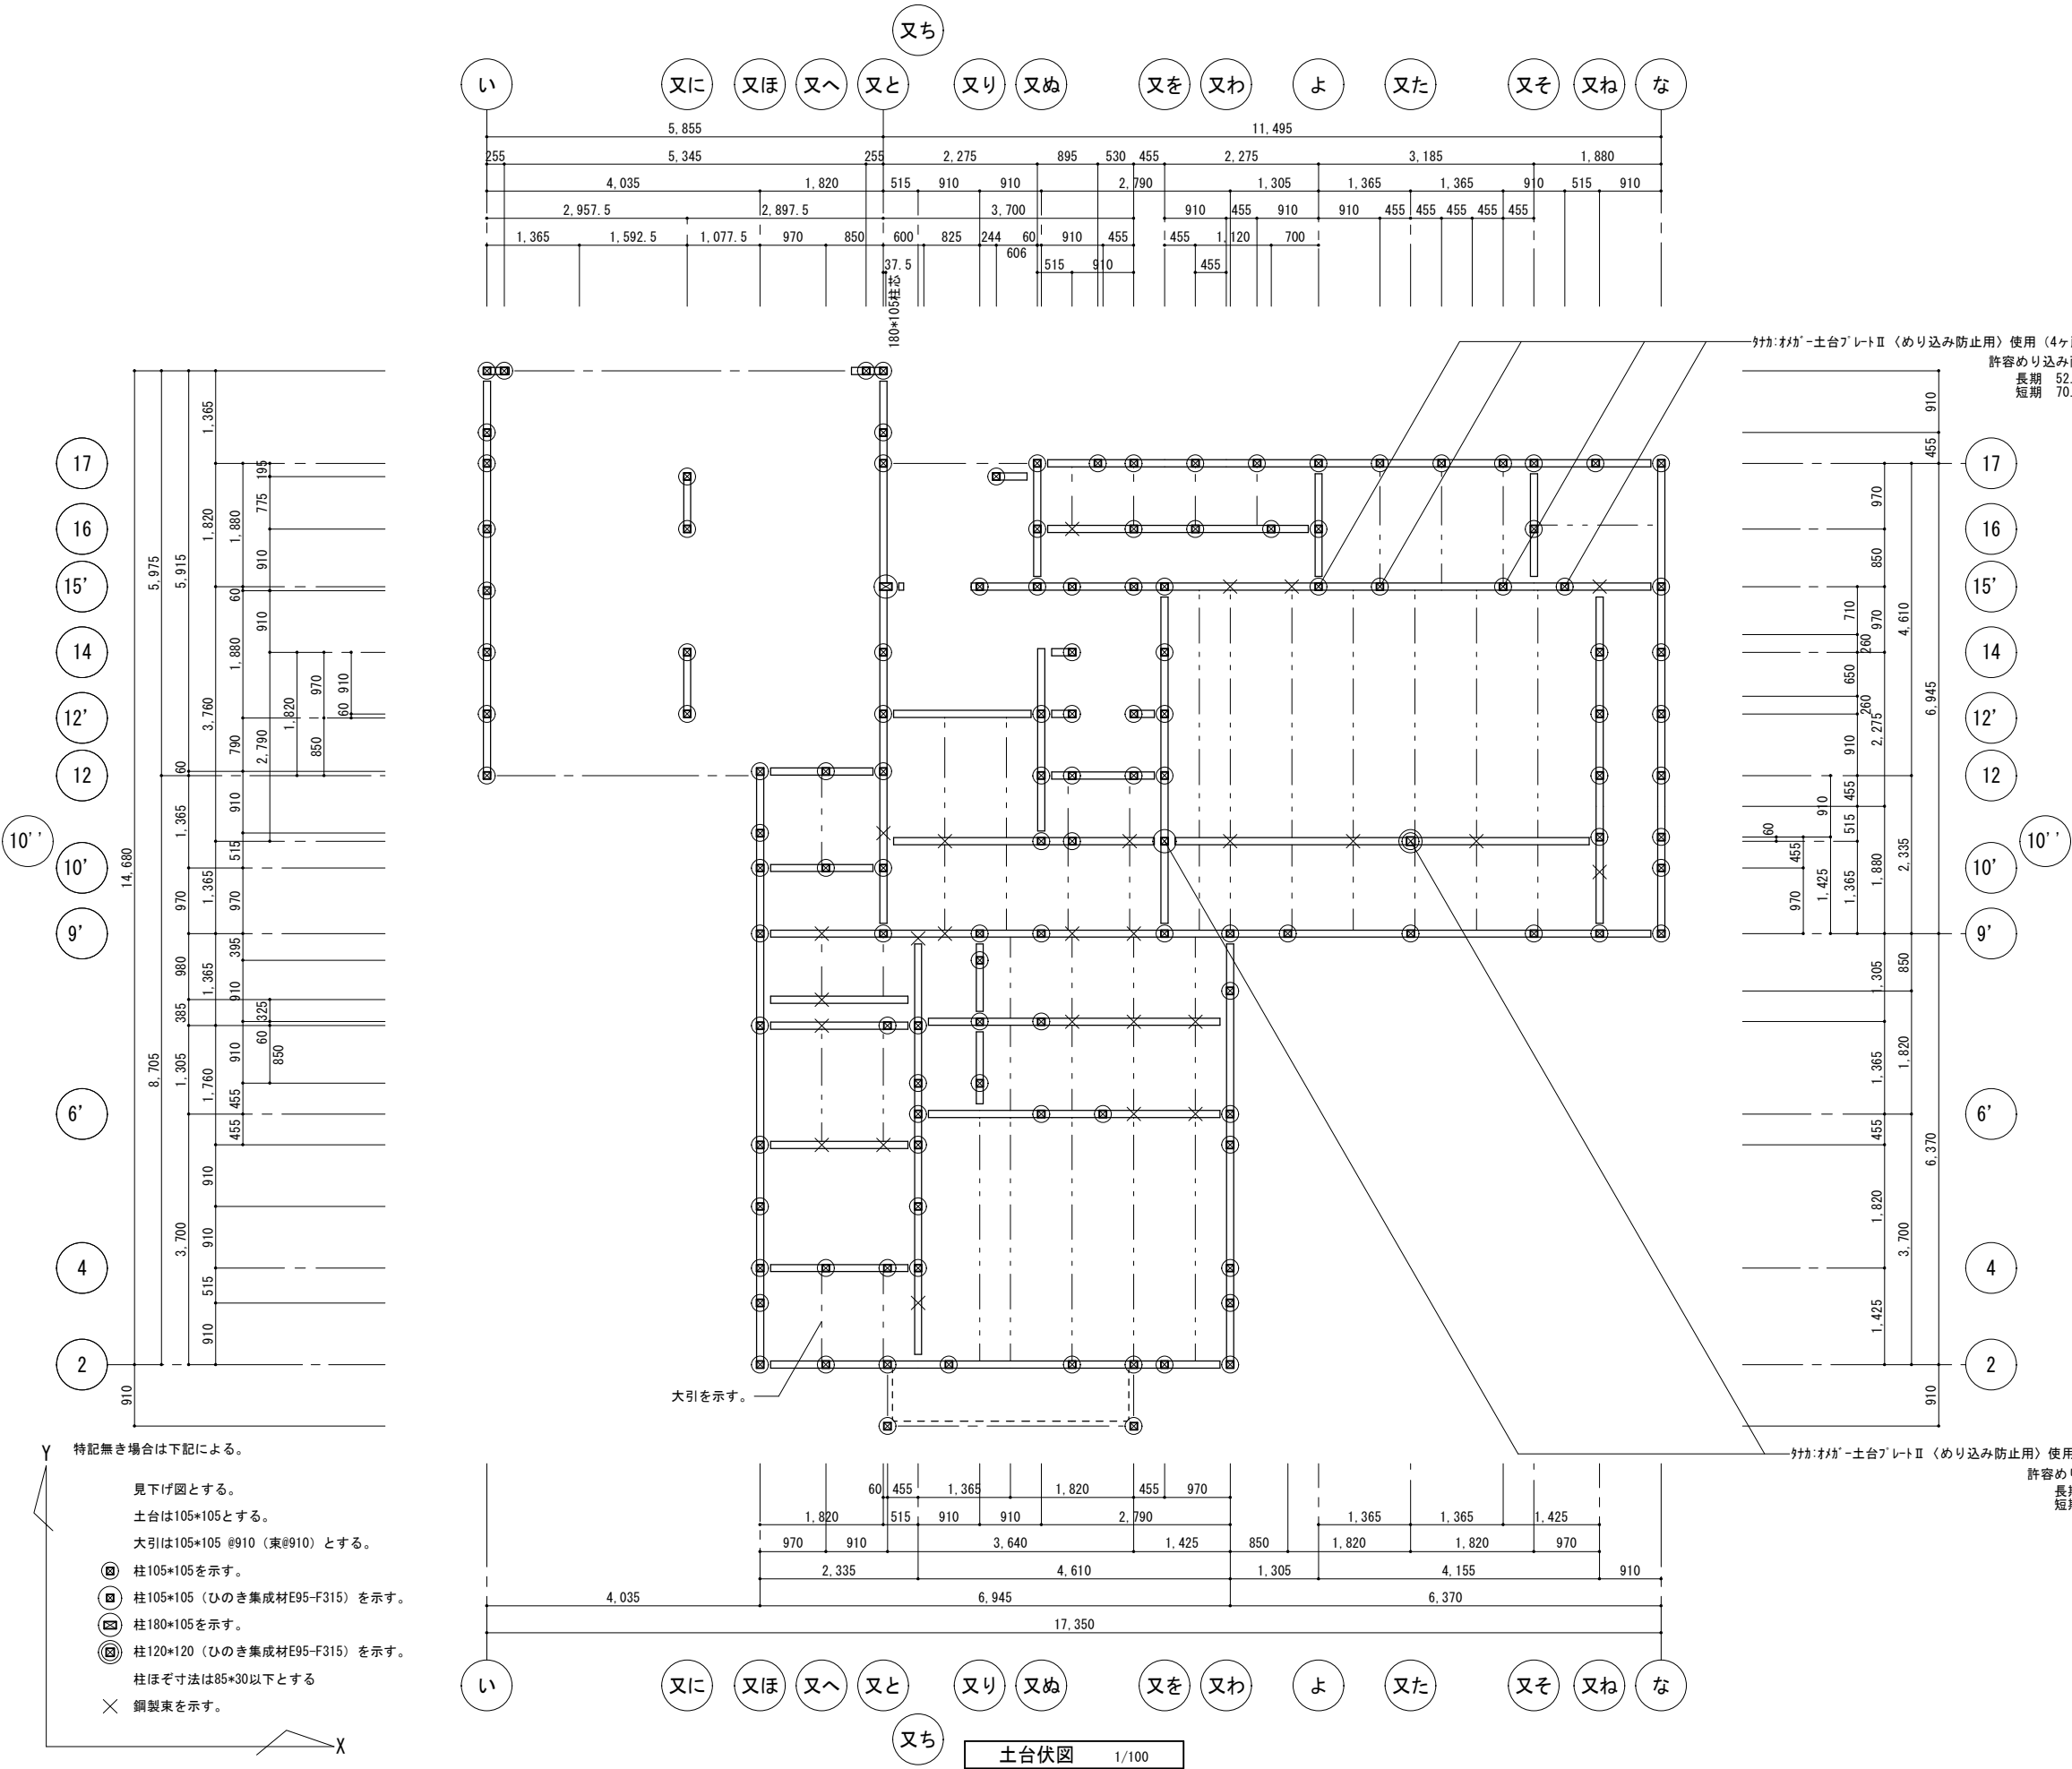

木 材 リ ス ト				
名称	樹 種	等 級	寸 法	備 考
土台	ひのき	無等級	105*105	
柱	杉	無等級	105*105	
〃	杉	無等級	180*105	
〃	集成材	E95F315 (同一等級)	105*105	ひのき (hg表記)
〃	集成材	E95F315 (同一等級)	120*120	ひのき (hg表記)
梁	杉	無等級	105*120	
〃	杉	無等級	105*150	
〃	杉	無等級	105*180	
〃	杉	無等級	105*210	
〃	杉	無等級	105*240	
〃	集成材	E105F300 (対称異等級)	105*210	欧州7か7 (hg表記)
〃	集成材	E105F300 (対称異等級)	105*240	欧州7か7 (hg表記)
〃	集成材	E105F300 (対称異等級)	105*270	欧州7か7 (hg表記)
〃	集成材	E105F300 (対称異等級)	105*330	欧州7か7 (hg表記)
〃	集成材	E105F300 (対称異等級)	105*360	欧州7か7 (hg表記)
〃	集成材	E105F300 (対称異等級)	105*420	欧州7か7 (hg表記)
〃	集成材	E120F330 (対称異等級)	120*450	米松 (hhg表記)
大引	杉	無等級	105*105	@910
筋交い	杉	無等級	45*90	
火打梁	杉	無等級	90*90	
小屋束	杉	無等級	105*105	
母屋	杉	無等級	105*105	@910
棟木	杉	無等級	105*105	
垂木	ひのき	無等級	45*90	@455


※リスト内は設計基準強度が同等以上の樹種に変更可能です。
設計基準強度は、(圧縮・引張・曲げ・せん断・ヤング係数)を示す。

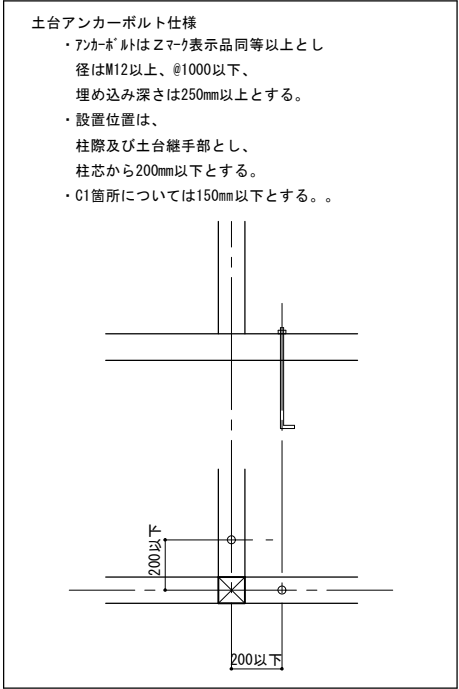

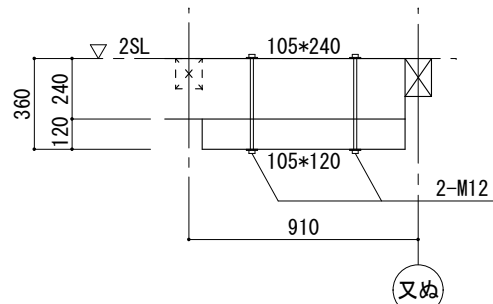


床下地は構造用合板24mmとする。

-  柱105×105を示す。
 柱105×105（ひのき集成材E95-F315）を示す。
 柱180×105を示す。
 柱120×120（ひのき集成材E95-F315）を示す。
 柱ほぞ寸法は85×30以下とする
 hgは欧州リッパ集成材E105-F300を示す。
 hhgは米松集成材E120-F330を示す。
 耐力壁を示し、（ ）は壁倍率を示す。
 梁端埋込Lは2SL-645mmとする。
 重ね梁とする。（詳細図参照。）

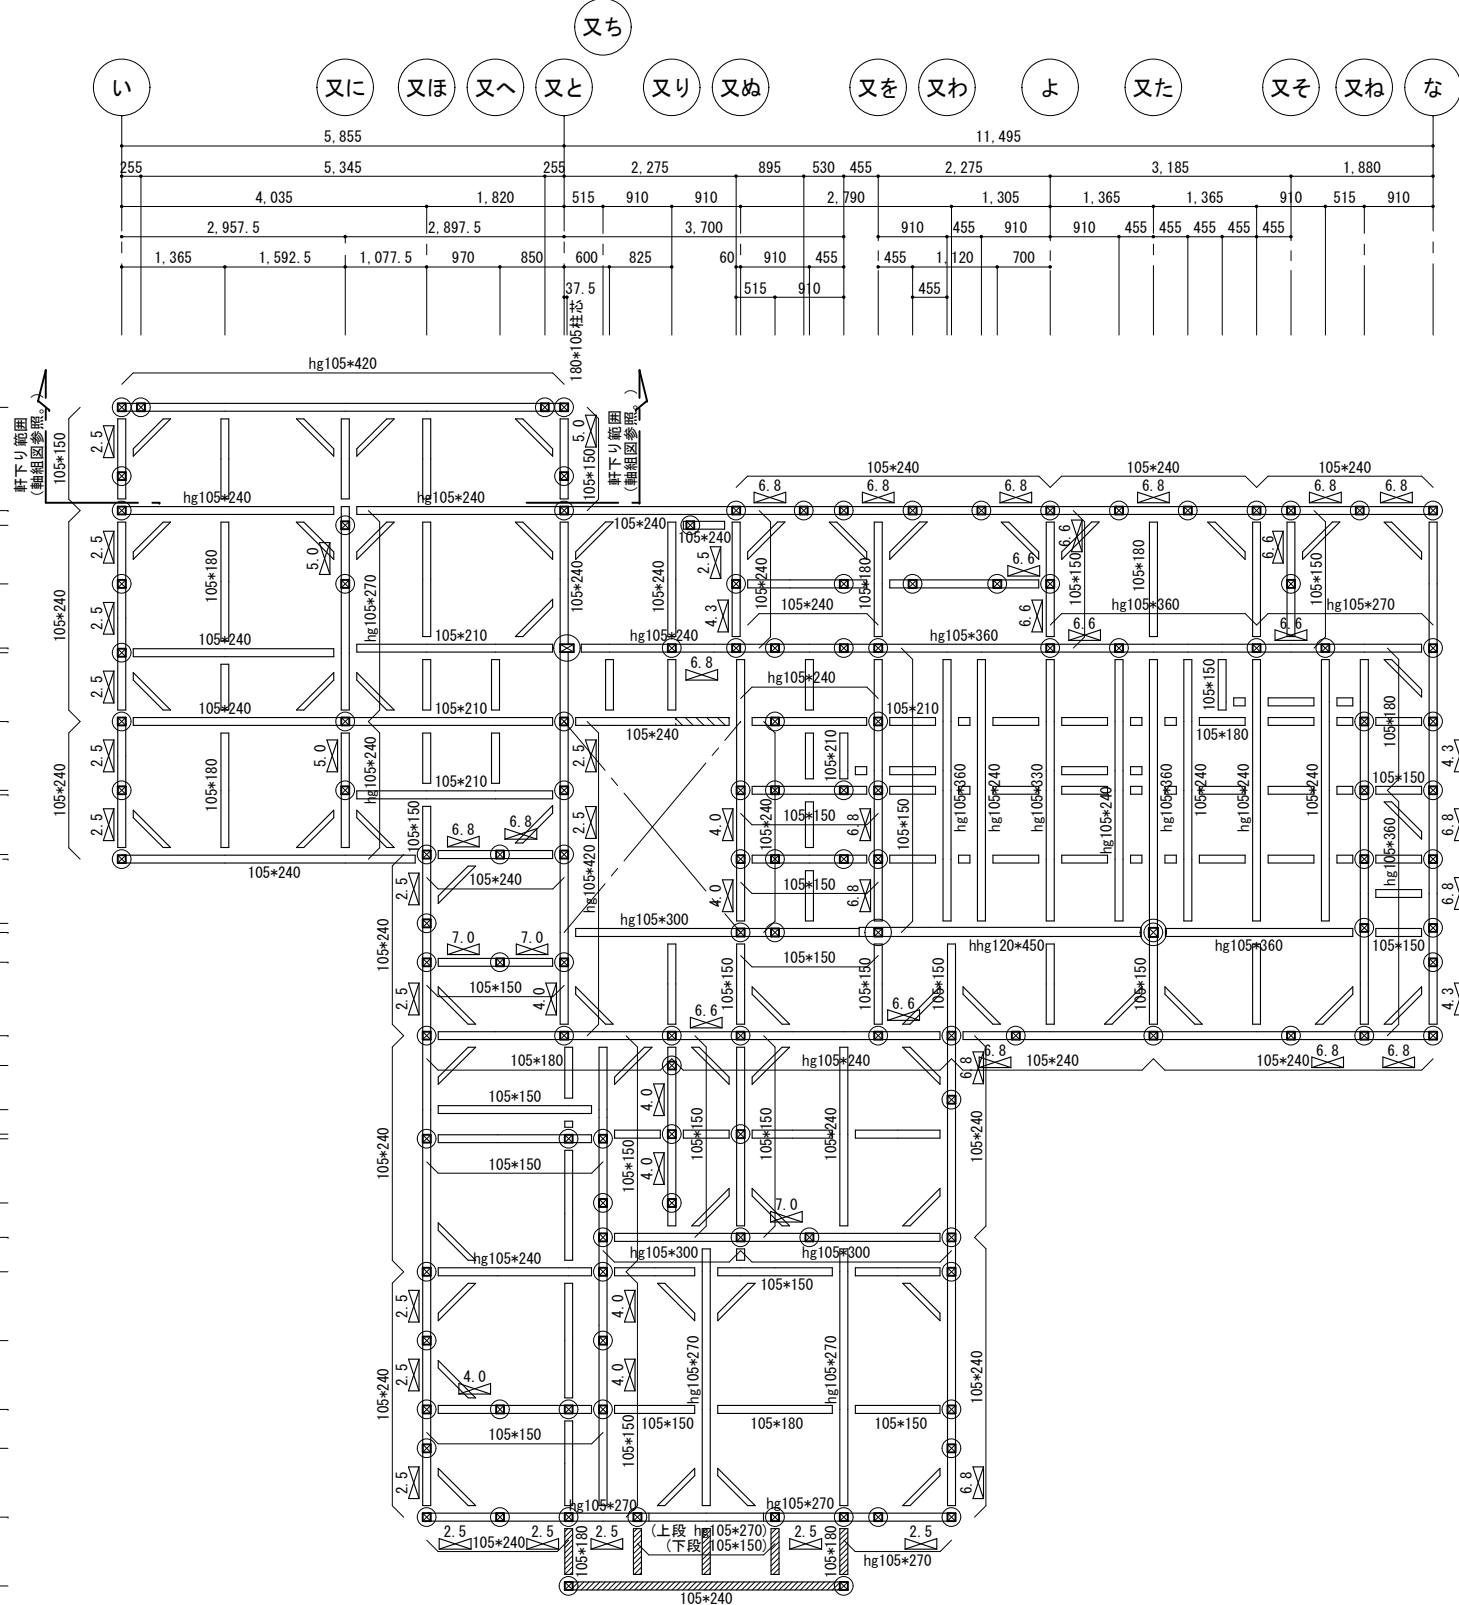

軒下り伏図、2SL伏図

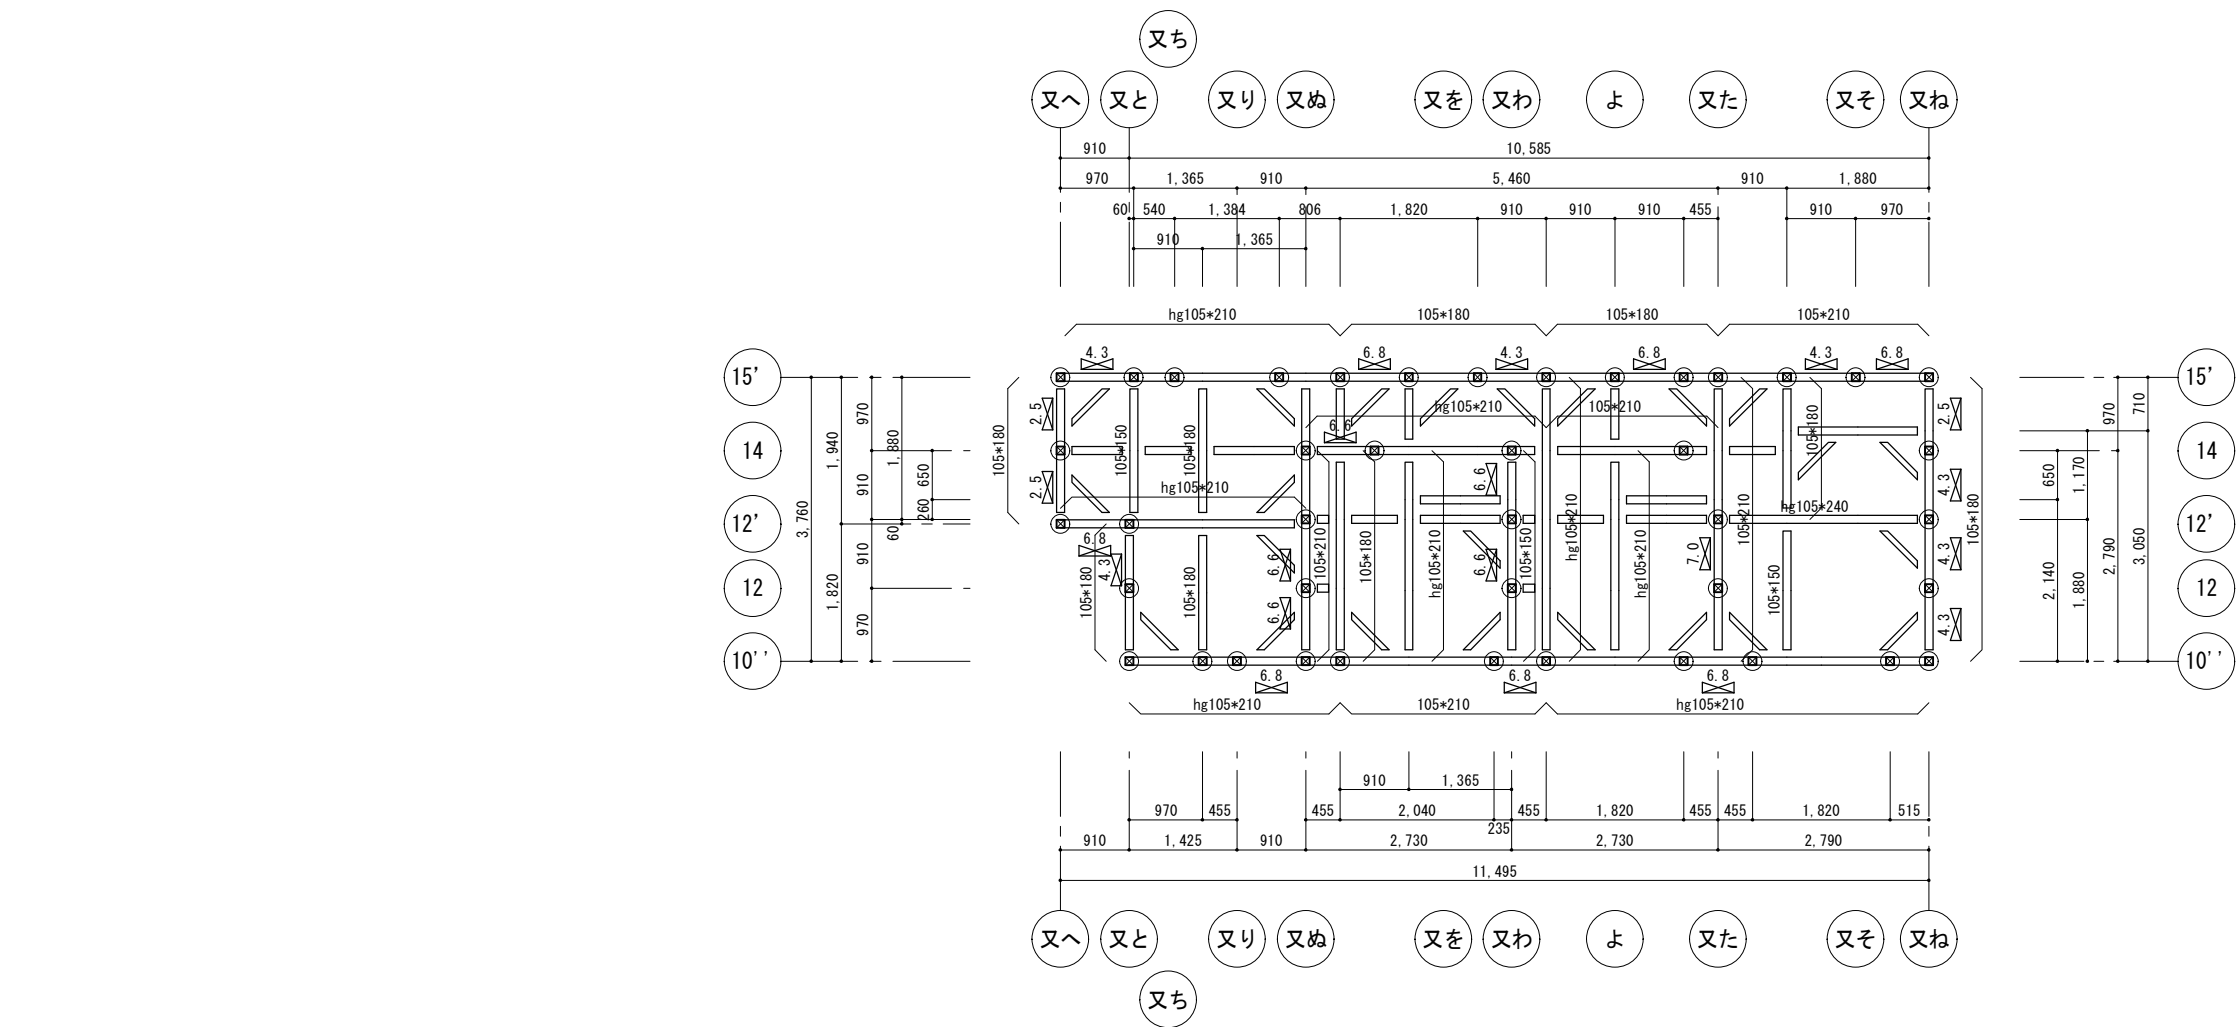

RFL伏図 1/100

特記無き場合は下記による。

見上げ図とする。

梁は105*120とする。

火打梁は90*90とする。

柱105*105を示す。

柱ほぞ寸法は85*30以下とする

hgは欧州7カマ集成材E105-F300を示す。

耐力壁を示し、()は壁倍率を示す。

耐力壁の仕様					
部位	記号	面材1	面材2	筋交い	
		仕様	仕様	仕様	倍率
外壁	2.5	スターウッド (構造用MDF) t=9	2.5	-	-
	4.3	スターウッド (構造用MDF) t=9	4.3	-	-
	5.0	スターウッド (構造用MDF) t=9	2.5	スターウッド (構造用MDF) t=9	2.5
	6.8	スターウッド (構造用MDF) t=9	4.3	構造用合板 t=9	2.5
	4.0	-	-	-	45*90㌢x 4.0
内壁	6.6	構造用合板 t=9	3.3	構造用合板 t=9	3.3
	6.8	タイガ-ハイバ-ハード T&Kスト(石膏ボード) t=12.5	2.8	-	45*90㌢x 4.0
	7.0	タイガ-ハイバ-ハード T&Kスト(石膏ボード) t=12.5	3.0	-	45*90㌢x 4.0

スターウッド (構造用MDF2.5倍) 釘仕様：面材張り大壁
構造用MDF N50を用いてピッチ150mm以下で柱・間柱・梁・桁・土台その他の横架材の片面に釘打ち(継目には受材を設けて釘打ち)

スターウッド (構造用MDF4.3倍) 釘仕様：面材張り大壁
構造用MDF N50を用いて外周@75mm以下、中通り@150mm以下で柱・間柱・梁・桁・土台その他の横架材の片面に釘打ち(継目には受材を設けて釘打ち)


構造用合板仕様(屋内側)：受材仕様真壁 (2.5倍)
受材 30mm x 40mm以上を柱・土台・横架材にN75ピッチ300mm以下で釘打ち。
合板 N50を用いてピッチ150mm以下で受材・間柱に釘打ち。


構造用合板仕様(屋内側)：受材仕様真壁 (3.3倍)
受材 30mm x 40mm以上を柱・土台・横架材にN75ピッチ200mm以下で釘打ち。
合板 CN50を用いて、外周部ピッチ75mm以下で受材に釘打ち、
その他の部分はピッチ150mm以下で受材等に釘打ち。

タイガ-ハイバ-ハード T&Kスト 入隅部 ビス仕様(倍率2.8)：床勝ち仕様大壁(認定品：認定FRM-0738)
DTSN32を用い、外周@75mm以下、中通り@150mm以下で受材、間柱、胴つなぎ等に打ちつけ。


タイガ-ハイバ-ハード T&Kスト 一般部 ビス仕様(倍率3.0)：床勝ち仕様大壁(認定品：認定FRM-0737)
DTSN32を用い、外周@75mm以下、中通り@150mm以下で受材、間柱、胴つなぎ等に打ちつけ。

Y
特記無き場合は下記による。
見下げ図とする。
棟木・母屋は105*105 @910とする。
垂木は45*90 @455とする。
垂木の断面欠損はなしとする。
野地板は構造用合板12mmとする。
屋根仕様はS3とする。(S-05木工事・軸組工法工事 標準仕様書3参照。)
くも筋交いは13*90以上とし、
XY方向共 @2,000以下かつ、耐力壁上部に配置する。
外壁は屋根面まで合板張りとする。
○ 東位置を示す。
X

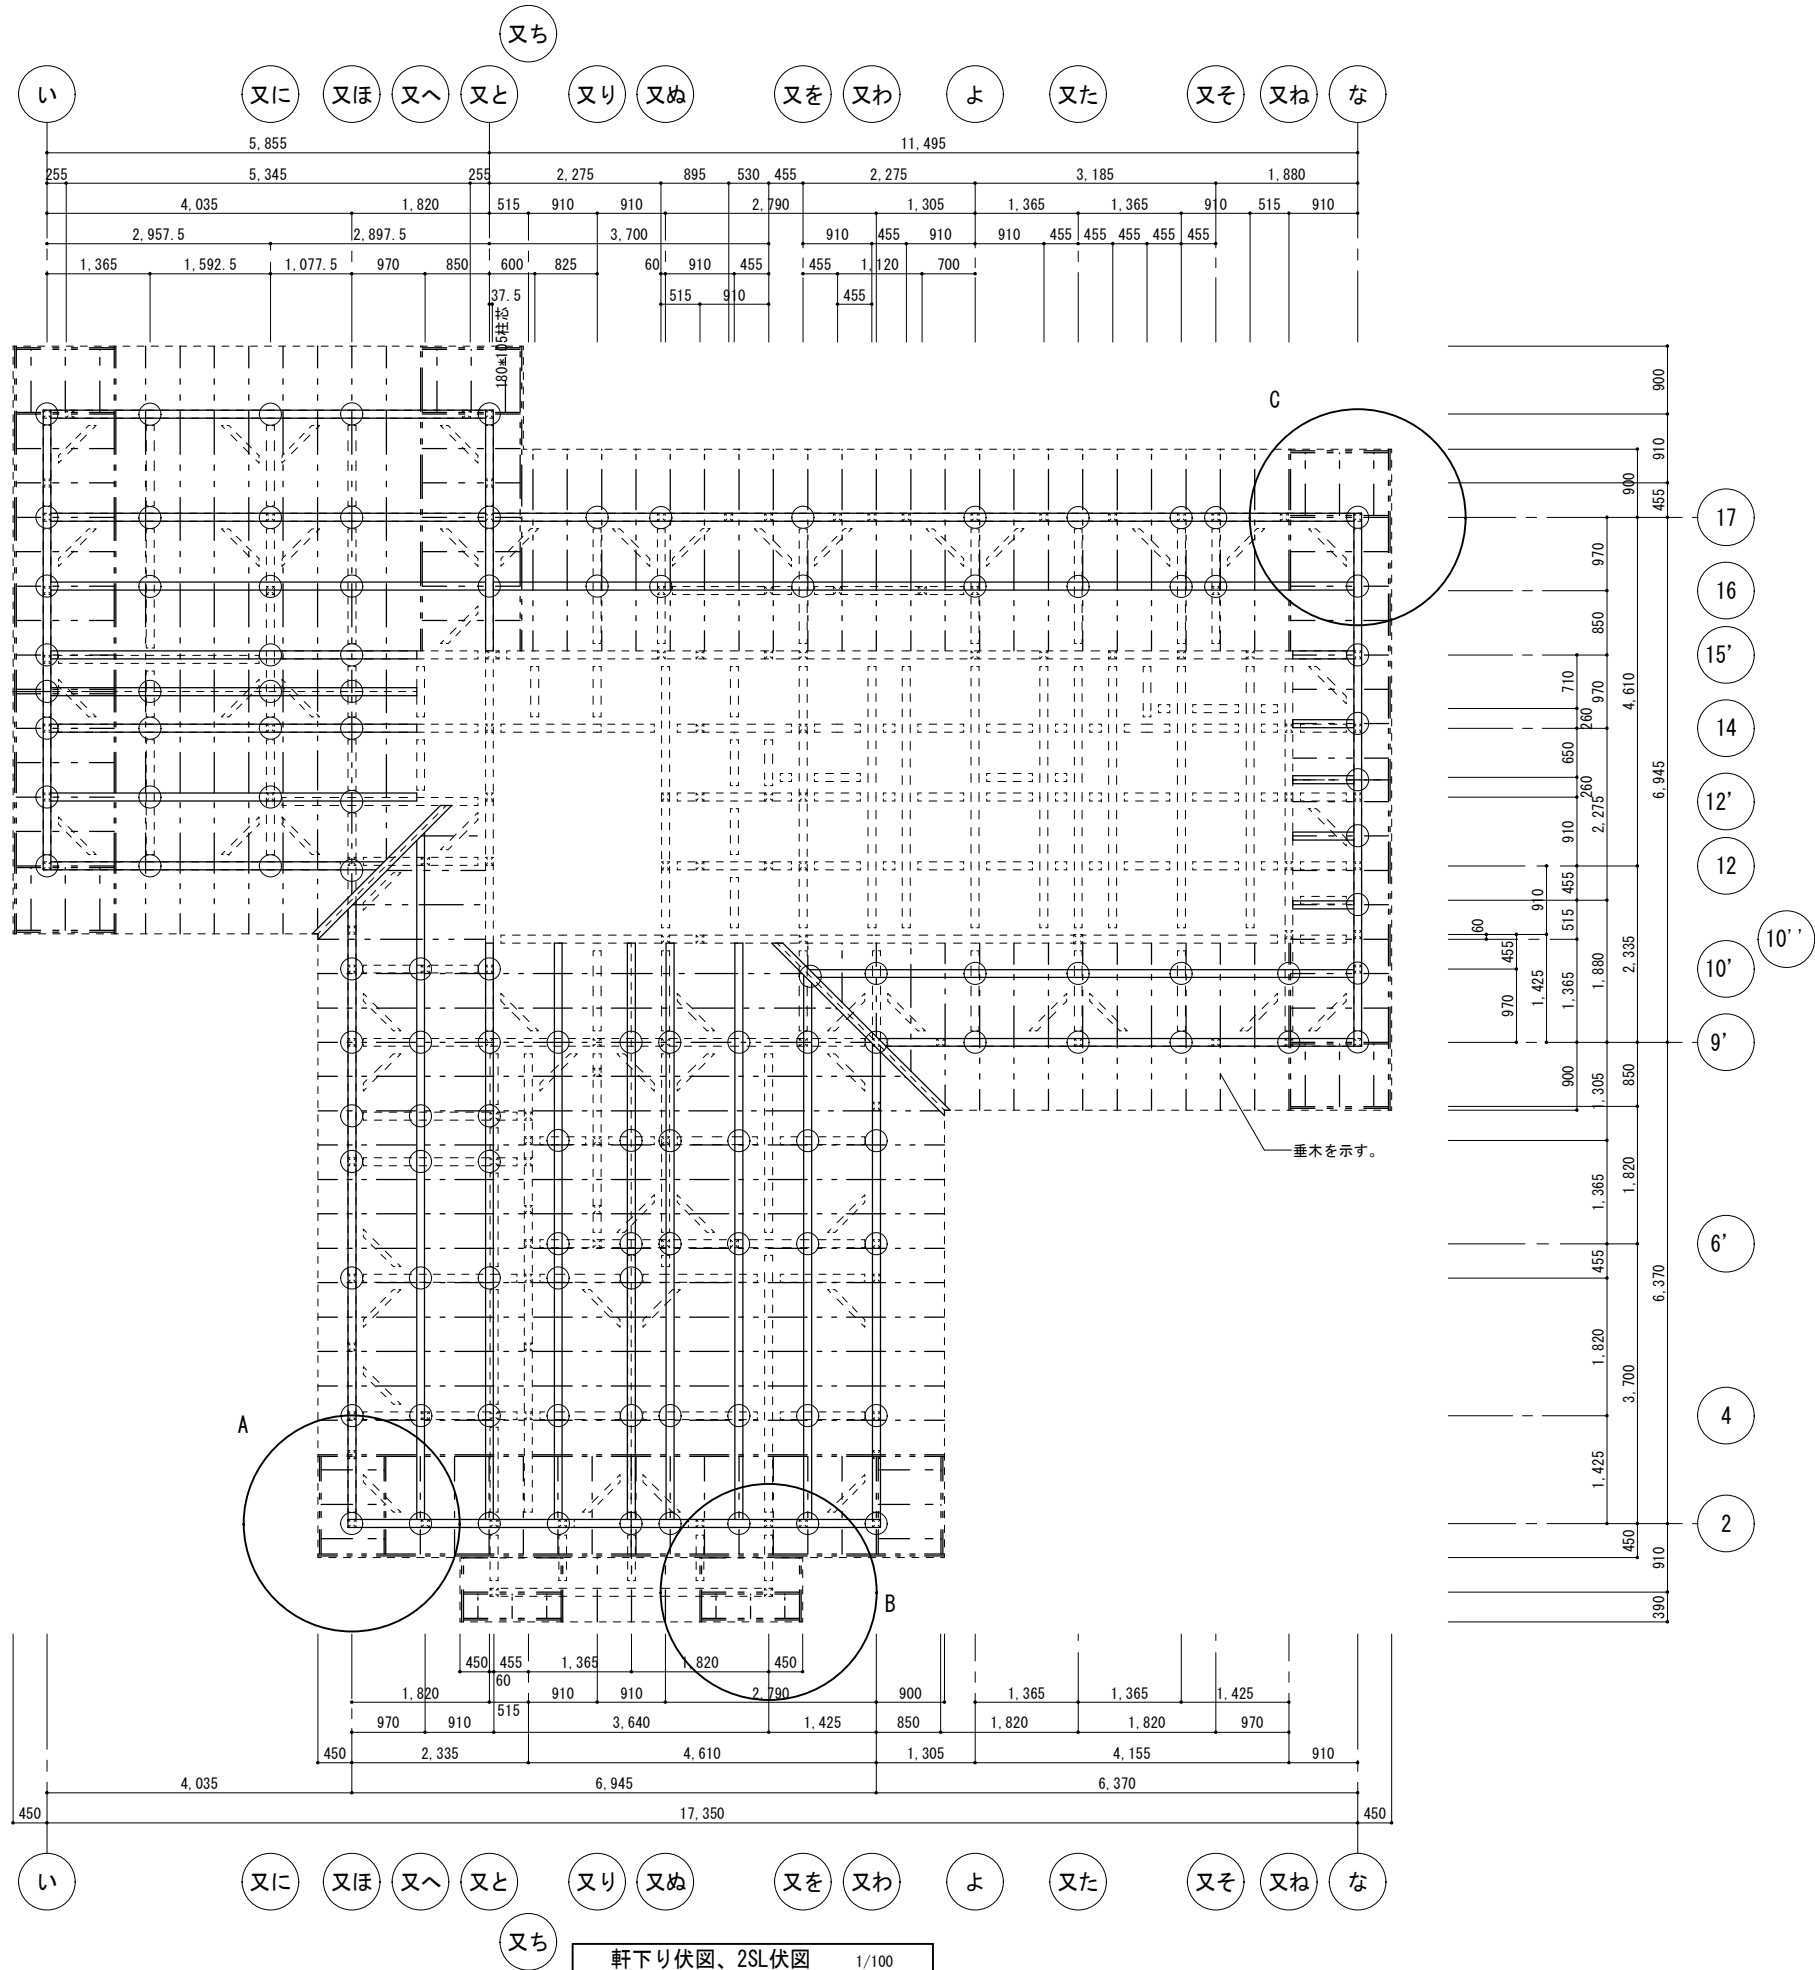


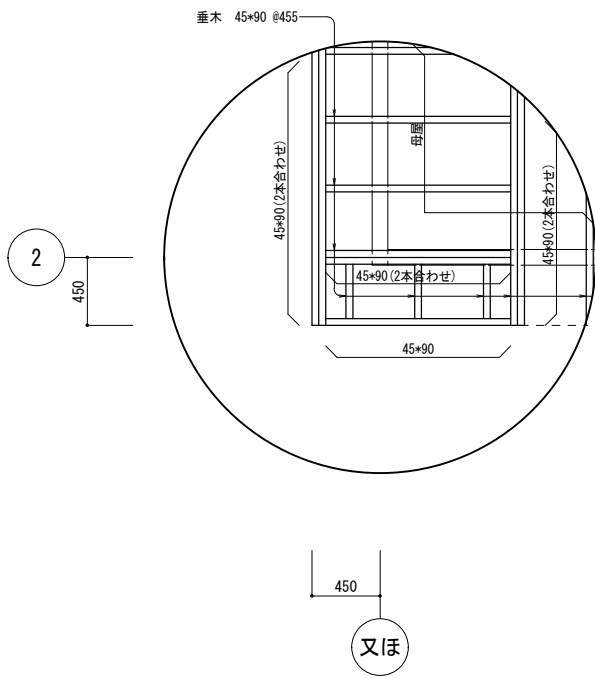


軒先部詳細図A 1/50

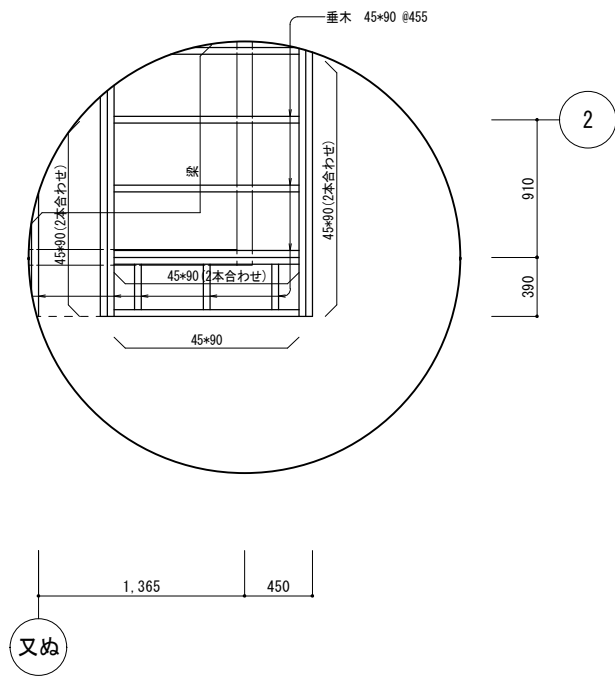

軒先部詳細図B 1/50

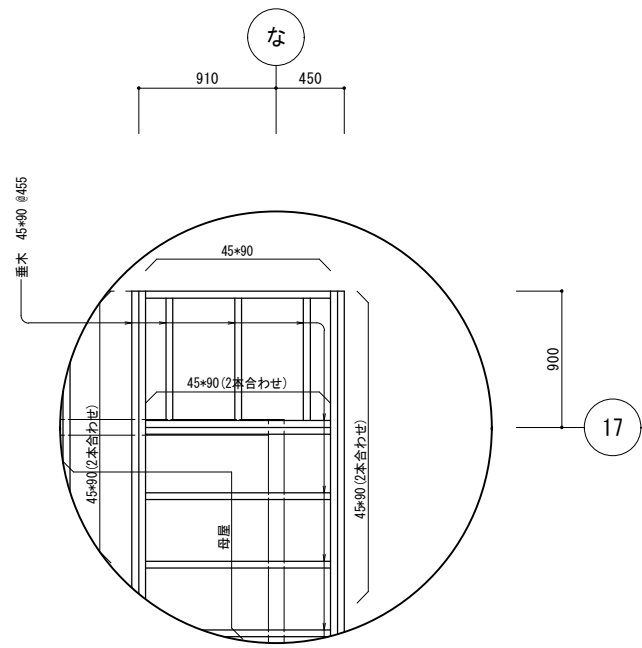


軒先部詳細図C 1/50

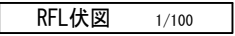


株式会社 R-be architects 二級建築士事務所
二級 東京都知事登録 第 16330 号
二級 建築士登録 第 83516 号
渡 辺 隆 一

OSAMU FUJITA ARCHITECT+ASSOCIATES
 藤田十衛事務所 第2520号 / 一級建築士 第200012号 藤田 伊

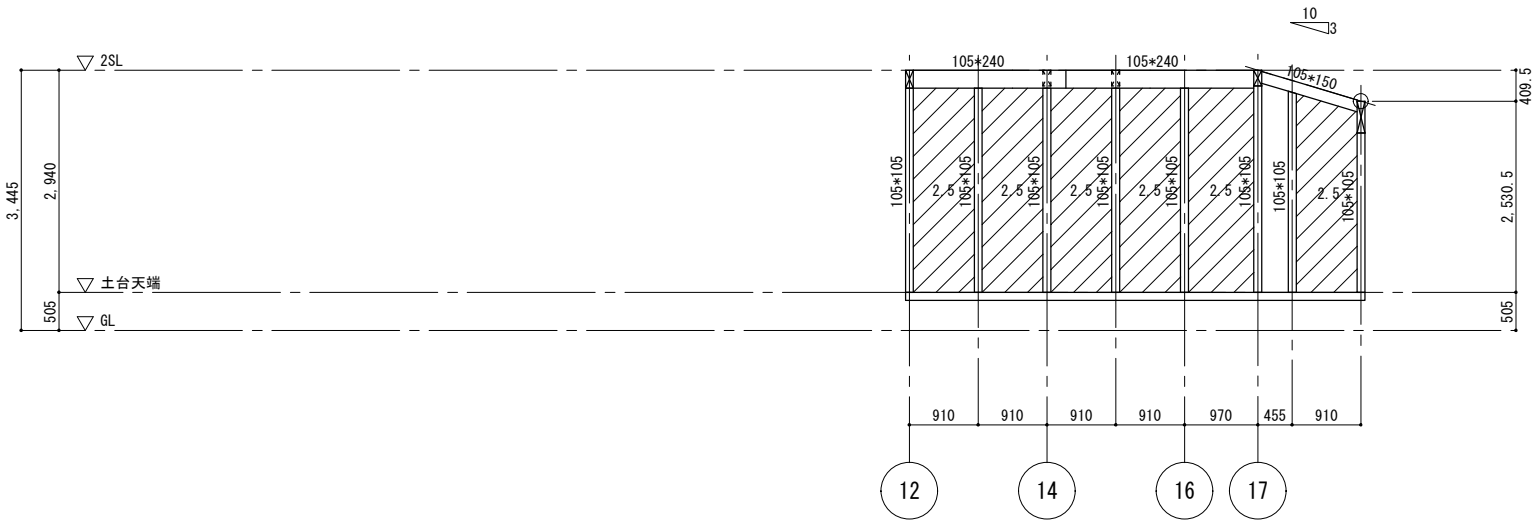

い通軸組図 1/100

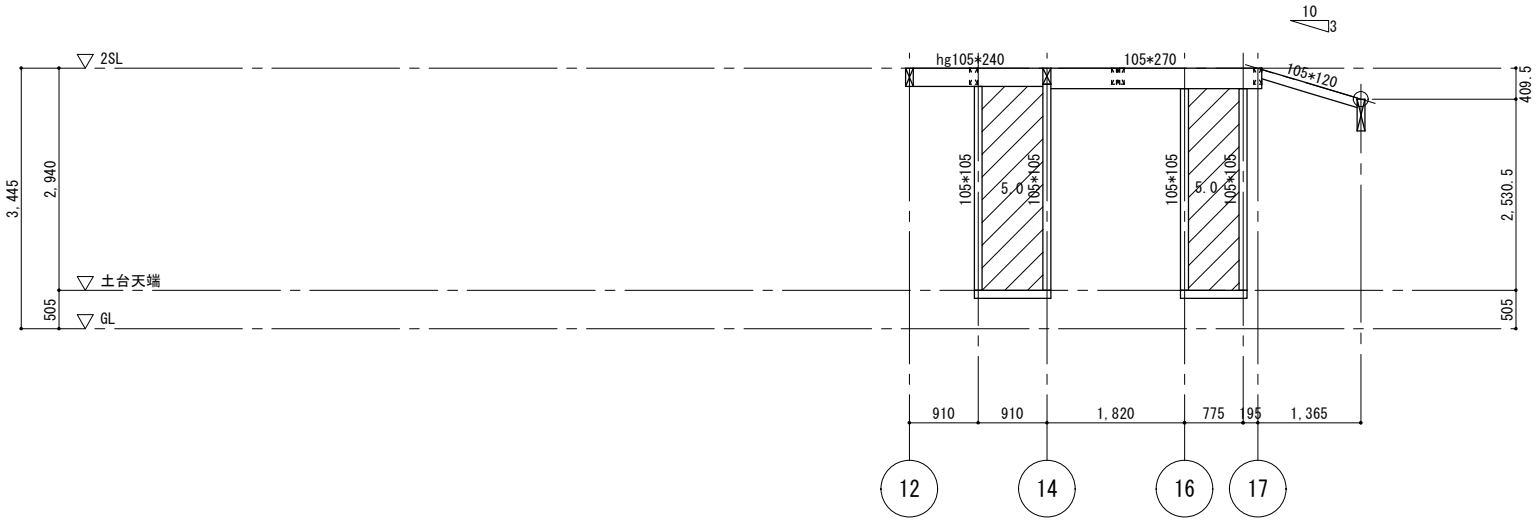

又に通軸組図 1/100

特記無き場合は下記による。

土台:105*105

は壁倍率を示す。

株式会社 Rbe architects 二級建築士事務所
二級 東京都知事登録 第 16330 号
二級 建築士登録 第 83516 号
渡 辺 隆 一

森田厚史邸新築工事


軸組図1

1/100

S-13

藤田摂建築設計事務所

OSAMU FUJITA ARCHITECT+ASSOCIATES
一級建築士事務所 第2520号 / 一級建築士 第300013号 藤 田 摂

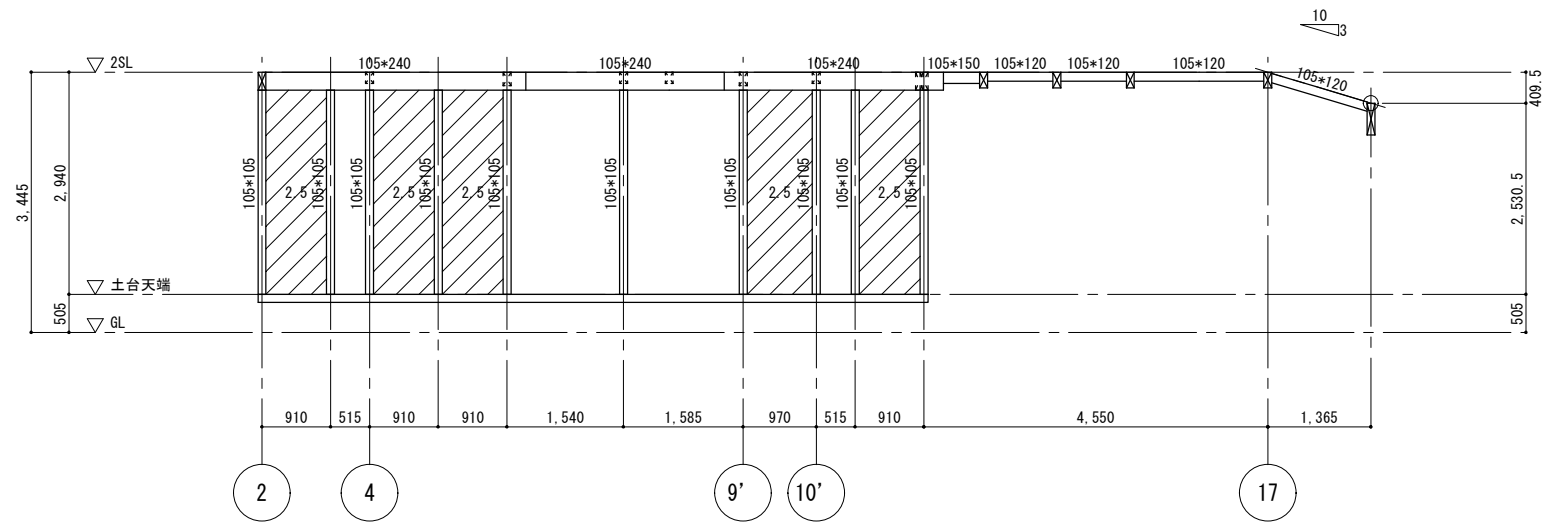

又ほ通軸組図 1/100



又へ通軸組図 1/100

特記無き場合は下記による。

土台:105*105

は壁倍率を示す。

株式会社 Rbe architects 二級建築士事務所
二級 東京都知事登録 第 16330 号
二級 建築士登録 第 83516 号
渡 辺 隆 一

森田厚史邸新築工事


軸組図2

1/100


S-14

藤田摂建築設計事務所

OSAMU FUJITA ARCHITECT+ASSOCIATES
一級建築士事務所 第2520号 / 一級建築士 第300013号 藤 田 摂

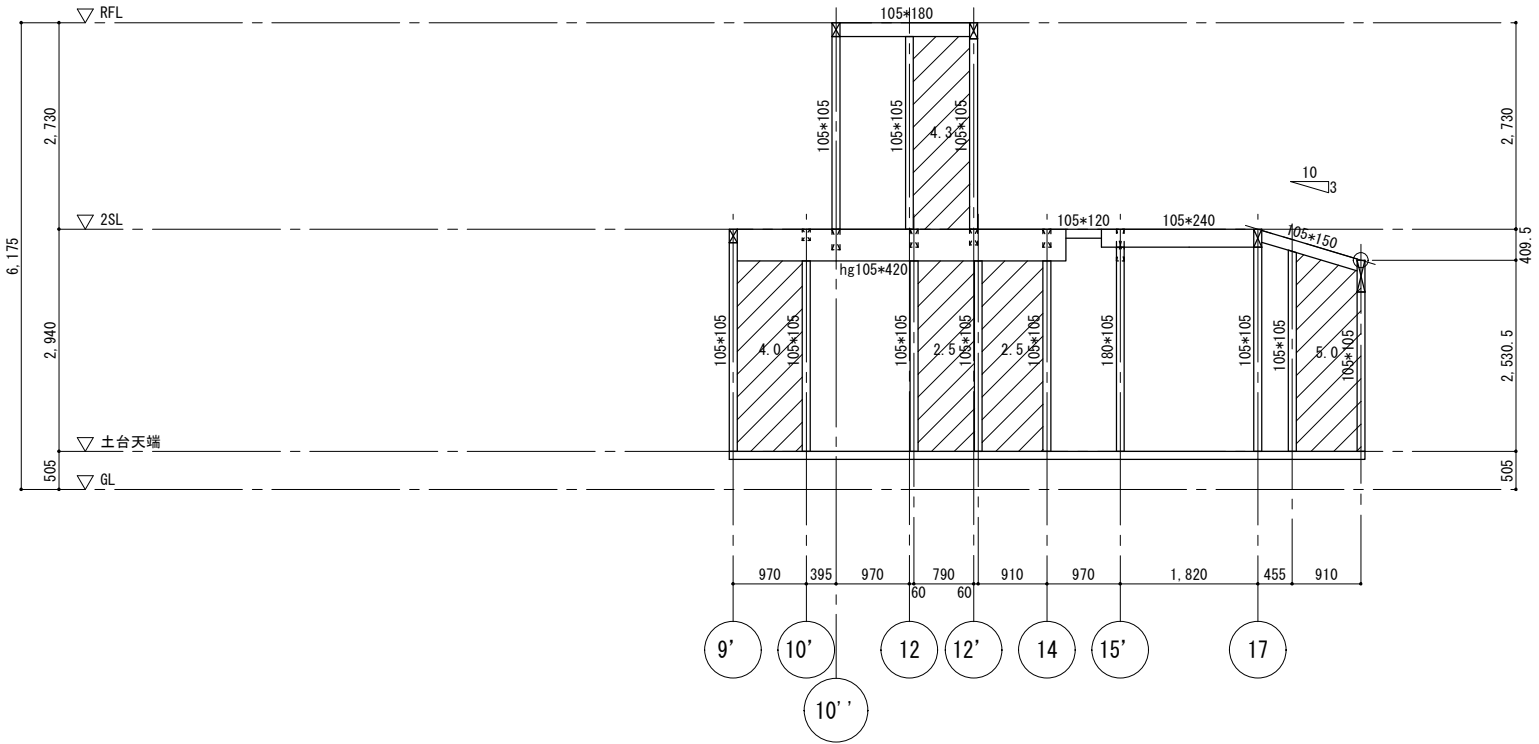

又と通軸組図 1/100

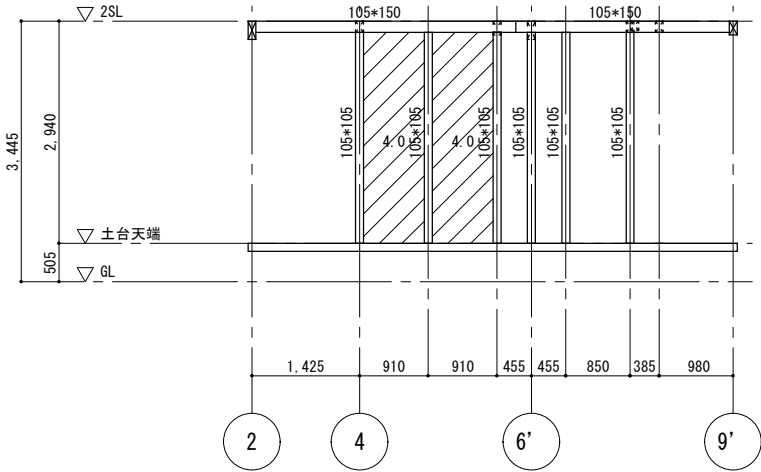

又ち通軸組図 1/100

特記無き場合は下記による。

土台:105*105

〰 (〰) は壁倍率を示す。

株式会社 Rbe architects 二級建築士事務所
二級 東京都知事登録 第 16330 号
二級 建築士登録 第 83516 号
渡 辺 隆 一

森田厚史邸新築工事


軸組図3

1/100


S-15

藤田摂建築設計事務所

OSAMU FUJITA ARCHITECT+ASSOCIATES
一級建築士事務所 第2520号 / 一級建築士 第300013号 藤 田 摂

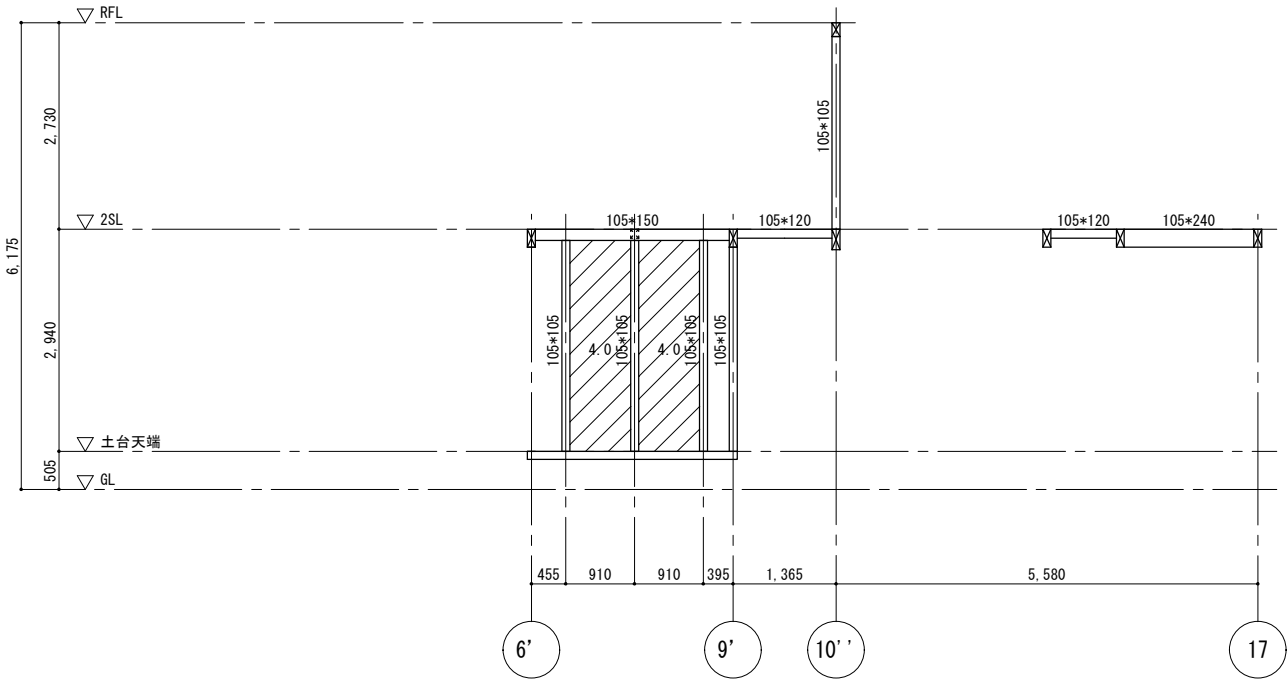

又り通軸組図 1/100

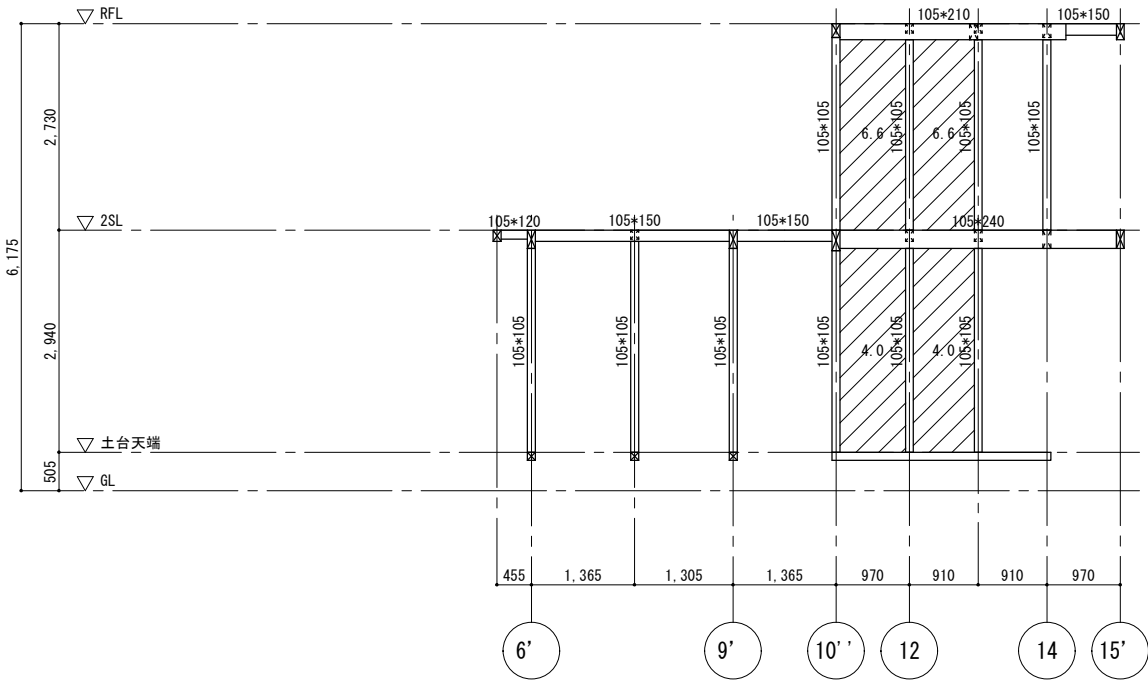

又ぬ通軸組図 1/100

特記無き場合は下記による。

土台:105*105

は壁倍率を示す。

株式会社 Rbe architects 二級建築士事務所
二級 東京都知事登録 第 16330 号
二級 建築士登録 第 83516 号
渡 辺 隆 一

森田厚史邸新築工事


軸組図4

1/100


S-16

藤田摂建築設計事務所


OSAMU FUJITA ARCHITECT+ASSOCIATES
一級建築士事務所 第2520号 / 一級建築士 第300013号 藤 田 摂

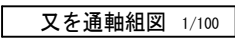

 () は壁倍率を示す。

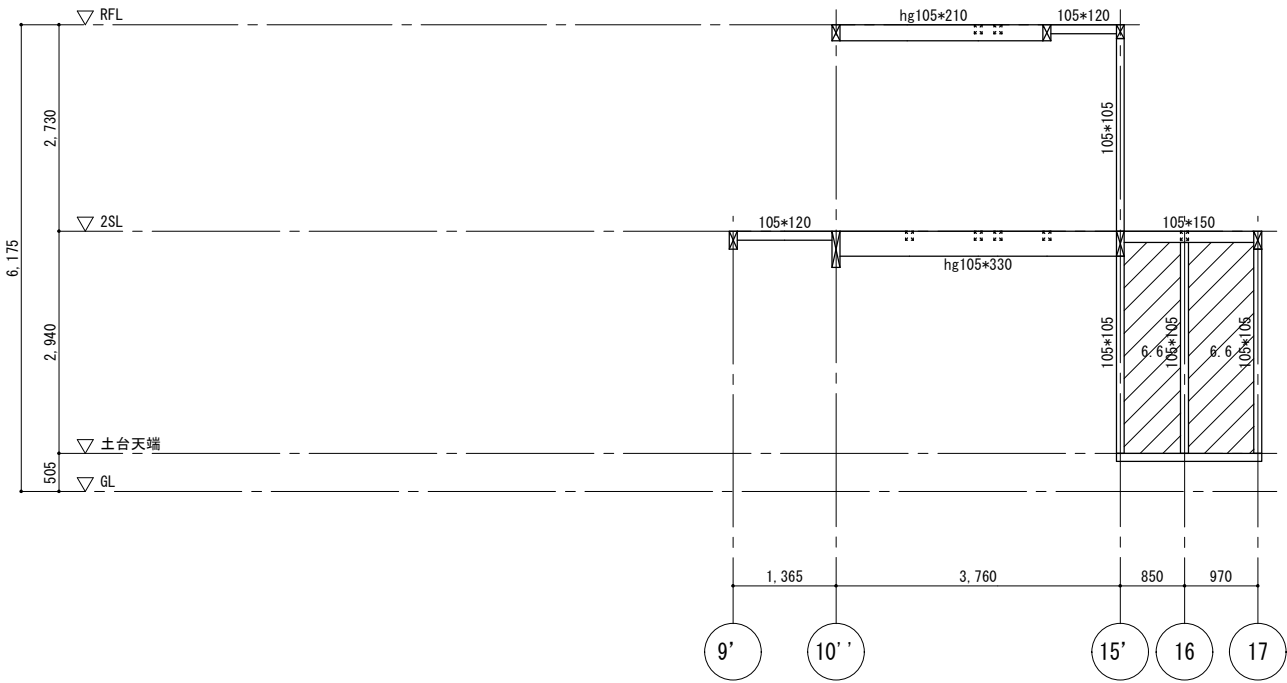

よ通軸組図 1/100


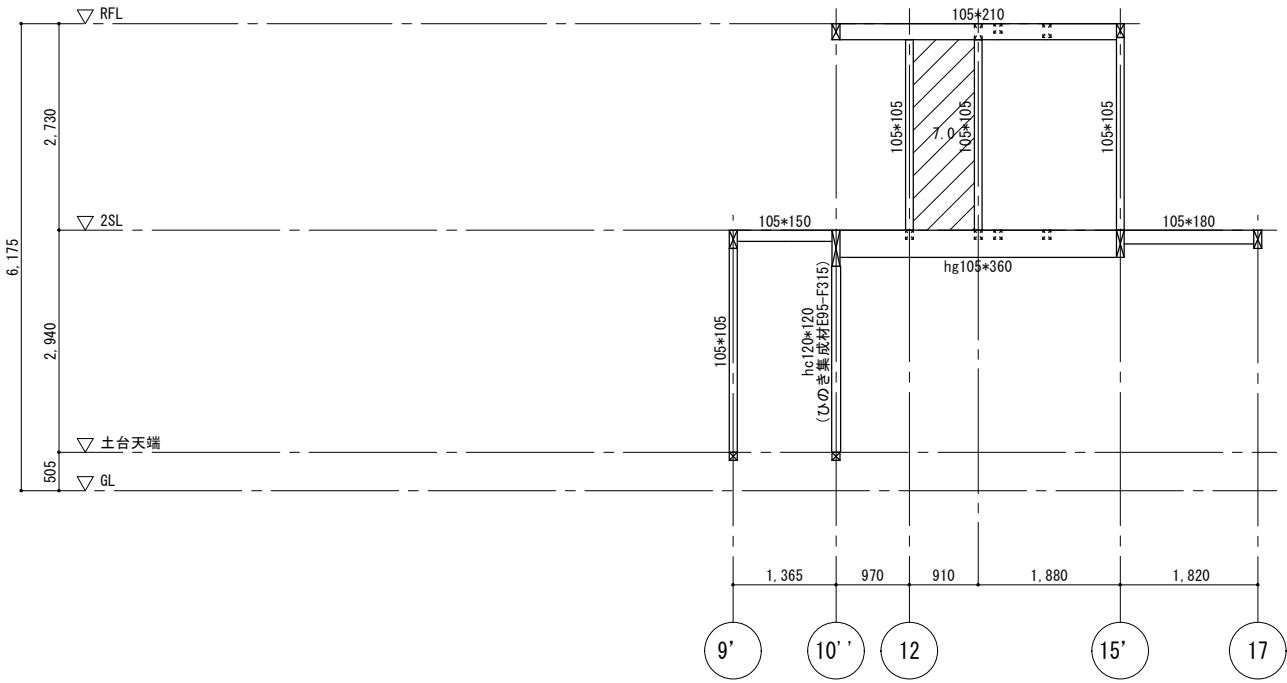


又た通軸組図 1/100


特記無き場合は下記による。

土台:105*105

（斜線）は壁倍率を示す。

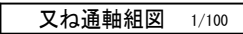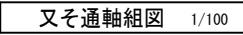

 () は壁倍率を示す。

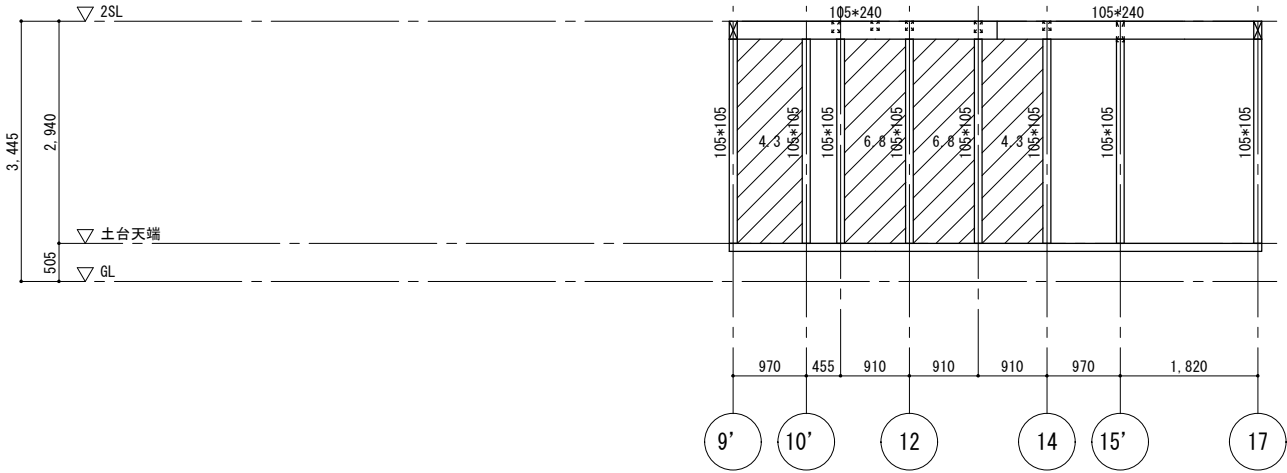

な通軸組図 1/100

特記無き場合は下記による。

土台:105*105

（ ）は壁倍率を示す。

株式会社 Rbe architects 二級建築士事務所
二級 東京都知事登録 第 16330 号
二級 建築士登録 第 83516 号
渡 辺 隆 一

森田厚史邸新築工事


軸組図8

1/100


S-20

藤田摂建築設計事務所

OSAMU FUJITA ARCHITECT+ASSOCIATES
一級建築士事務所 第2520号 / 一級建築士 第300013号 藤 田 摂

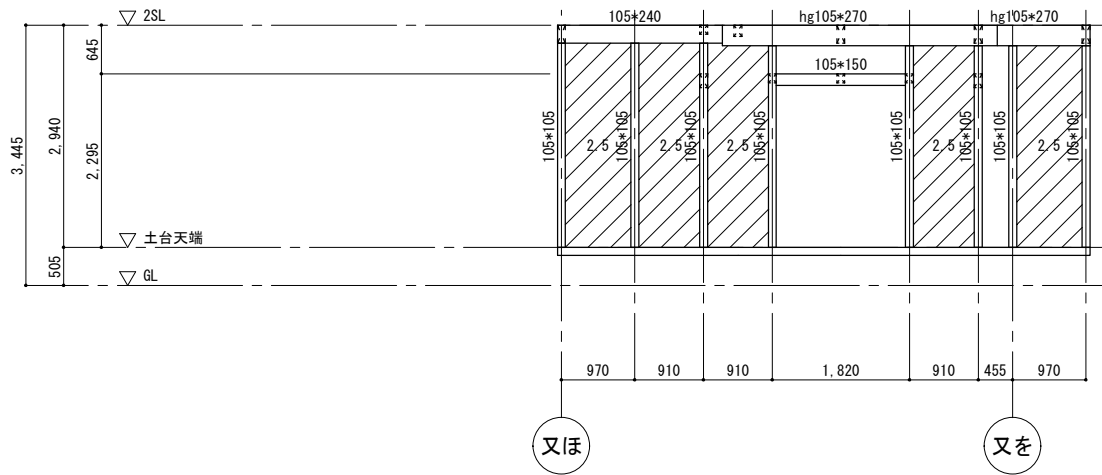

2通軸組図 1/100

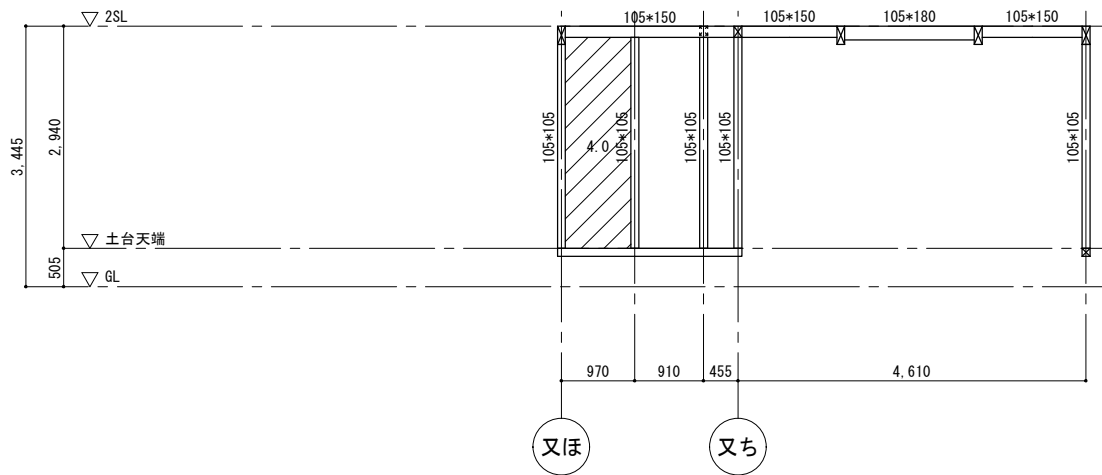


4通軸組図 1/100


特記無き場合は下記による。

土台:105*105

斜線()は壁倍率を示す。

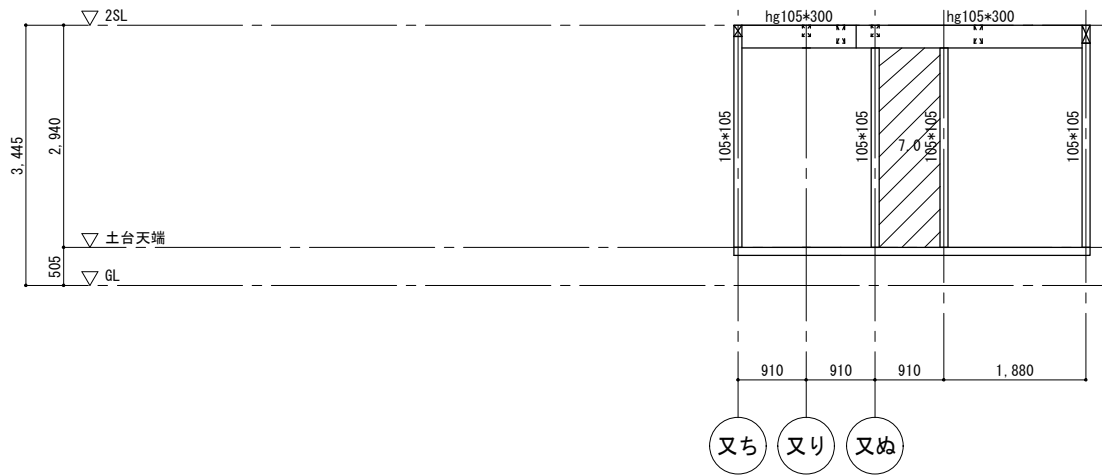

6' 通軸組図 1/100

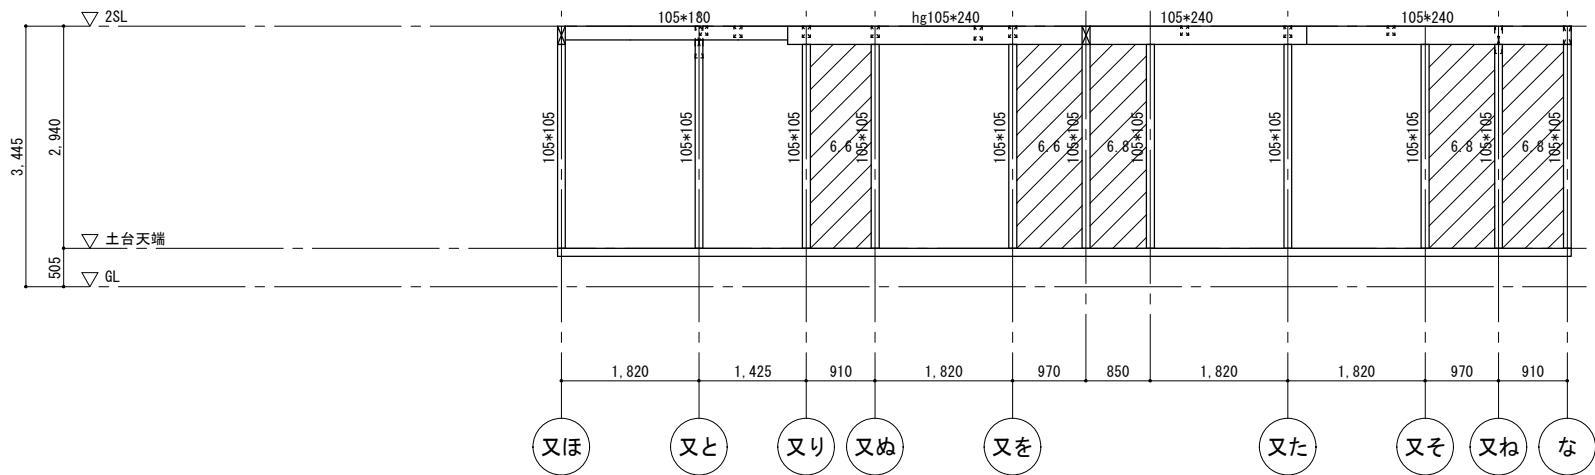

9' 通軸組図 1/100

特記無き場合は下記による。

土台:105*105

は壁倍率を示す。

株式会社 Rbe architects 二級建築士事務所
二級 東京都知事登録 第 16330 号
二級 建築士登録 第 83516 号
渡 辺 隆 一

森田厚史邸新築工事


軸組図10

1/100


S-22

藤田摂建築設計事務所

OSAMU FUJITA ARCHITECT+ASSOCIATES
一級建築士事務所 第2520号 / 一級建築士 第300013号 藤 田 摂


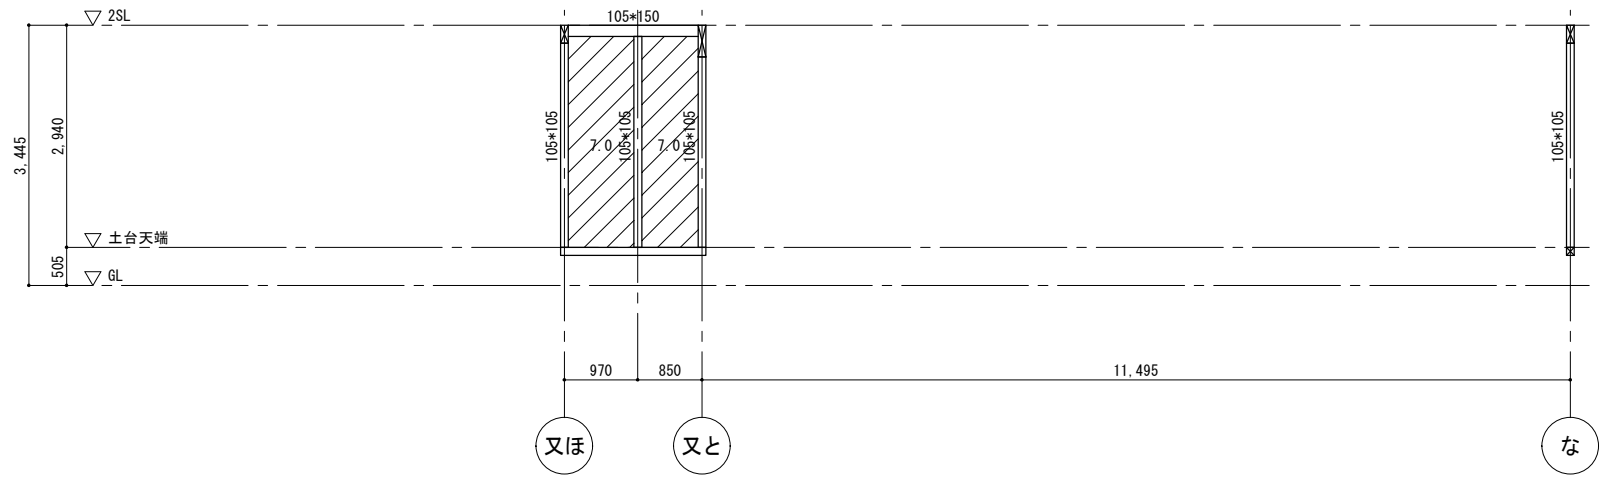


10' 通軸組図 1/100

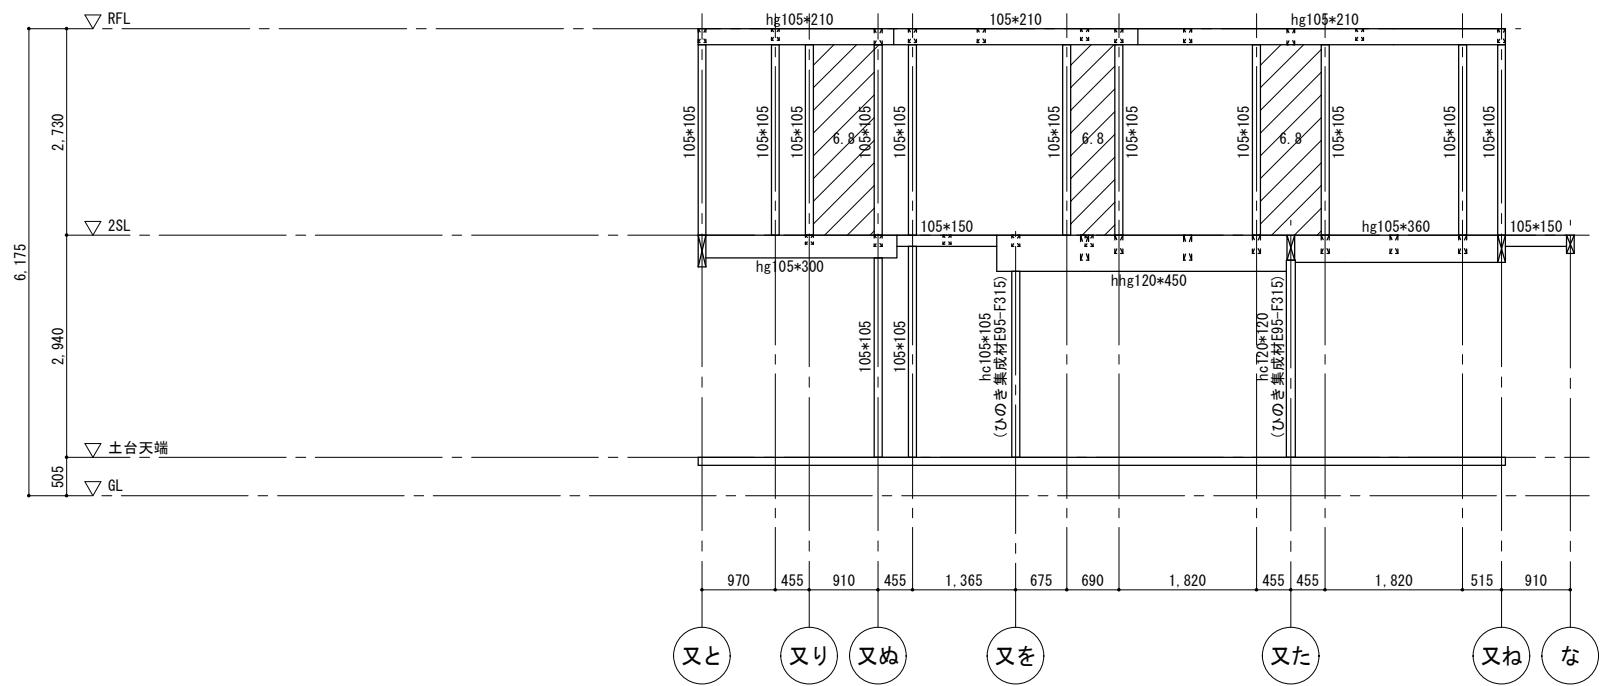


10'' 通軸組図 1/100


特記無き場合は下記による。
土台:105*105
/// () は壁倍率を示す。

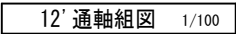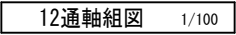

 () は壁倍率を示す。

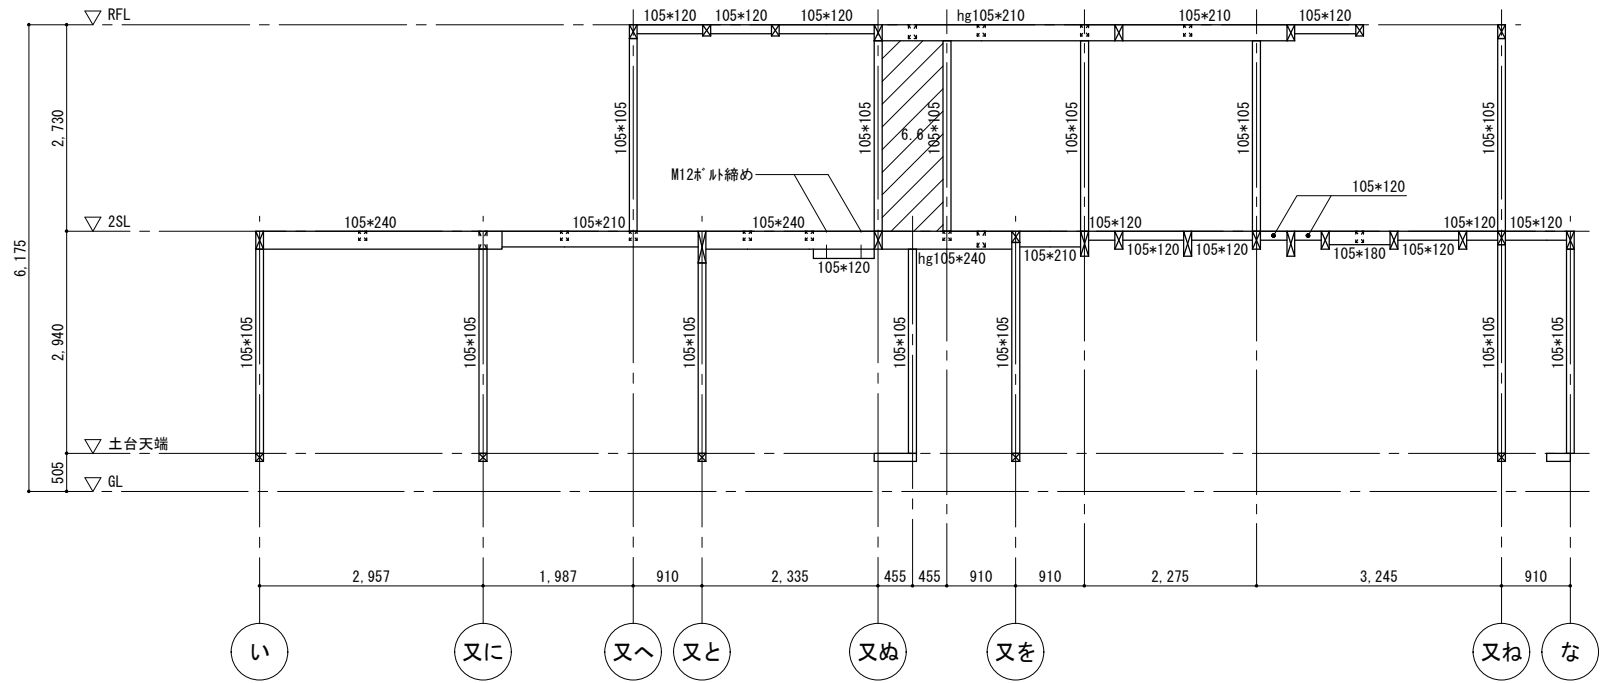


14通軸組図 1/100

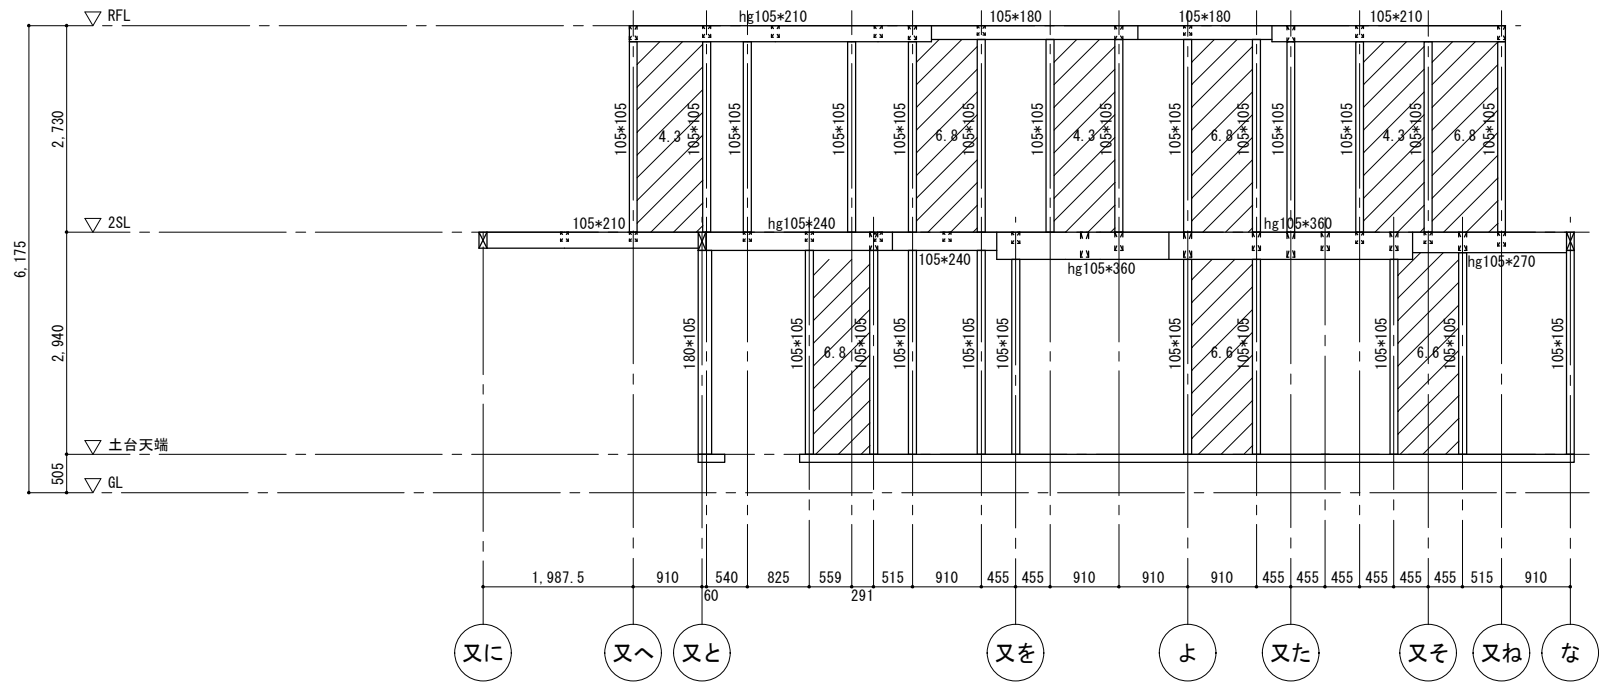


15'通軸組図 1/100

特記無き場合は下記による。
土台:105*105
(/)は壁倍率を示す。

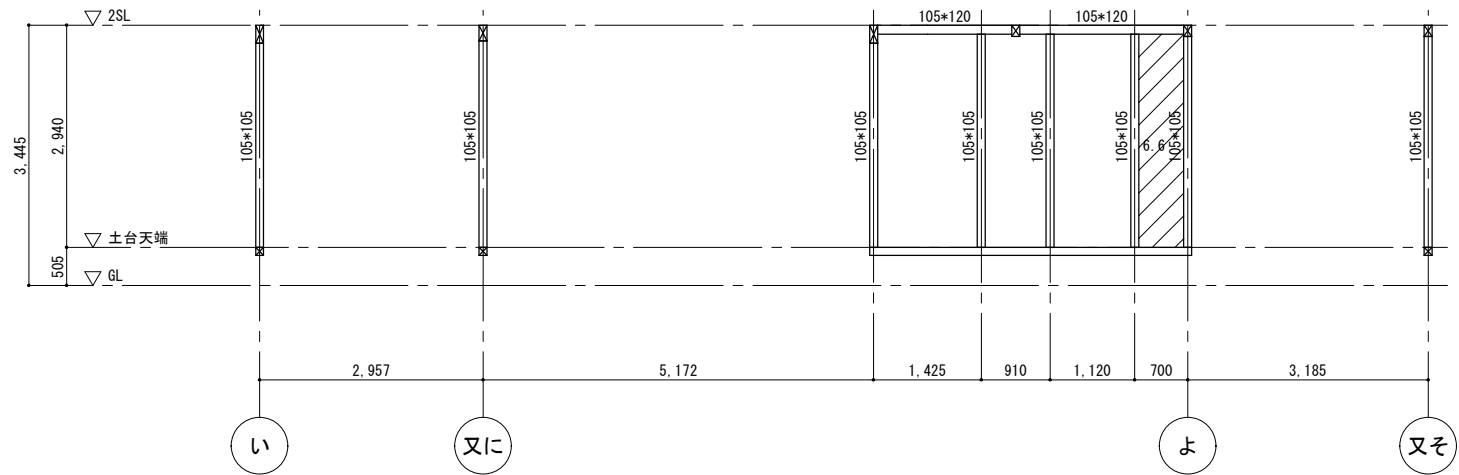

16通軸組図 1/100

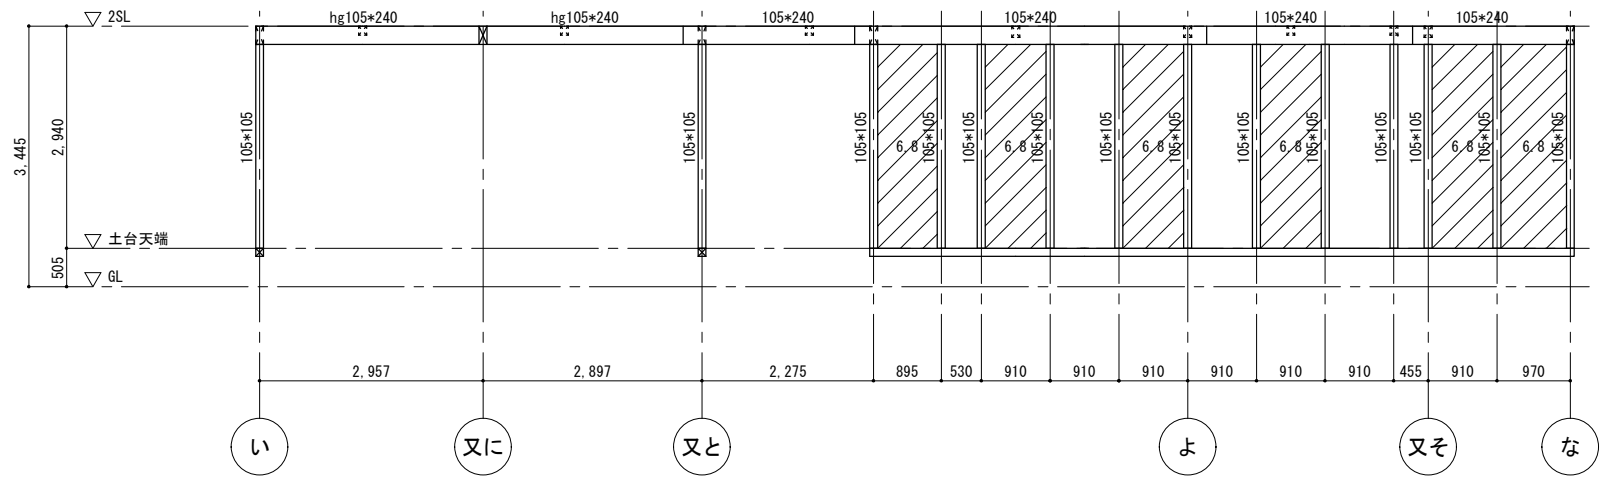



17通軸組図 1/100

特記無き場合は下記による。

土台:105*105

は壁倍率を示す。

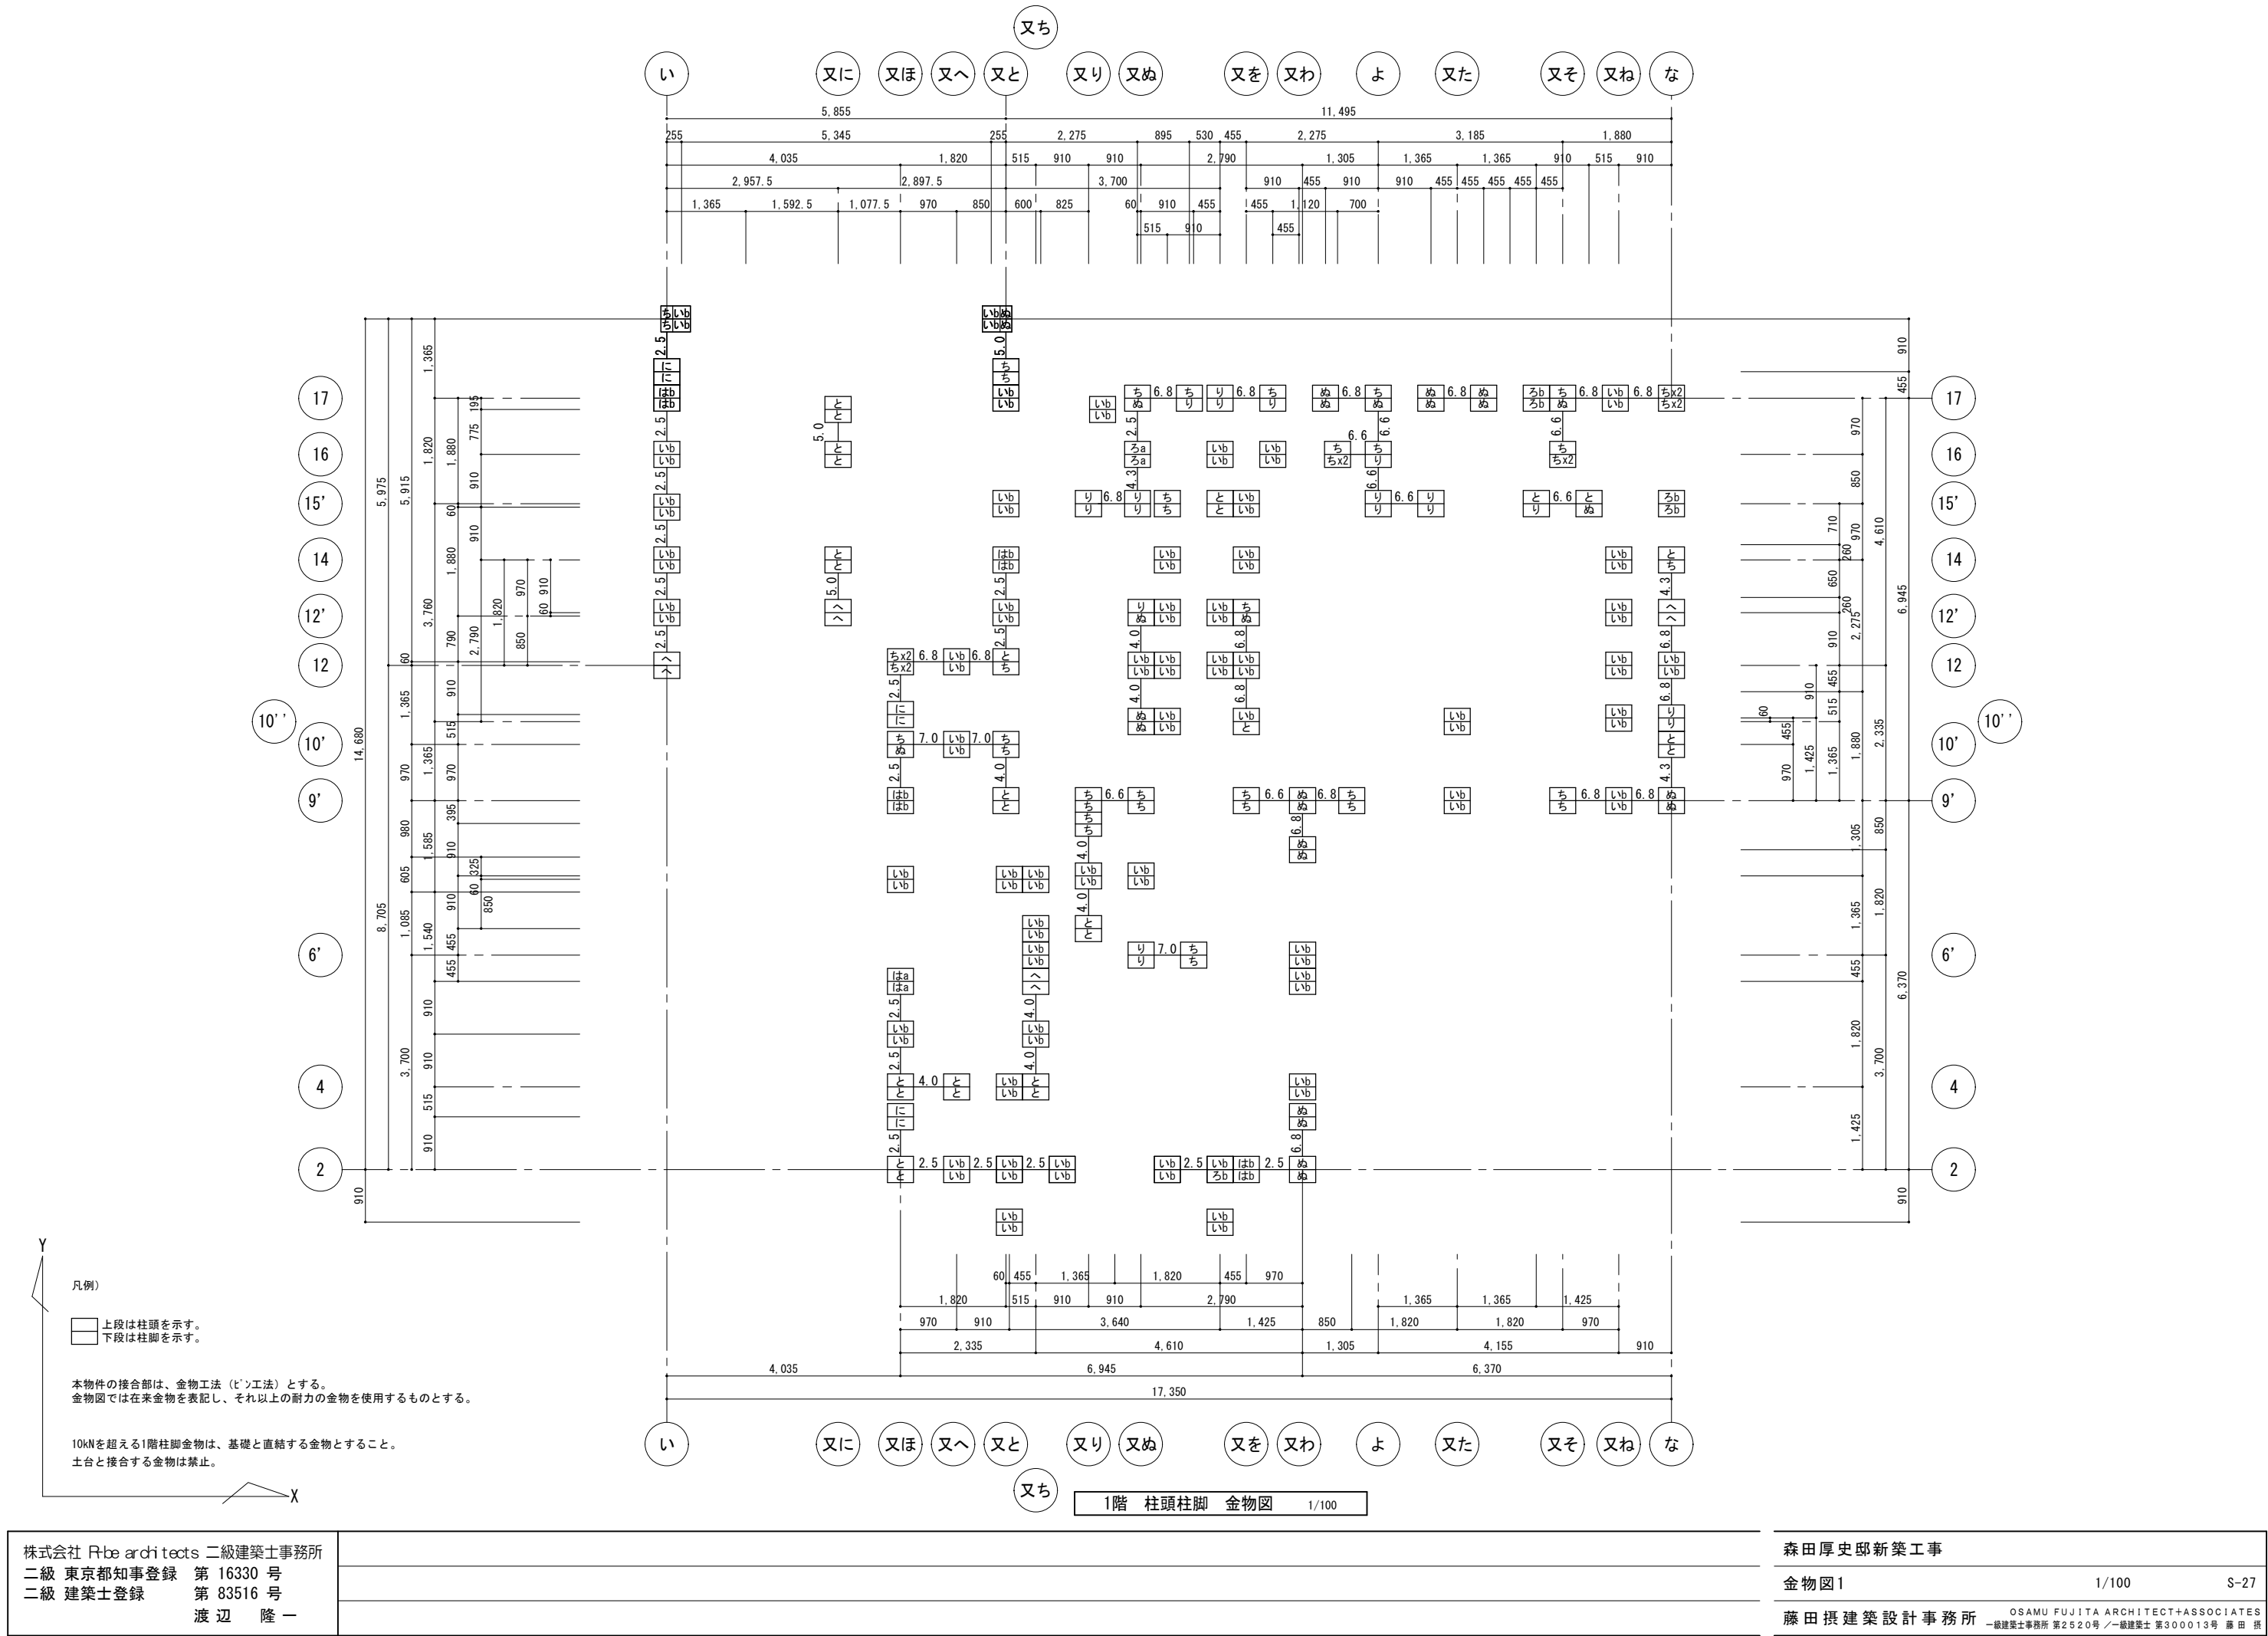

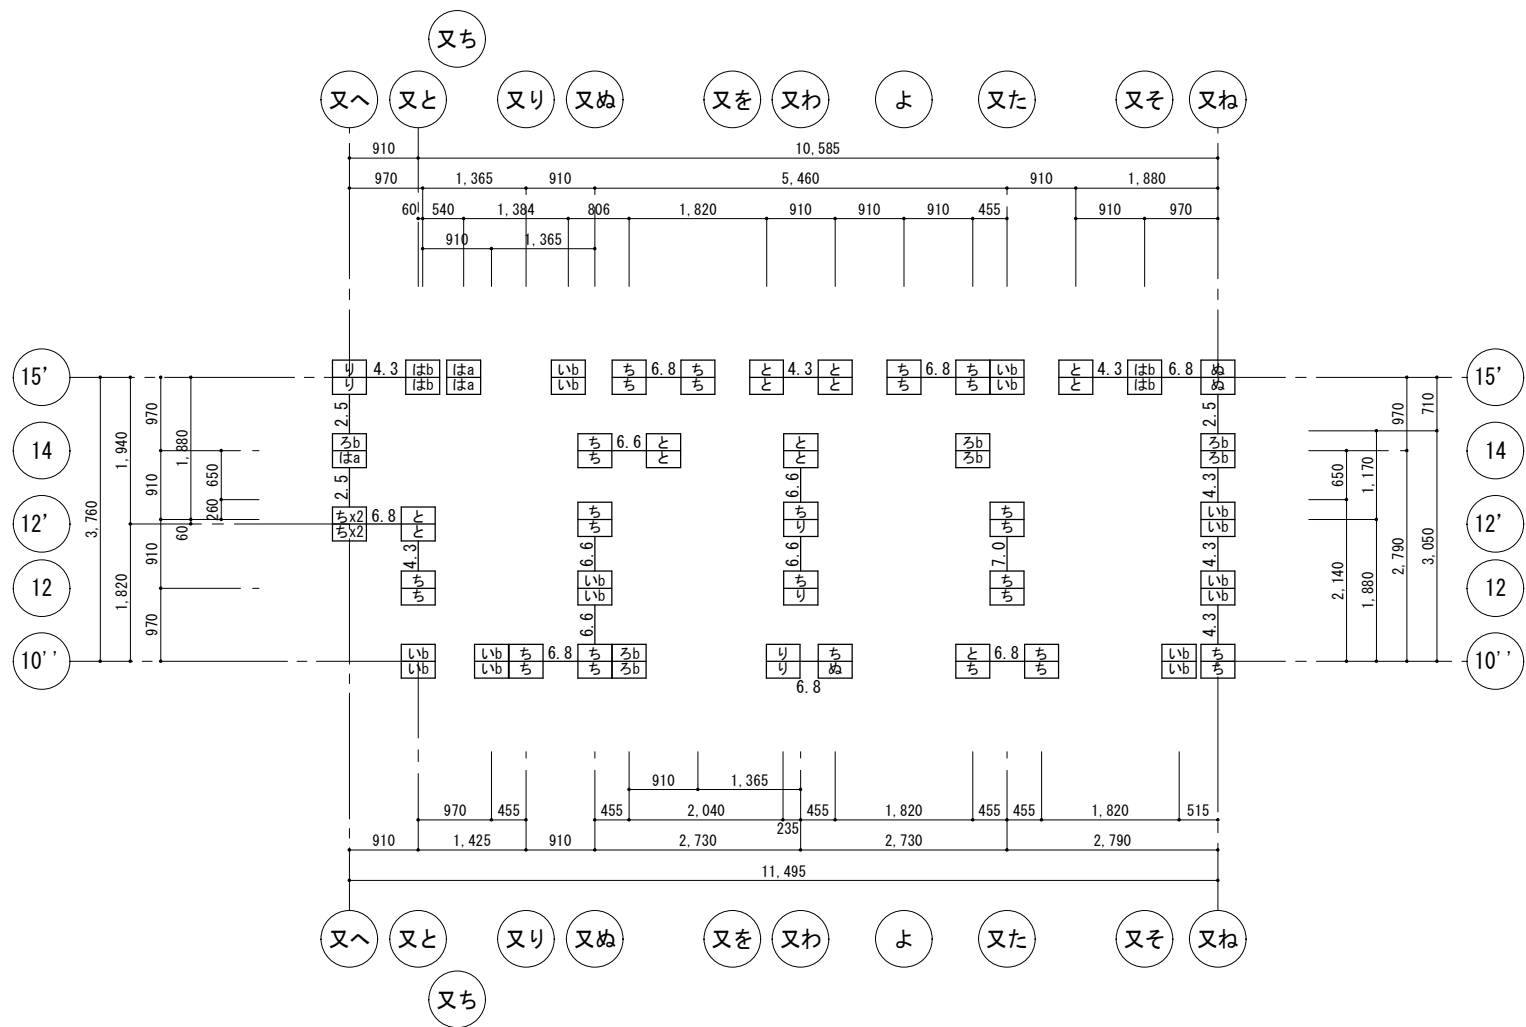

2階 柱頭柱脚 金物図 1/100

Y
凡例)



上段は柱頭を示す。

下段は柱脚を示す。



本物件の接合部は、金物工法（ビル工法）とする。
金物図では在来金物を表記し、それ以上の耐力の金物を使用するものとする。

X

株式会社 Rbe architects 二級建築士事務所 二級 東京都知事登録 第 16330 号 二級 建築士登録 第 83516 号 渡 辺 隆 一	森田厚史邸新築工事		
	金物図2	1/100	S-28
	藤田摂建築設計事務所 OSAMU FUJITA ARCHITECT+ASSOCIATES 一級建築士事務所 第2520号 / 一級建築士 第300013号 藤 田 摂		

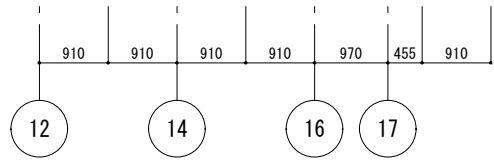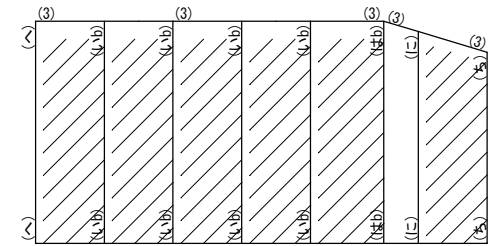



い通軸組図 1/100

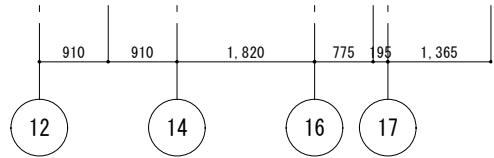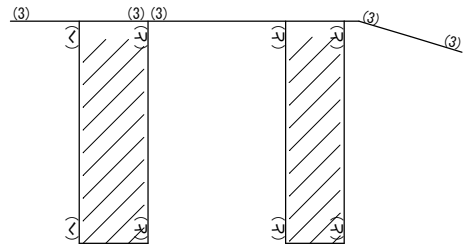



又に通軸組図 1/100

特記無き場合は下記による。
筋交45*90:Zマ-7筋交い金物2.0倍用とする。



株式会社 Rbe architects 二級建築士事務所 二級 東京都知事登録 第 16330 号 二級 建築士登録 第 83516 号 渡 辺 隆 一	森田厚史邸新築工事		
	金物図3	1/100	S-29
	藤田摂建築設計事務所 OSAMU FUJITA ARCHITECT+ASSOCIATES 一級建築士事務所 第2520号 / 一級建築士 第300013号 藤 田 摂		

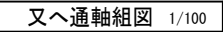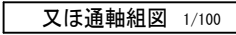

特記無き場合は下記による。
筋交45*90:Zマーク筋交い金物2.0倍用とする。

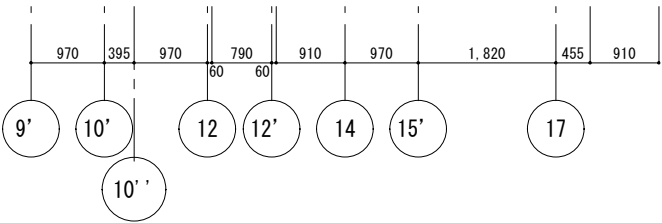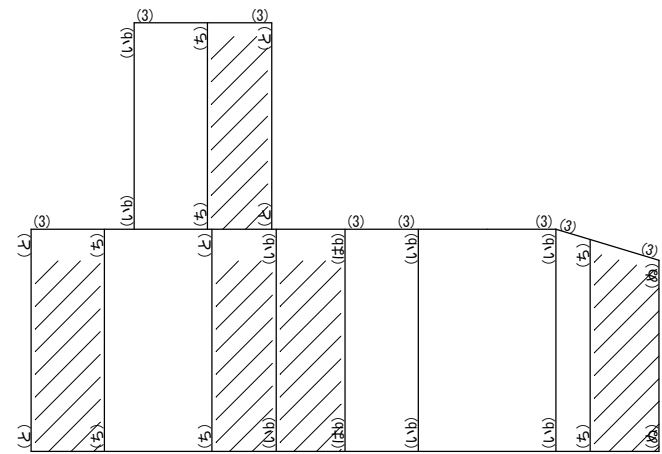


又と通軸組図 1/100

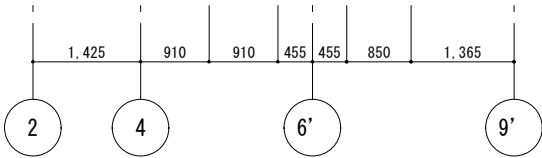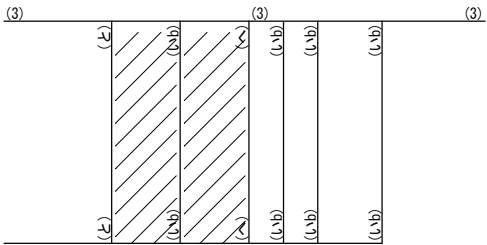


又ち通軸組図 1/100

特記無き場合は下記による。
筋交45*90:Zマ-7筋交い金物2.0倍用とする。

株式会社 Rbe architects 二級建築士事務所 二級 東京都知事登録 第 16330 号 二級 建築士登録 第 83516 号 渡 辺 隆 一	森田厚史邸新築工事		
	金物図5	1/100	S-31
	藤田摂建築設計事務所 OSAMU FUJITA ARCHITECT+ASSOCIATES 一級建築士事務所 第2520号 / 一級建築士 第300013号 藤 田 摂		

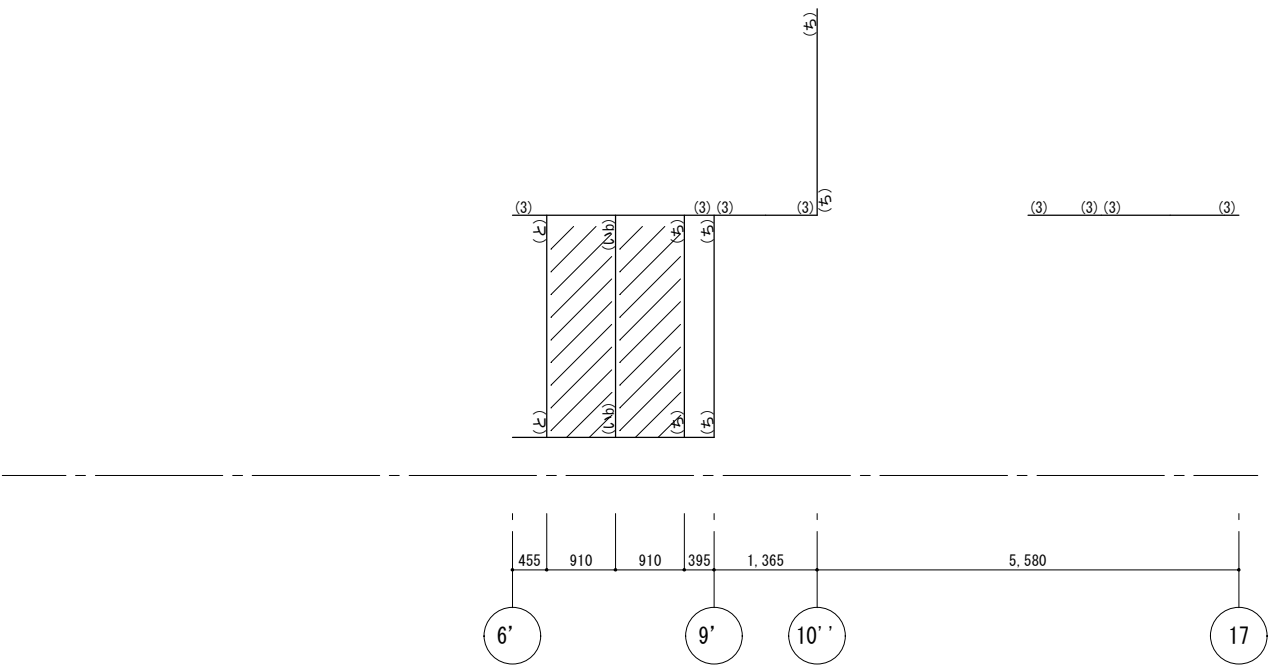


又り通軸組図 1/100

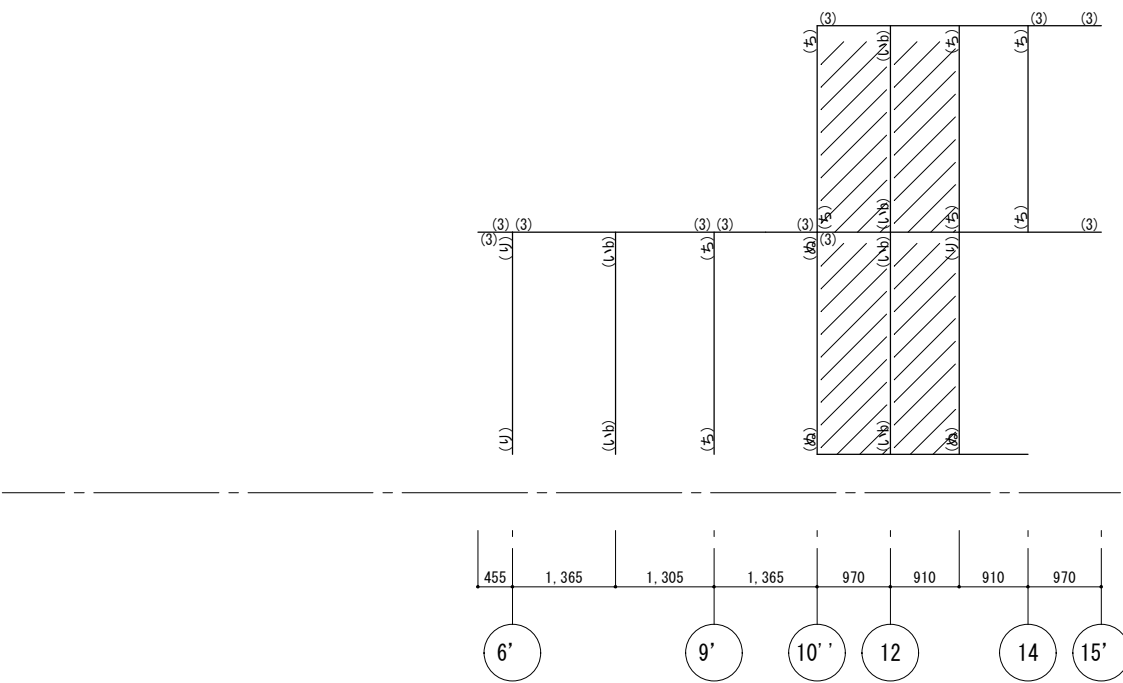


又ぬ通軸組図 1/100

特記無き場合は下記による。
筋交45*90:Zマ-7筋交い金物2.0倍用とする。

株式会社 Rbe architects 二級建築士事務所 二級 東京都知事登録 第 16330 号 二級 建築士登録 第 83516 号 渡 辺 隆 一	森田厚史邸新築工事		
	金物図6	1/100	S-32
	藤田摂建築設計事務所 OSAMU FUJITA ARCHITECT+ASSOCIATES 一級建築士事務所 第2520号 / 一級建築士 第300013号 藤 田 摂		

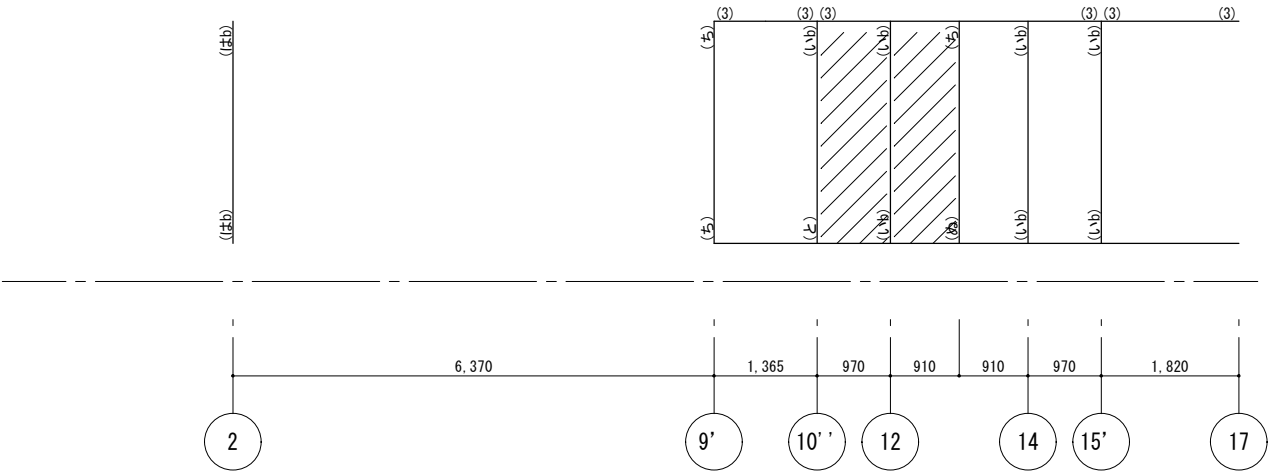



又を通軸組図 1/100

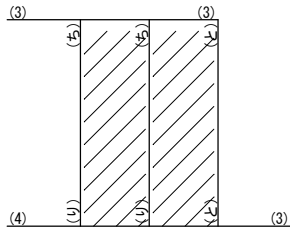



又わ通軸組図 1/100

特記無き場合は下記による。
筋交45*90:Zマ-7筋交い金物2.0倍用とする。

株式会社 Rbe architects 二級建築士事務所 二級 東京都知事登録 第 16330 号 二級 建築士登録 第 83516 号 渡 辺 隆 一	森田厚史邸新築工事		
	金物図7	1/100	S-33
	藤田摂建築設計事務所 OSAMU FUJITA ARCHITECT+ASSOCIATES 一級建築士事務所 第2520号 / 一級建築士 第300013号 藤 田 摂		

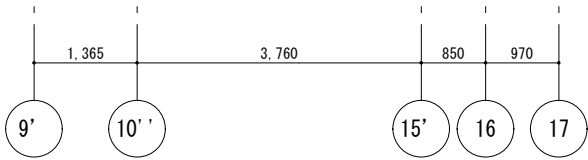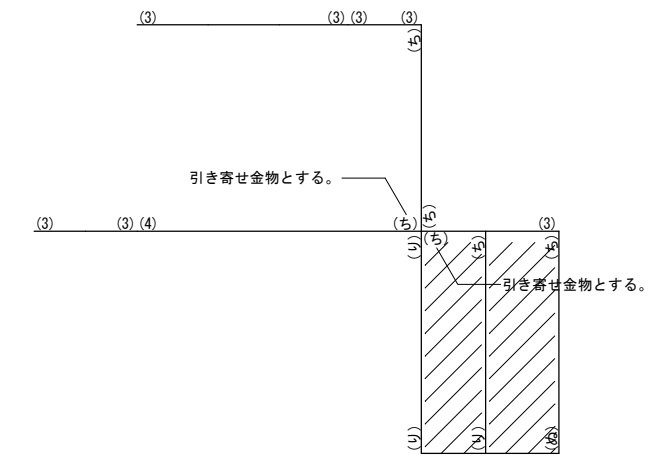


よ通軸組図 1/100

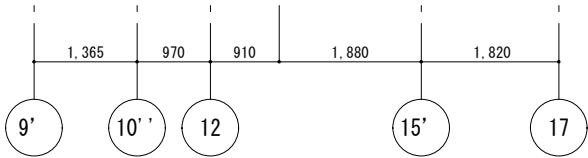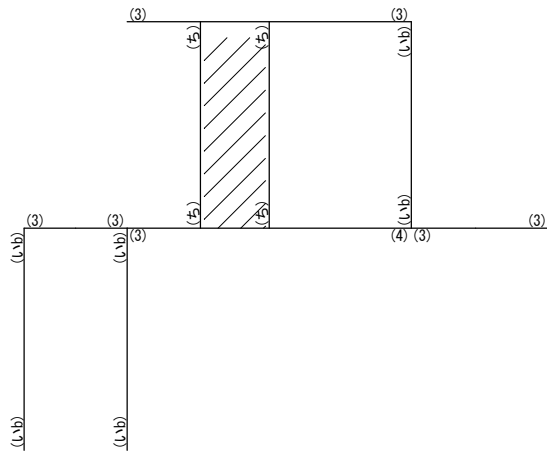


又た通軸組図 1/100

特記無き場合は下記による。
筋交45*90:Zマ-7筋交い金物2.0倍用とする。

株式会社 Rbe architects 二級建築士事務所 二級 東京都知事登録 第 16330 号 二級 建築士登録 第 83516 号 渡 辺 隆 一	森田厚史邸新築工事		
	金物図8	1/100	S-34
	藤田摂建築設計事務所 OSAMU FUJITA ARCHITECT+ASSOCIATES 一級建築士事務所 第2520号 / 一級建築士 第300013号 藤 田 摂		

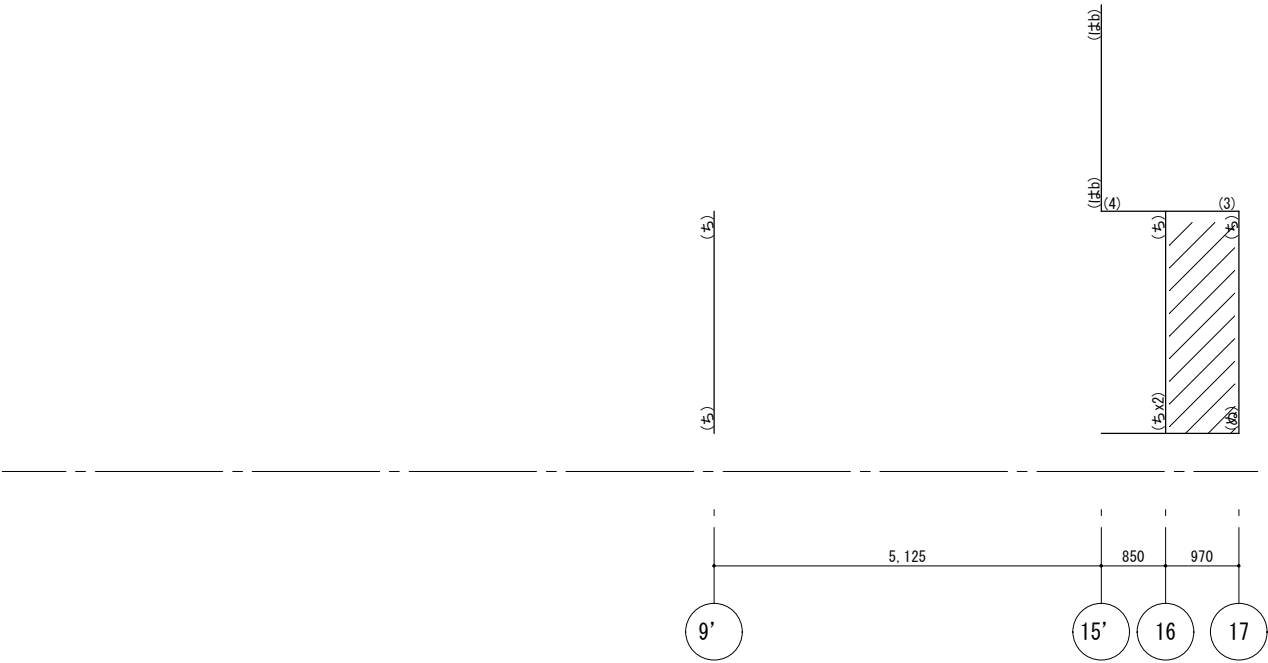


又そ通軸組図 1/100

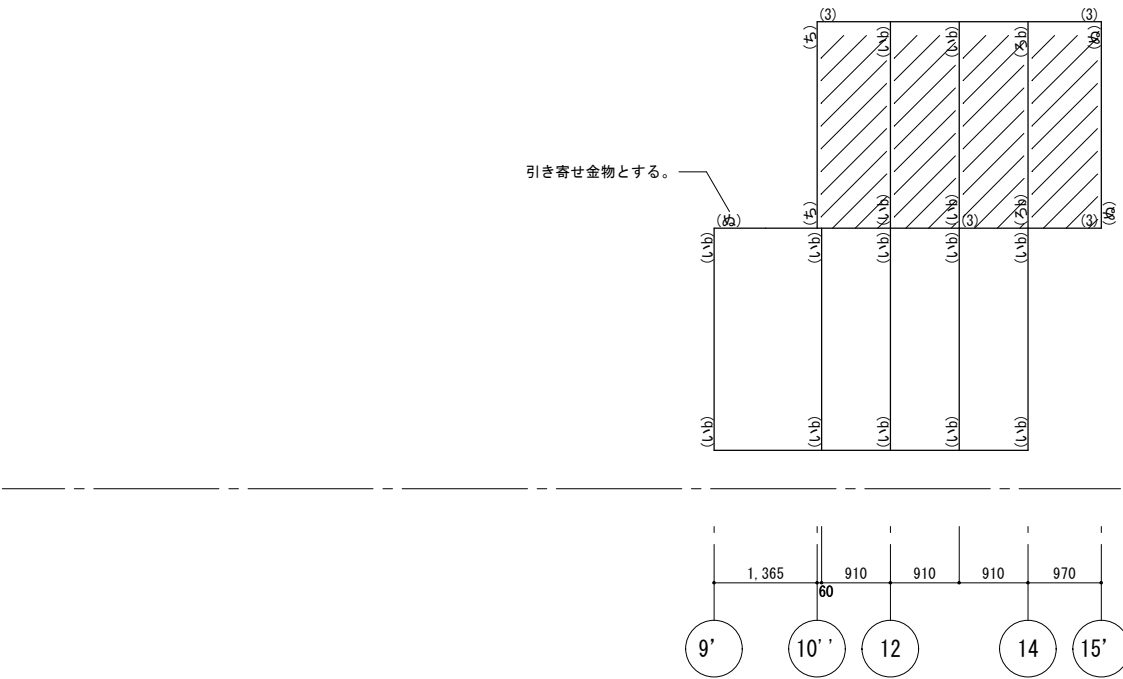

又ね通軸組図 1/100

特記無き場合は下記による。
筋交45*90:Zマ-7筋交い金物2.0倍用とする。


株式会社 Rbe architects 二級建築士事務所 二級 東京都知事登録 第 16330 号 二級 建築士登録 第 83516 号 渡 辺 隆 一	森田厚史邸新築工事		
	金物図9	1/100	S-35
	藤田 摂 建築設計事務所 OSAMU FUJITA ARCHITECT+ASSOCIATES 一級建築士事務所 第2520号 / 一級建築士 第300013号 藤 田 摂		

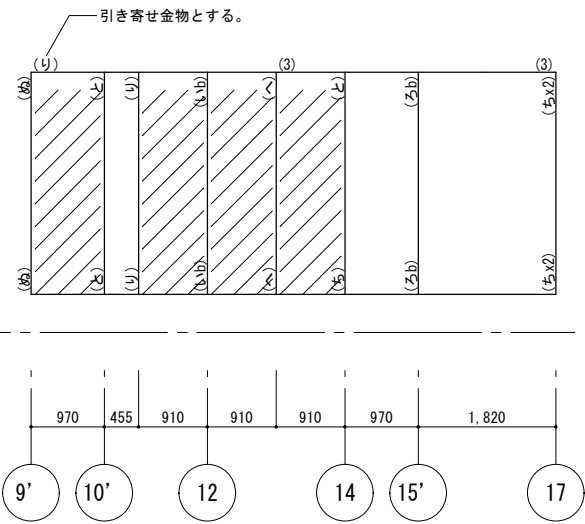


な通軸組図 1/100

特記無き場合は下記による。
筋交45*90:Zマ-7筋交い金物2.0倍用とする。

株式会社 Rbe architects 二級建築士事務所 二級 東京都知事登録 第 16330 号 二級 建築士登録 第 83516 号 渡 辺 隆 一	森田厚史邸新築工事		
	金物図10	1/100	S-36
	藤田摂建築設計事務所 OSAMU FUJITA ARCHITECT+ASSOCIATES 一級建築士事務所 第2520号 / 一級建築士 第300013号 藤 田 摂		

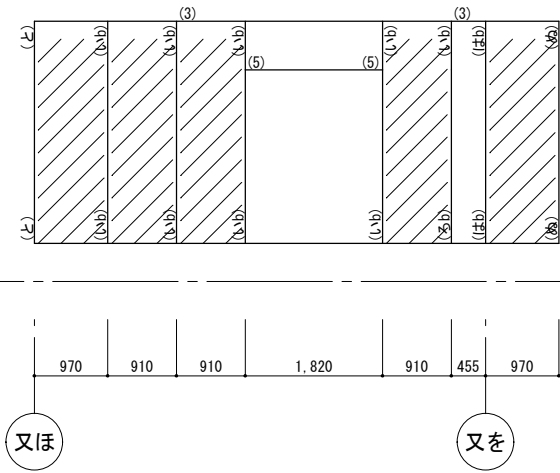



2通軸組図 1/100

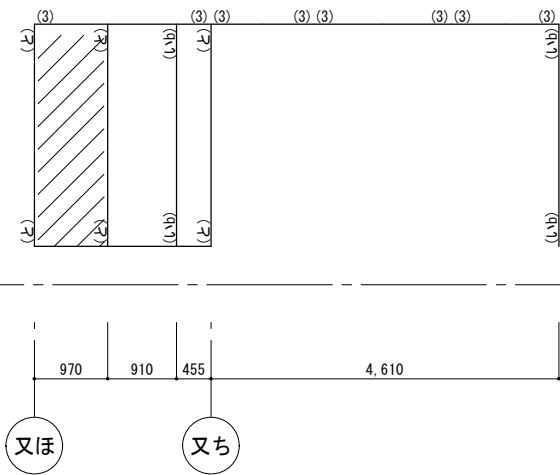



4通軸組図 1/100

特記無き場合は下記による。
筋交45*90:Zマ-7筋交い金物2.0倍用とする。

株式会社 Rbe architects 二級建築士事務所 二級 東京都知事登録 第 16330 号 二級 建築士登録 第 83516 号 渡 辺 隆 一	森田厚史邸新築工事		
	金物図11	1/100	S-37
	藤田 摂 建築設計事務所 OSAMU FUJITA ARCHITECT+ASSOCIATES 一級建築士事務所 第2520号 / 一級建築士 第300013号 藤 田 摂		

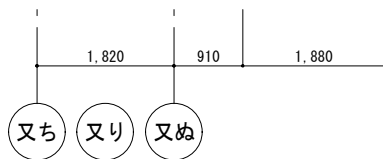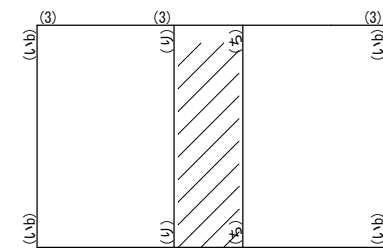



6' 通軸組図 1/100

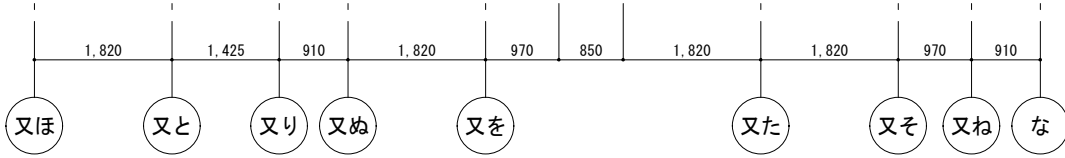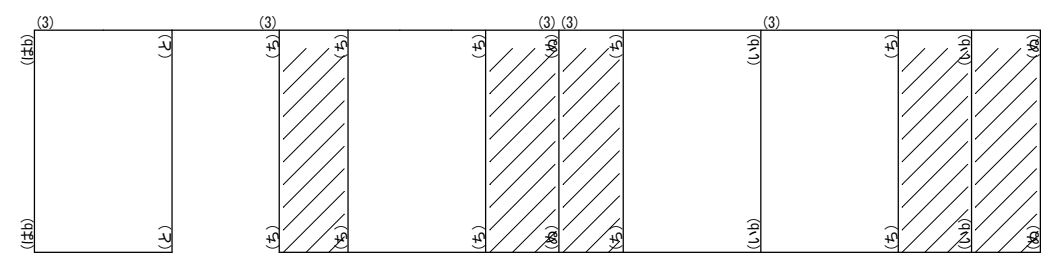

9' 通軸組図 1/100




特記無き場合は下記による。
筋交45*90:Zマ-7筋交い金物2.0倍用とする。

株式会社 Rbe architects 二級建築士事務所 二級 東京都知事登録 第 16330 号 二級 建築士登録 第 83516 号 渡 辺 隆 一	森田厚史邸新築工事		
	金物図12	1/100	S-38
	藤田摂建築設計事務所 OSAMU FUJITA ARCHITECT+ASSOCIATES 一級建築士事務所 第2520号 / 一級建築士 第300013号 藤 田 摂		

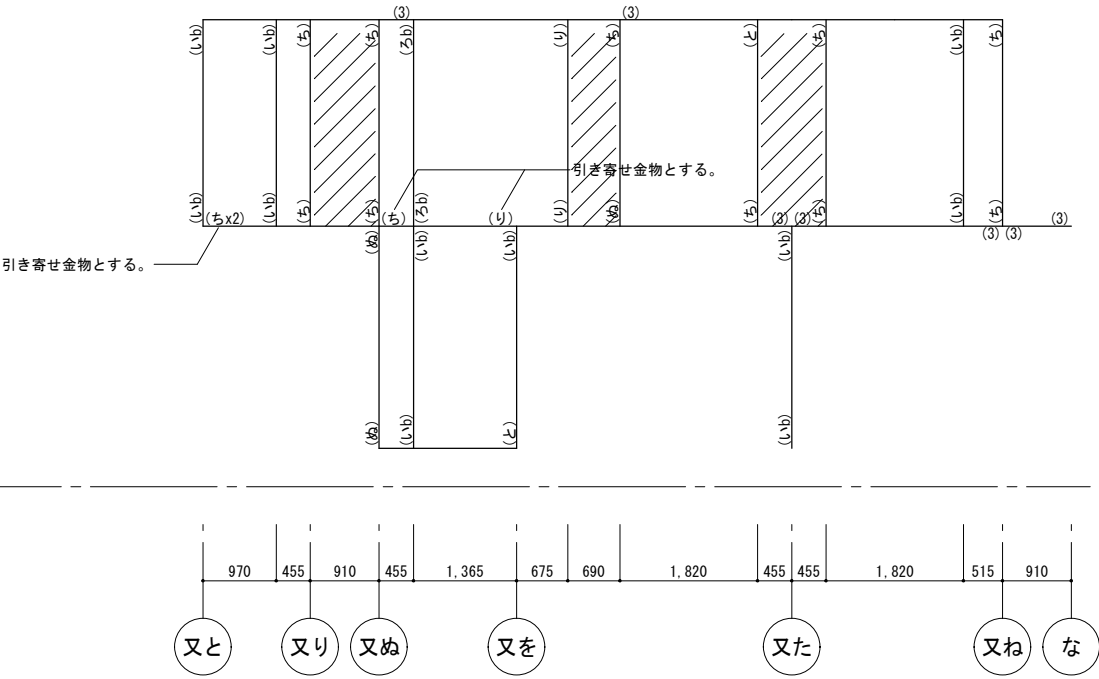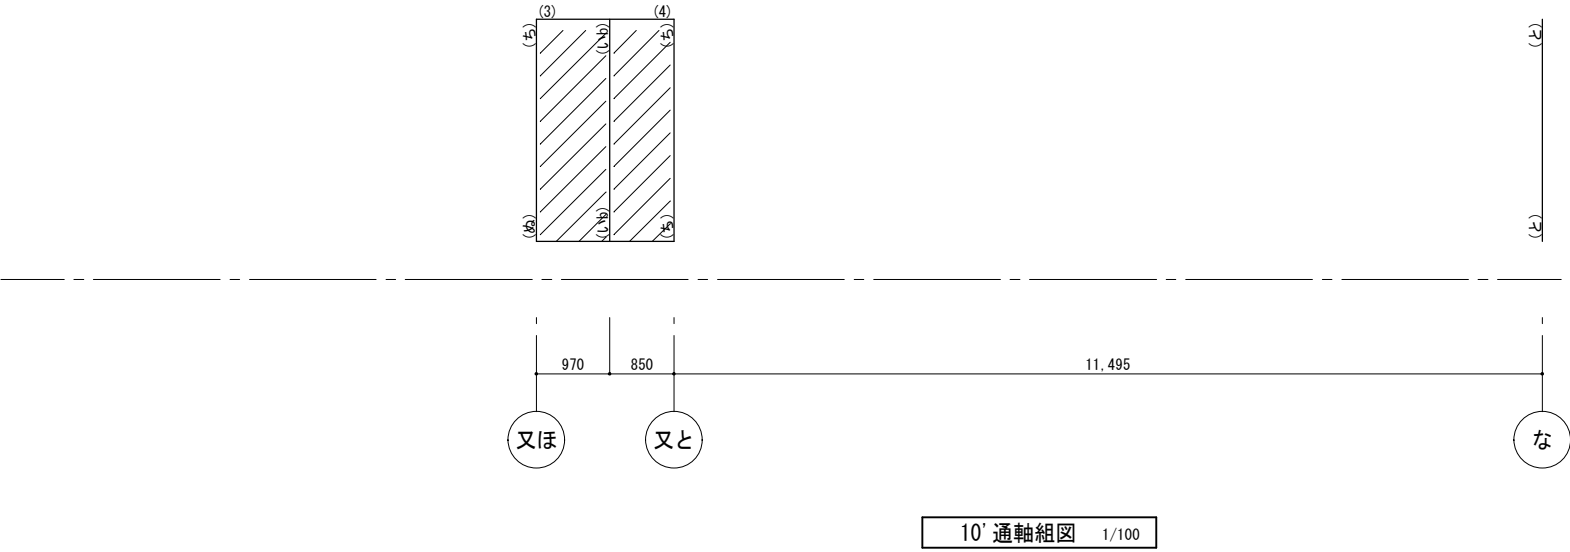



特記無き場合は下記による。
筋交45*90:Zマ-7筋交い金物2.0倍用とする。

株式会社 Rbe architects 二級建築士事務所 二級 東京都知事登録 第 16330 号 二級 建築士登録 第 83516 号 渡 辺 隆 一	森田厚史邸新築工事	
	金物図13	1/100 S-39
	藤田摂建築設計事務所 OSAMU FUJITA ARCHITECT+ASSOCIATES 一級建築士事務所 第2520号 / 一級建築士 第300013号 藤 田 摂	

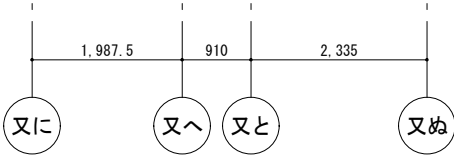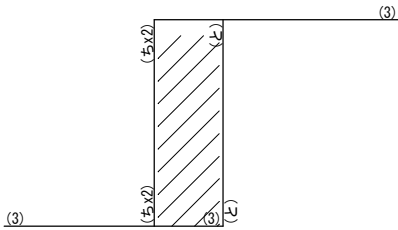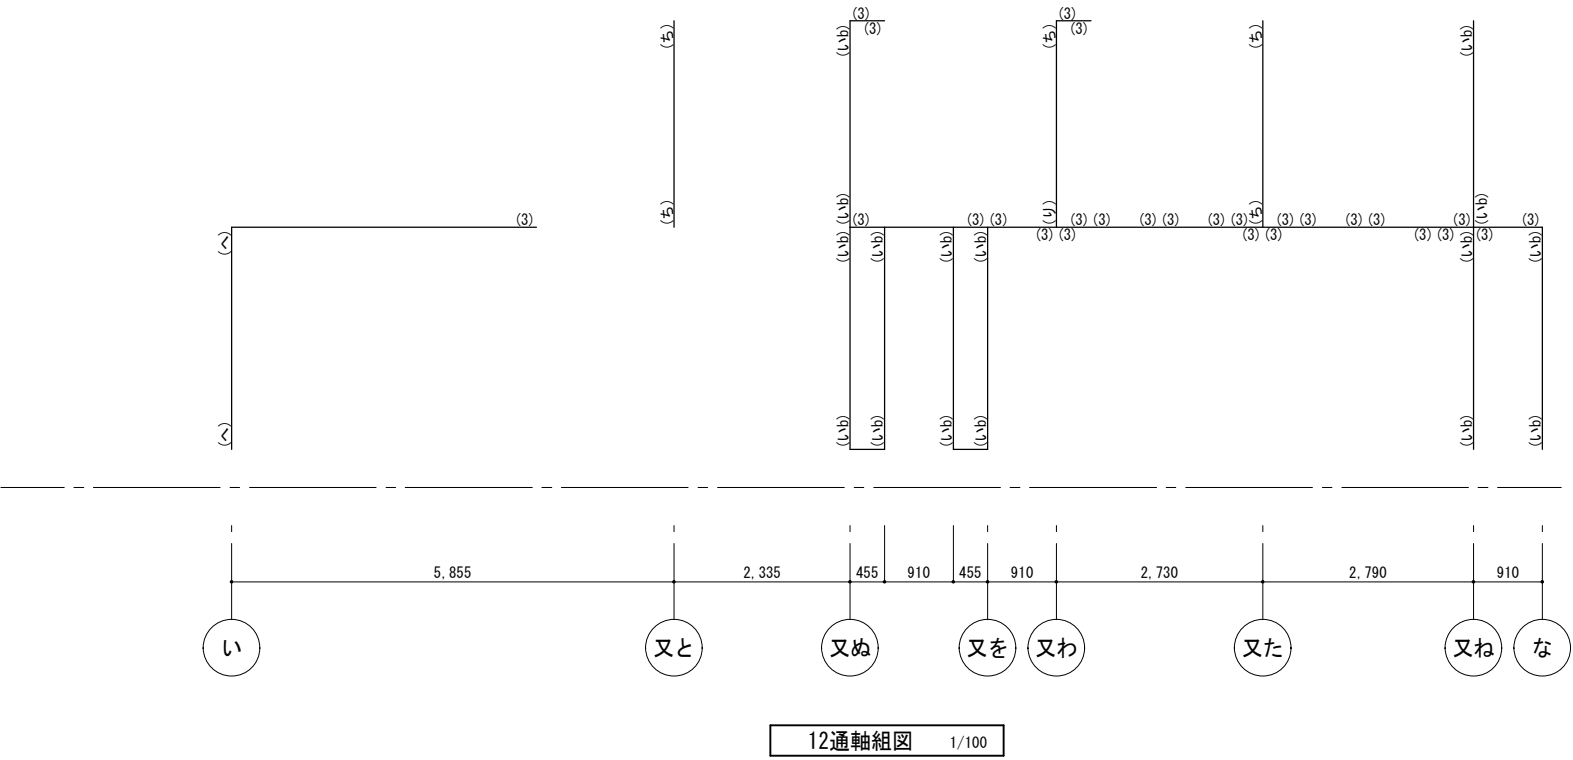


特記無き場合は下記による。
筋交45*90:Zマ-7筋交い金物2.0倍用とする。

株式会社 Rbe architects 二級建築士事務所 二級 東京都知事登録 第 16330 号 二級 建築士登録 第 83516 号 渡 辺 隆 一	森田厚史邸新築工事		
	金物図14	1/100	S-40
	藤田摂建築設計事務所 OSAMU FUJITA ARCHITECT+ASSOCIATES 一級建築士事務所 第2520号 / 一級建築士 第300013号 藤 田 摂		

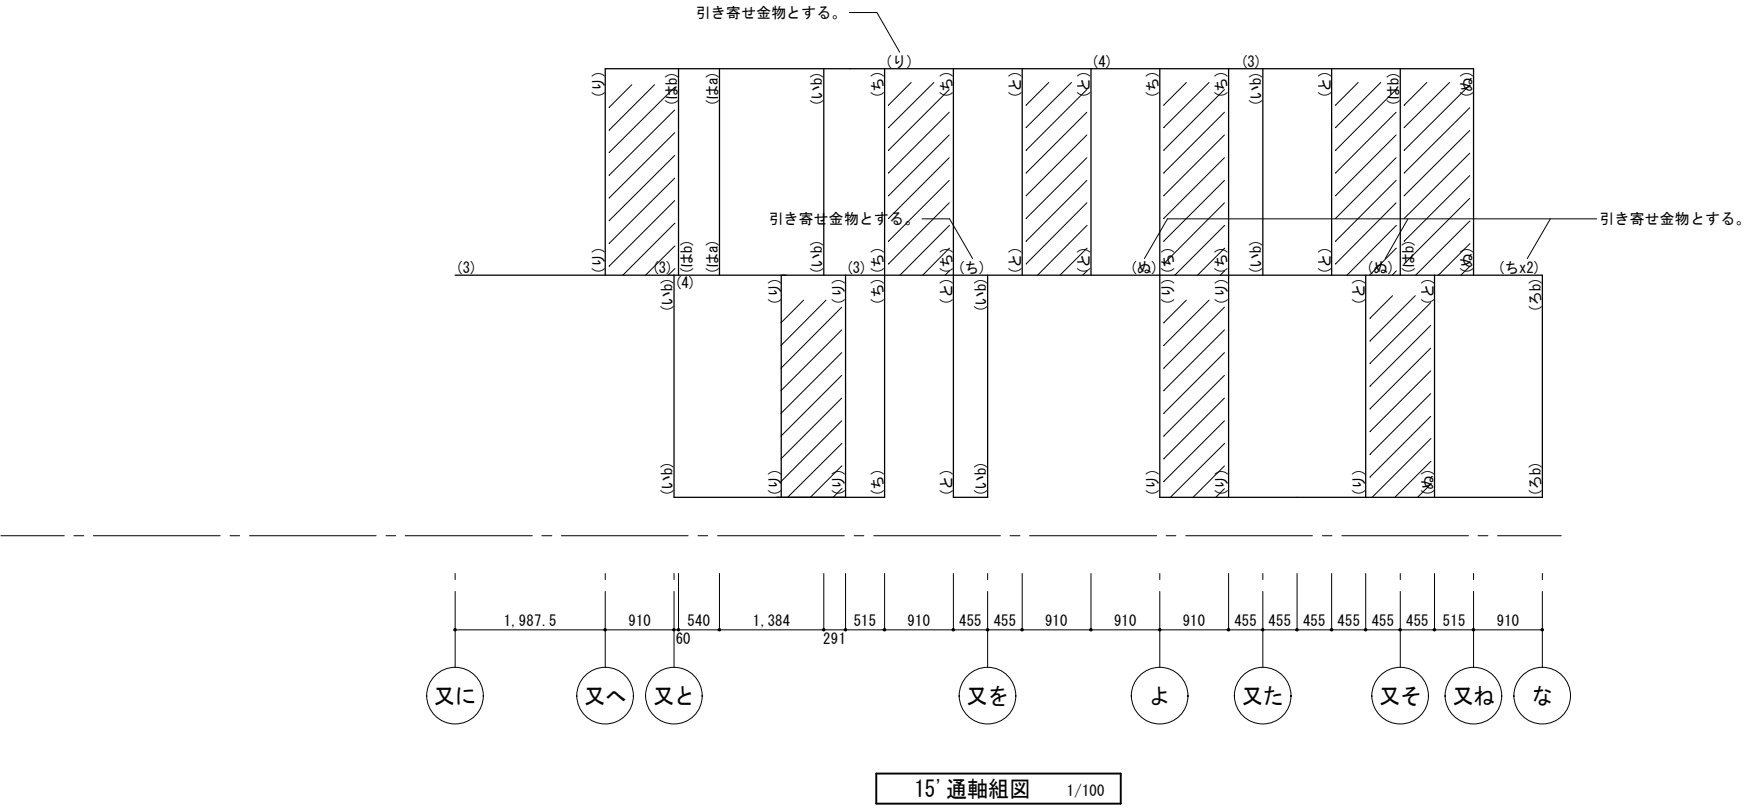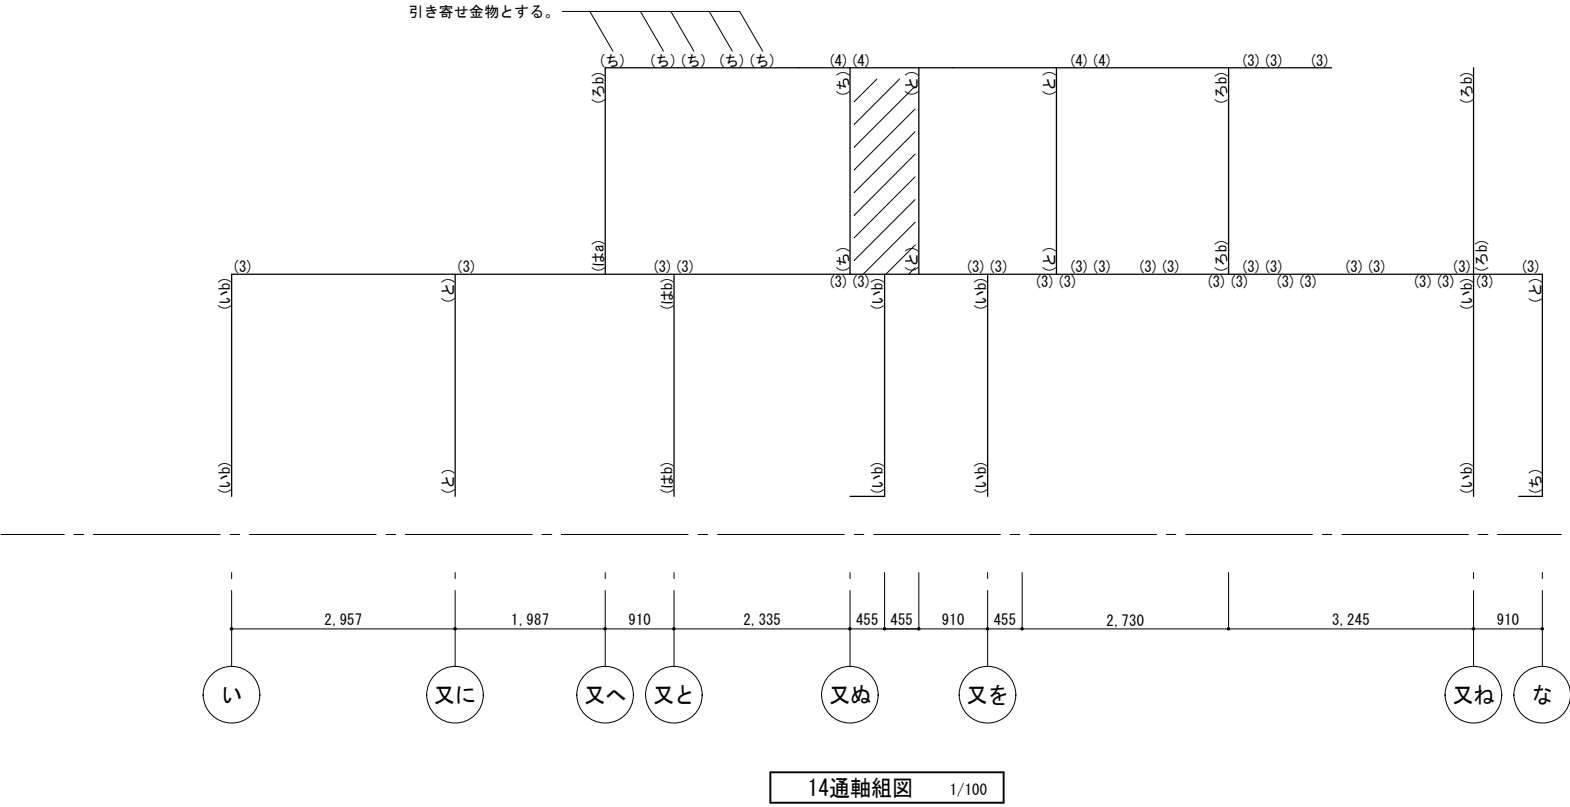


特記無き場合は下記による。
筋交45*90:Zマ-7筋交い金物2.0倍用とする。

株式会社 Rbe architects 二級建築士事務所 二級 東京都知事登録 第 16330 号 二級 建築士登録 第 83516 号 渡 辺 隆 一	森田厚史邸新築工事	
	金物図15	1/100 S-41
	藤田摂建築設計事務所 OSAMU FUJITA ARCHITECT+ASSOCIATES 一級建築士事務所 第2520号 / 一級建築士 第300013号 藤 田 摂	

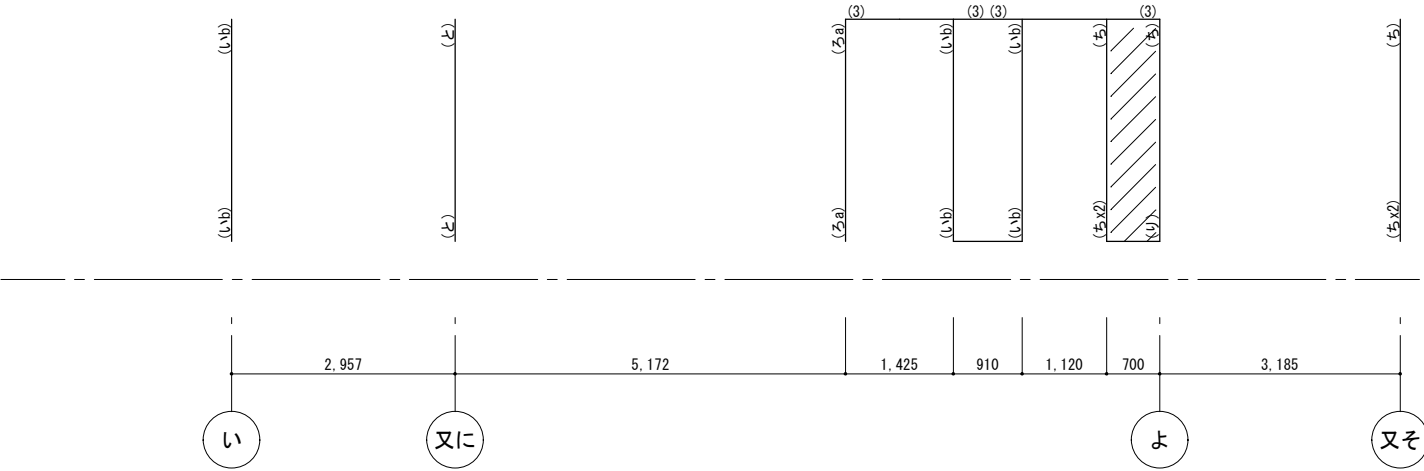


16通軸組図 1/100


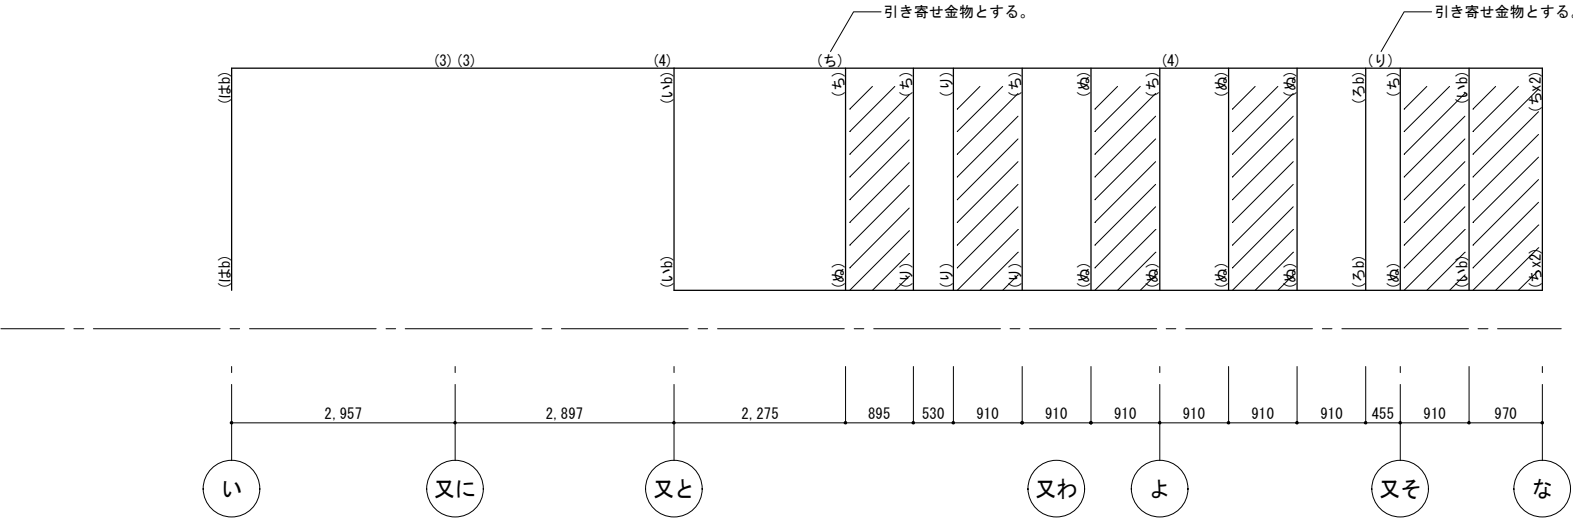


17通軸組図 1/100

特記無き場合は下記による。
筋交45*90:Zマ-7筋交い金物2.0倍用とする。

株式会社 Rbe architects 二級建築士事務所 二級 東京都知事登録 第 16330 号 二級 建築士登録 第 83516 号 渡 辺 隆 一	森田厚史邸新築工事	
	金物図16	1/100 S-42
	藤田摂建築設計事務所 OSAMU FUJITA ARCHITECT+ASSOCIATES 一級建築士事務所 第2520号 / 一級建築士 第300013号 藤 田 摂	

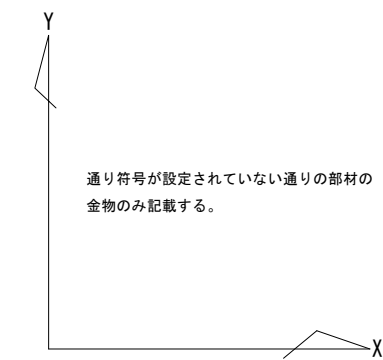

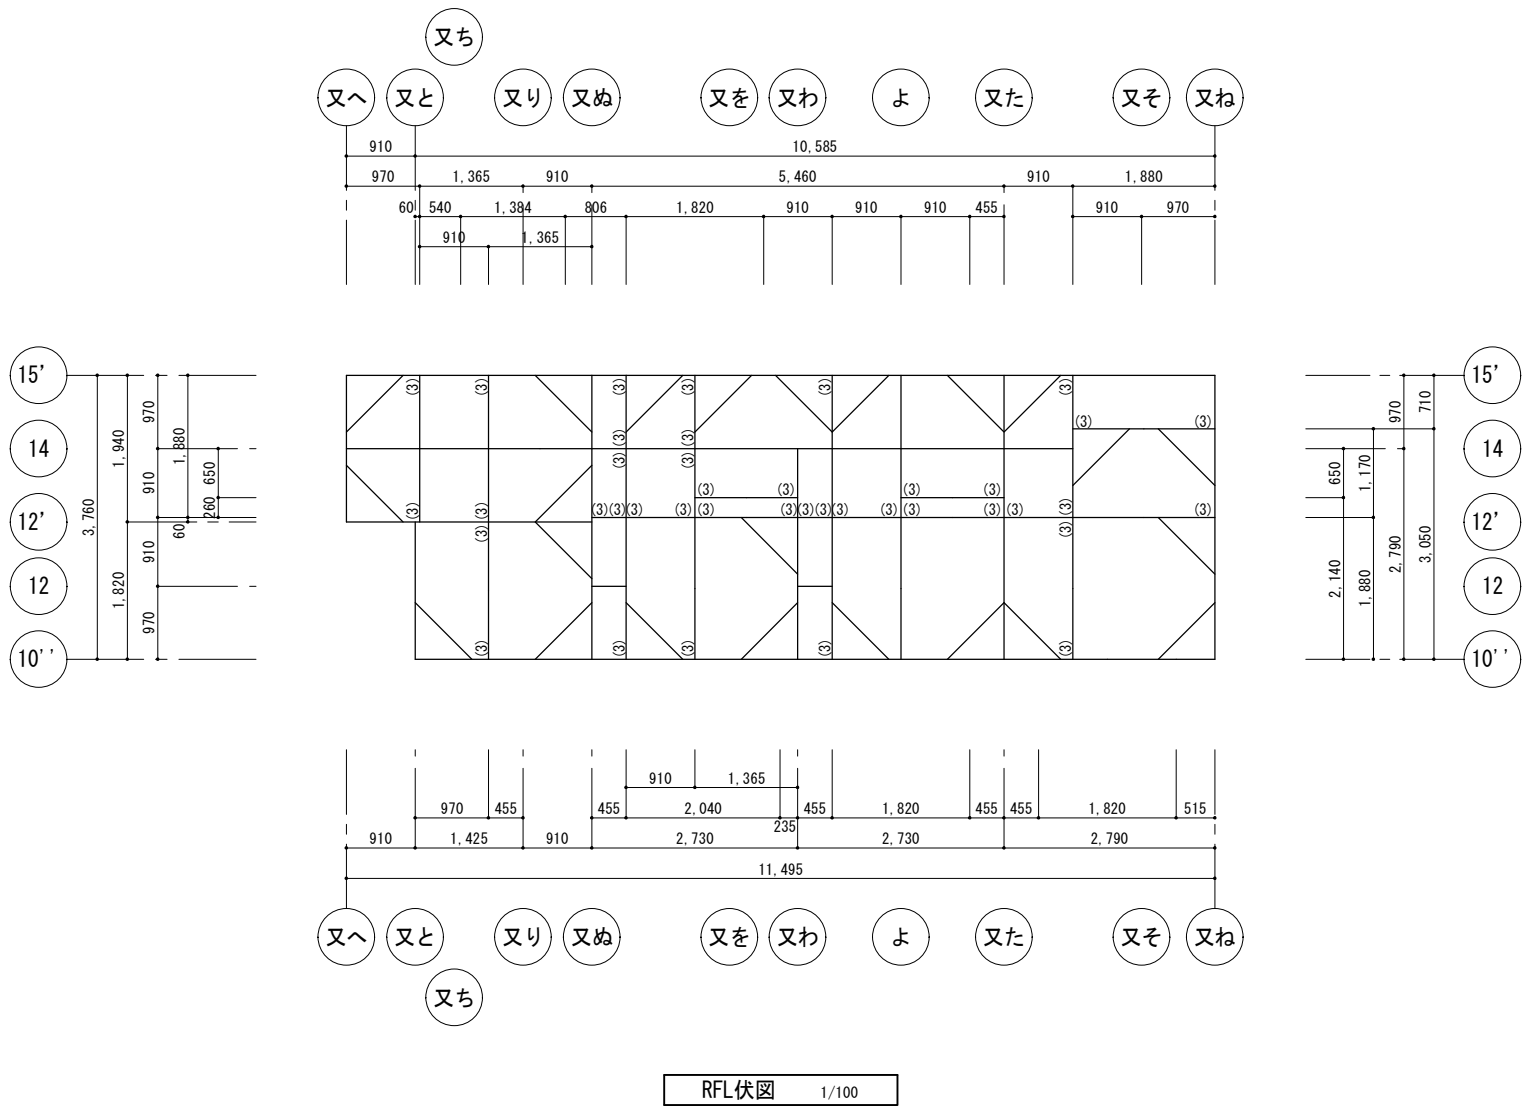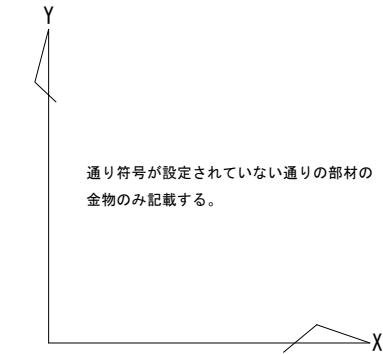

梁仕口の断面欠損率は0.5以下とする。



梁幅105mmのプレカットによる大入れ蟻掛け、及び、短ぼぞ差しを設けた
場合の断面係数、及び全断面に対する低減率
プレカット加工2社の寸法をもとにした参考値)

仕口 梁せい	全断面	A	A+A	B	B+B	A+B	C	A+C	A+A+C	B+C	B+B+C	A+B+C
105	 1.00 105 192.9	 0.86 165.4	 0.71 137.8	 0.74 142.9	 0.45 86.0	 0.60 114.8	 0.81 155.5	 0.66 127.8	 0.52 100.1	 0.53 102.1	 0.21 40.5	 0.38 73.2
120	 1.00 120 252.0	 0.88 222.2	 0.76 191.8	 0.74 186.3	 0.44 119.8	 0.61 153.7	 0.82 206.3	 0.70 175.3	 0.57 143.4	 0.54 136.5	 0.22 56.3	 0.40 101.9
150	 1.00 150 393.8	 0.89 350.9	 0.78 305.7	 0.74 291.0	 0.44 172.2	 0.61 241.8	 0.84 331.0	 0.73 286.0	 0.60 238.1	 0.58 227.8	 0.25 97.3	 0.43 170.8
180	 1.00 180 567.0	 0.89 504.9	 0.77 439.2	 0.75 425.7	 0.46 262.1	 0.63 354.7	 0.86 486.9	 0.74 422.3	 0.62 353.7	 0.60 339.5	 0.29 166.7	 0.47 265.9
210	 1.00 210 771.8	 0.89 686.0	 0.77 597.0	 0.75 578.6	 0.46 356.8	 0.63 482.4	 0.87 674.1	 0.76 585.9	 0.64 493.9	 0.62 475.1	 0.31 241.9	 0.48 373.9
240	 1.00 240 1008.0	 0.89 898.5	 0.78 784.2	 0.75 757.4	 0.46 466.4	 0.63 634.3	 0.89 892.8	 0.77 780.6	 0.66 663.6	 0.63 634.0	 0.33 330.8	 0.50 567.4
270	 1.00 270 1275.8	 0.89 1140.0	 0.78 999.3	 0.75 960.2	 0.48 613.7	 0.64 812.3	 0.90 1142.8	 0.79 1004.5	 0.68 861.2	 0.64 820.8	 0.37 466.0	 0.53 669.8
300	 1.00 300 1575.0	 0.90 1412.0	 0.79 1244.0	 0.76 1196.3	 0.50 781.8	 0.65 1020.1	 0.90 1424.3	 0.80 1258.8	 0.69 1088.4	 0.66 1038.7	 0.39 615.9	 0.55 859.7
330	 1.00 330 1905.8	 0.90 1714.7	 0.80 1518.9	 0.76 1440.6	 0.49 929.8	 0.65 1234.7	 0.91 1737.2	 0.81 1543.9	 0.71 1345.6	 0.66 1264.3	 0.39 744.0	 0.55 1055.7
360	 1.00 360 2268.0	 0.90 2047.4	 0.80 1824.1	 0.75 1708.0	 0.48 1091.5	 0.65 1471.9	 0.92 2081.6	 0.82 1859.9	 0.72 1633.2	 0.67 1513.0	 0.39 885.9	 0.56 1274.3
390	 1.00 390 2661.8	 0.91 2413.2	 0.81 2160.0	 0.75 1998.3	 0.48 1266.9	 0.65 1731.7	 0.92 2457.5	 0.83 2206.9	 0.73 1951.5	 0.67 1784.6	 0.39 1041.4	 0.57 1515.5
仕口の記号は、 A：根太・甲乙梁の大入れ 片側※1 B：大入れ蟻掛け 片側※2 C：短ぼぞ差し※3						凡例 0.74・・・断面係数の全断面に対する比（低減率） 142.9・・・断面係数（cm3）						
※1：根太・甲乙梁のせいは105mm、大入れの奥行きは15mmとする ※2：蟻掛けは、梁幅105mm、男木と女木の梁せいは同じとする ※3：短ぼぞの幅は30mm、深さは30mmとする												

金物凡例		
記号	金物仕様	短期許容引張耐力 (kN)
いa	短ぼぞ差し以上	0.0
いb	かすがい打ち以上	1.08
ろa	長ぼぞ差し込み栓打ち以上	3.81
ろb	L字型かど金物 くぎCN65*10本以上	3.38
はa	T字型かど金物 くぎCN65*10本以上	5.07
はb	山形プレート金物 くぎCN90*8本以上	5.88
に	羽子板ボルトφ12mm又は短ざく金物以上	7.50
ほ	羽子板ボルトφ12mm又は短ざく金物に長さ50mm径4.5mmスクリー ヌー釘*1本以上	8.50
へ	引き寄せ金物φ12mmのボルト*2本以上	10.0
と	引き寄せ金物φ12mmのボルト*3本以上	15.0
ち	引き寄せ金物φ12mmのボルト*4本以上	20.0
り	引き寄せ金物φ12mmのボルト*5本以上	25.0
ぬ	引き寄せ金物φ12mmのボルト*3本*2セット以上	30.0
(1)	腰掛け蟻（鎌） 継ぎ+厚さ3.2mmの短ざく金物で双方の横架材に対してそれぞれ 径12mmのボルト締めしたもの。又は、これと同等以上の接合方法としたもの。	10.1
(2)	腰掛け蟻（鎌） 継ぎ+厚さ3.2mmの短ざく金物2枚を用いて双方の横架材に対して それぞれ径12mmのボルト締めしたもの。又は、これと同等以上の接合方法としたもの。	15.9
(3)	大入れ蟻掛け+厚さ3.2mmの鋼板に径12mmのボルトを溶接した金物（羽子板ボルト）を 用いて、一方の部材に対して径12mmボルト締め、他方の部材に対して 厚さ4.5mm、40mm角の座金を介してナット締めしたもの。 又は、これと同等以上の接合方法としたもの。	10.1
(4)	大入れ蟻掛け+厚さ3.2mmの鋼板に径12mmのボルトを溶接した金物（羽子板ボルト） 2個を用いて、一方の部材に対して径12mmのボルト締め、 他方の部材に対して2個の金物それぞれについて厚さ4.5mm、40mm角の座金を 介してナット締めしたもの。又は、これと同等以上の接合方法としたもの。	15.9
(5)	横架材端部を通し柱に大入れ短ざく差し、又は、傾ぎ大入れとし、引張力は 羽子板ボルト又は短ざく金物、又は、かね折り金物（厚さ3.2mmの鋼板を L字型に折り曲げて出隅部の通し柱に取り付け直交方向の横架材端部どうし を径12mmのボルト締め）を用いて径12mmのボルト締めとしたもの。 又は、これと同等以上の接合方法としたもの。	7.5
(6)	横架材端部を通し柱に大入れ短ざく差し、又は、傾ぎ大入れとし、引張力は 羽子板ボルト又は短ざく金物を用いて径12mmのボルト締めに加えて長さ 50mm径4.5mmスクリー ヌー釘1本をそれぞれの横架材に打ち込んだもの。 又は、これと同等以上の接合方法としたもの。	8.5
備考 (へ)～(ぬ)の引き寄せ金物のアカーボルトはM16 (SS400) とする。		

梁継手詳細図1/20

梁の継手位置は柱芯から250mm以内の位置とする。

火打接合部詳細図1/30

HD金物詳細図（ち×2・り×2）1/30

※HD金物を柱の一面に取り付ける場合とする。
各メーカーの商品を使用する場合は除く。

A矢視詳細図

ち×2:40kN以上
樹脂製フルスーパウ40+高耐力フレックスアンカーボルト、同等品
鉄製ビス止めボルトウチ+オメガアンカーボルトM16、同等品
り×2:50kN以上
鉄製高耐力ボルトウチ+高耐力オメガアンカーボルトM16、同等品
樹脂製高耐力フレックスボルトウチ60+高耐力フレックスアンカーボルト、同等品