
天井点検口の候補位置（仮案）

1　　２階　ＷＩＣ：小屋裏点検用（収納棚を避けた通路上）


2　　１階　ホール：ＰＳ・収納手前の配管点検用（配管位置に合わせる）

3　　１階　脱衣室：ＵＢ側の設備点検用（ＵＢ付属点検口で届けば省略）

□は候補範囲。寸法・位置は梁、設備、脚立の設置スペースを確認して決定。

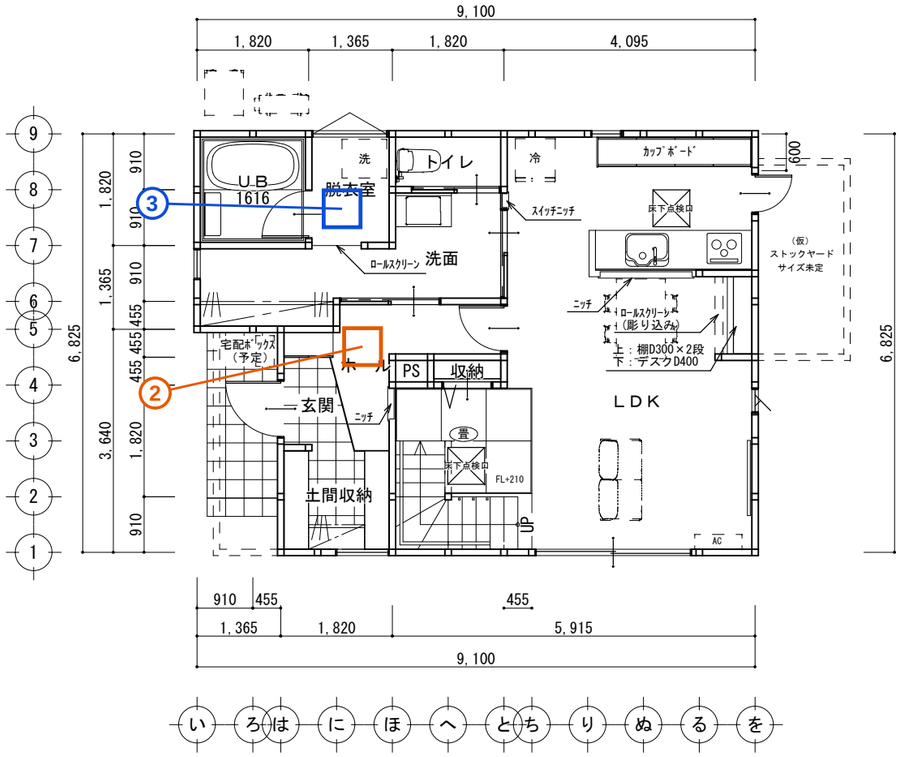

1階　平面図　S:1/100

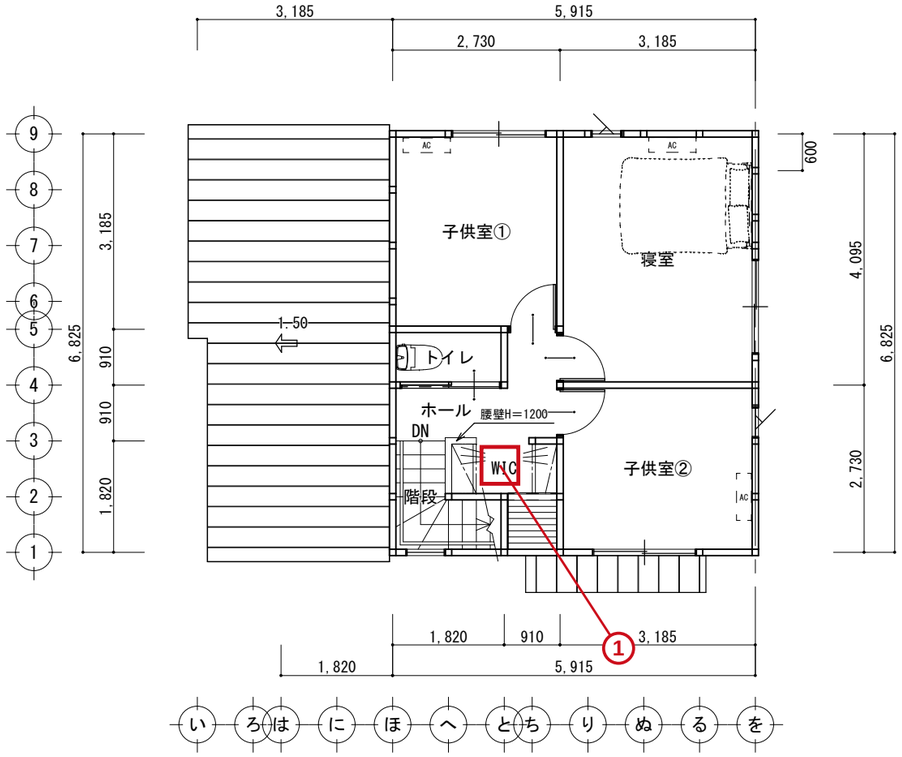

2階　平面図　S:1/100

注：床下点検口とは別用途。小屋裏へ入る開口は６００角を目安に検討。

工事名 来海　達也・有紀　様邸　新築工事	福山建築	管理者	設計者	担当者	図面名 平面図	図面No. A-6
備考	鳥取県倉吉市山根539-1　TEL 0858-27-0112　FAX 0858-27-0113	日付	日付	日付	縮尺 1/100	