


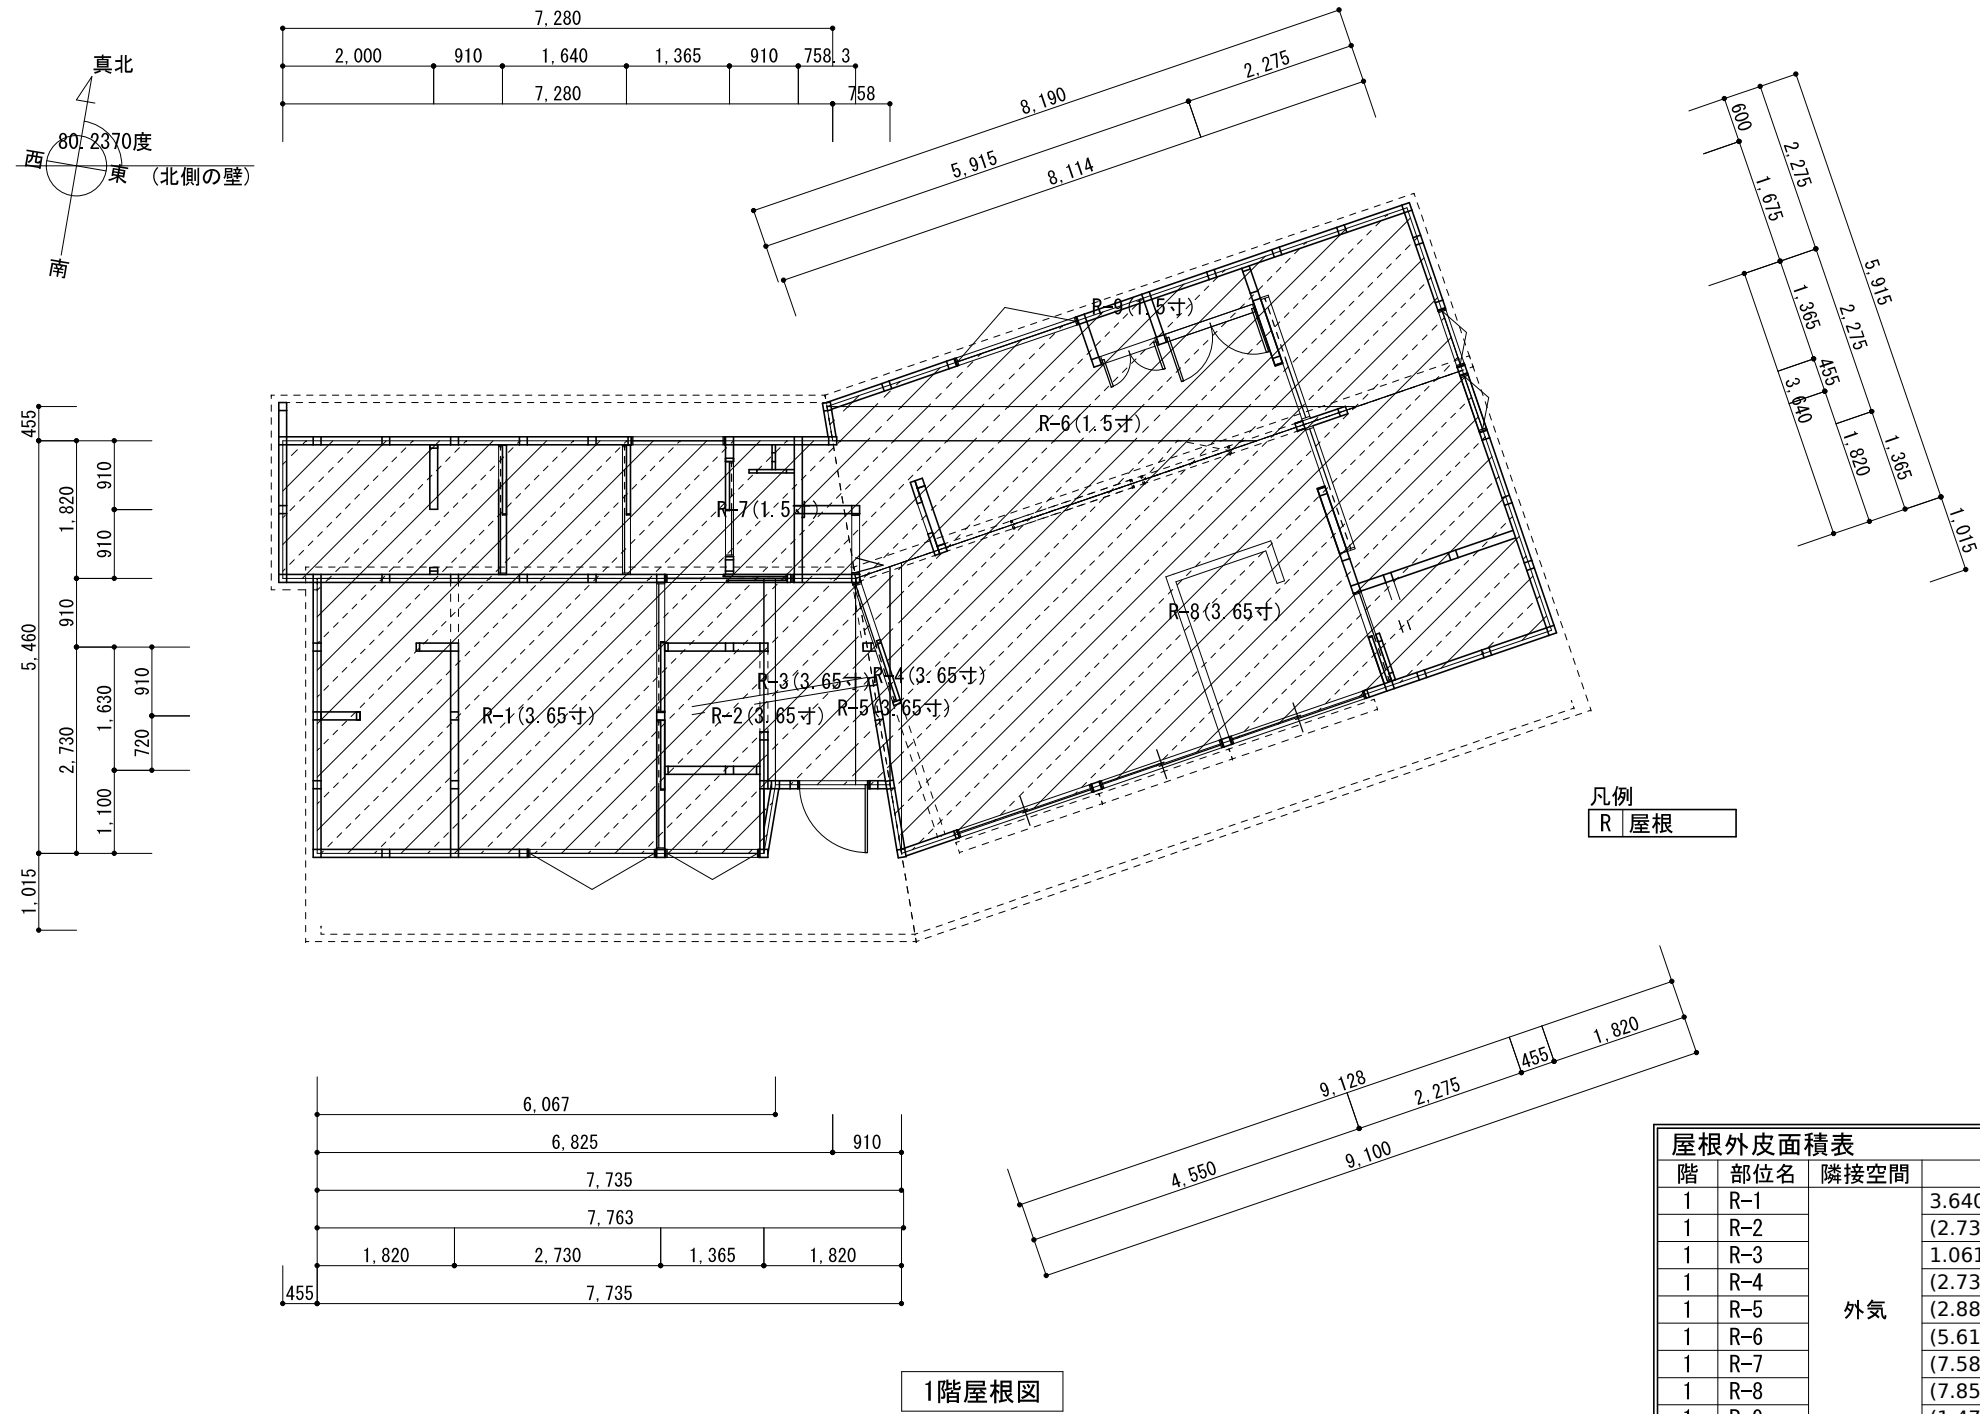

屋根外皮面積表						
階	部位名	隣接空間	計算式	面積[m ²]	小計[m ²]	仕様
1	R-1	外気	$3.640 \times 5.915 \times \sqrt{(4 \times 4 + 100)} \div 10$	23.19	94.764	屋根(1)
1	R-2		$(2.730 + 3.640) \times 0.151 \div 2.0 \times \sqrt{(4 \times 4 + 100)} \div 10$	0.52		
1	R-3		$1.061 \times 2.730 \times \sqrt{(4 \times 4 + 100)} \div 10$	3.12		
1	R-4		$(2.730 + 2.886) \times 0.455 \div 2.0 \times \sqrt{(4 \times 4 + 100)} \div 10$	1.38		
1	R-5		$(2.886 + 3.848) \times 0.151 \div 2.0 \times \sqrt{(4 \times 4 + 100)} \div 10$	0.55		
1	R-6		$(5.611 + 7.014) \times 0.455 \div 2.0 \times \sqrt{(1.5 \times 1.5 + 100)} \div 10$	2.90		
1	R-7		$(7.583 + 12.891) \times 1.820 \div 2.0 \times \sqrt{(1.5 \times 1.5 + 100)} \div 10$	18.84		
1	R-8		$(7.852 + 9.100) \times 3.640 \div 2.0 \times \sqrt{(4 \times 4 + 100)} \div 10$	33.23		
1	R-9		$(1.478 + 8.114) \times 2.275 \div 2.0 \times \sqrt{(1.5 \times 1.5 + 100)} \div 10$	11.03		
				面積合計	94.764	

注：小計・合計は外皮性能図1の94.764㎡を採用。記載寸法による再計算値は94.757㎡。