




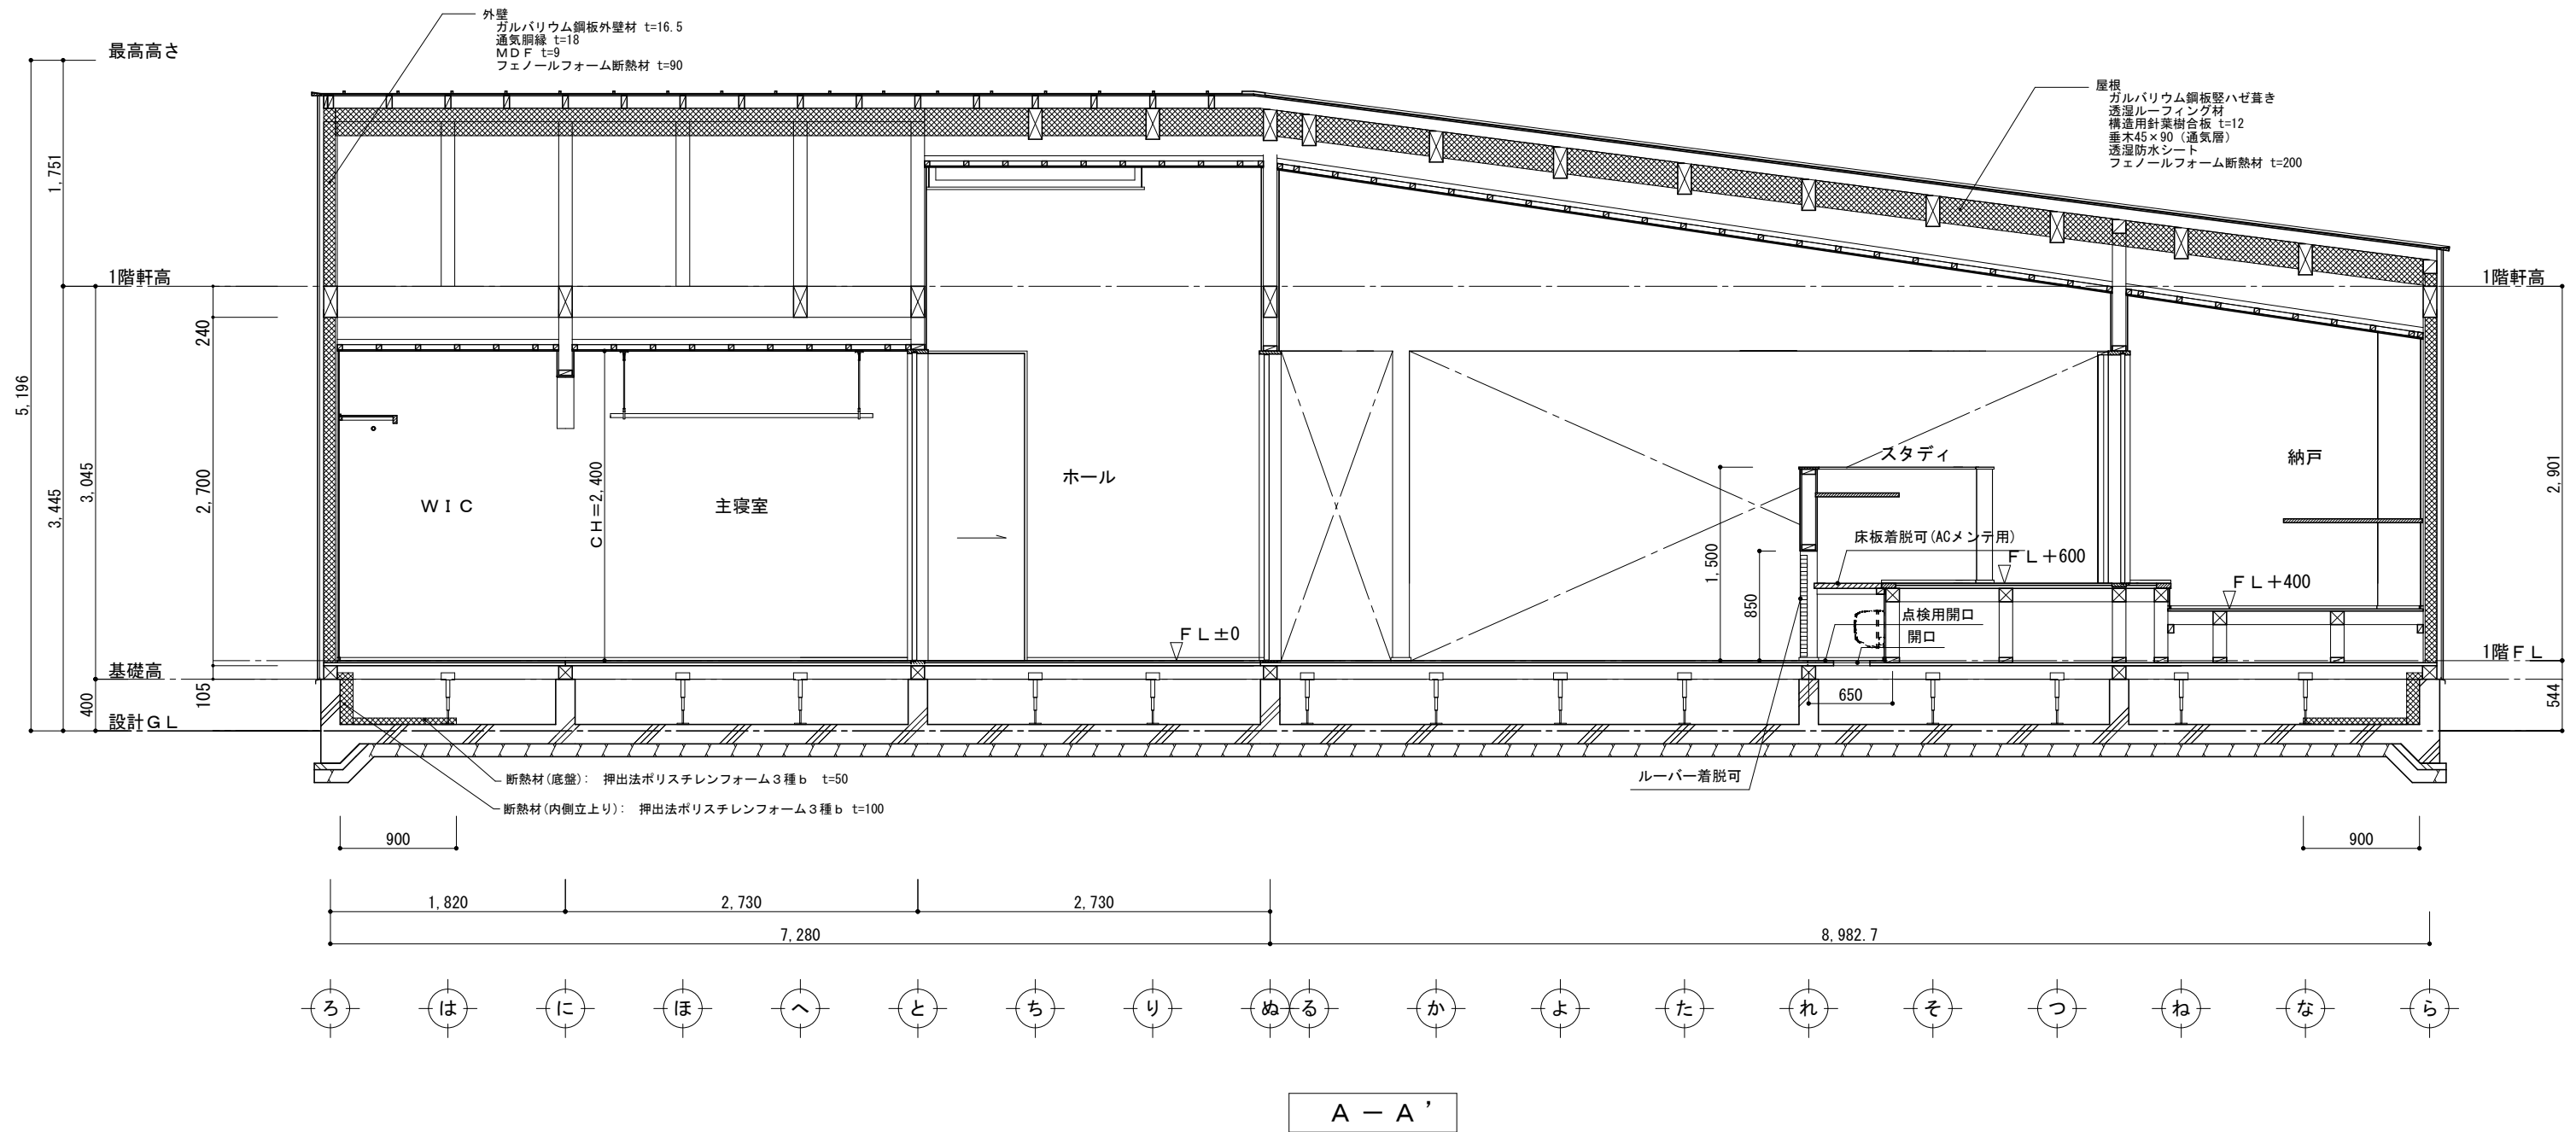

		井本賢也・明美邸新築工事	2026/01/27
断面詳細図 1		1 / 5 0	A - 1 0 - 1
福山建築			

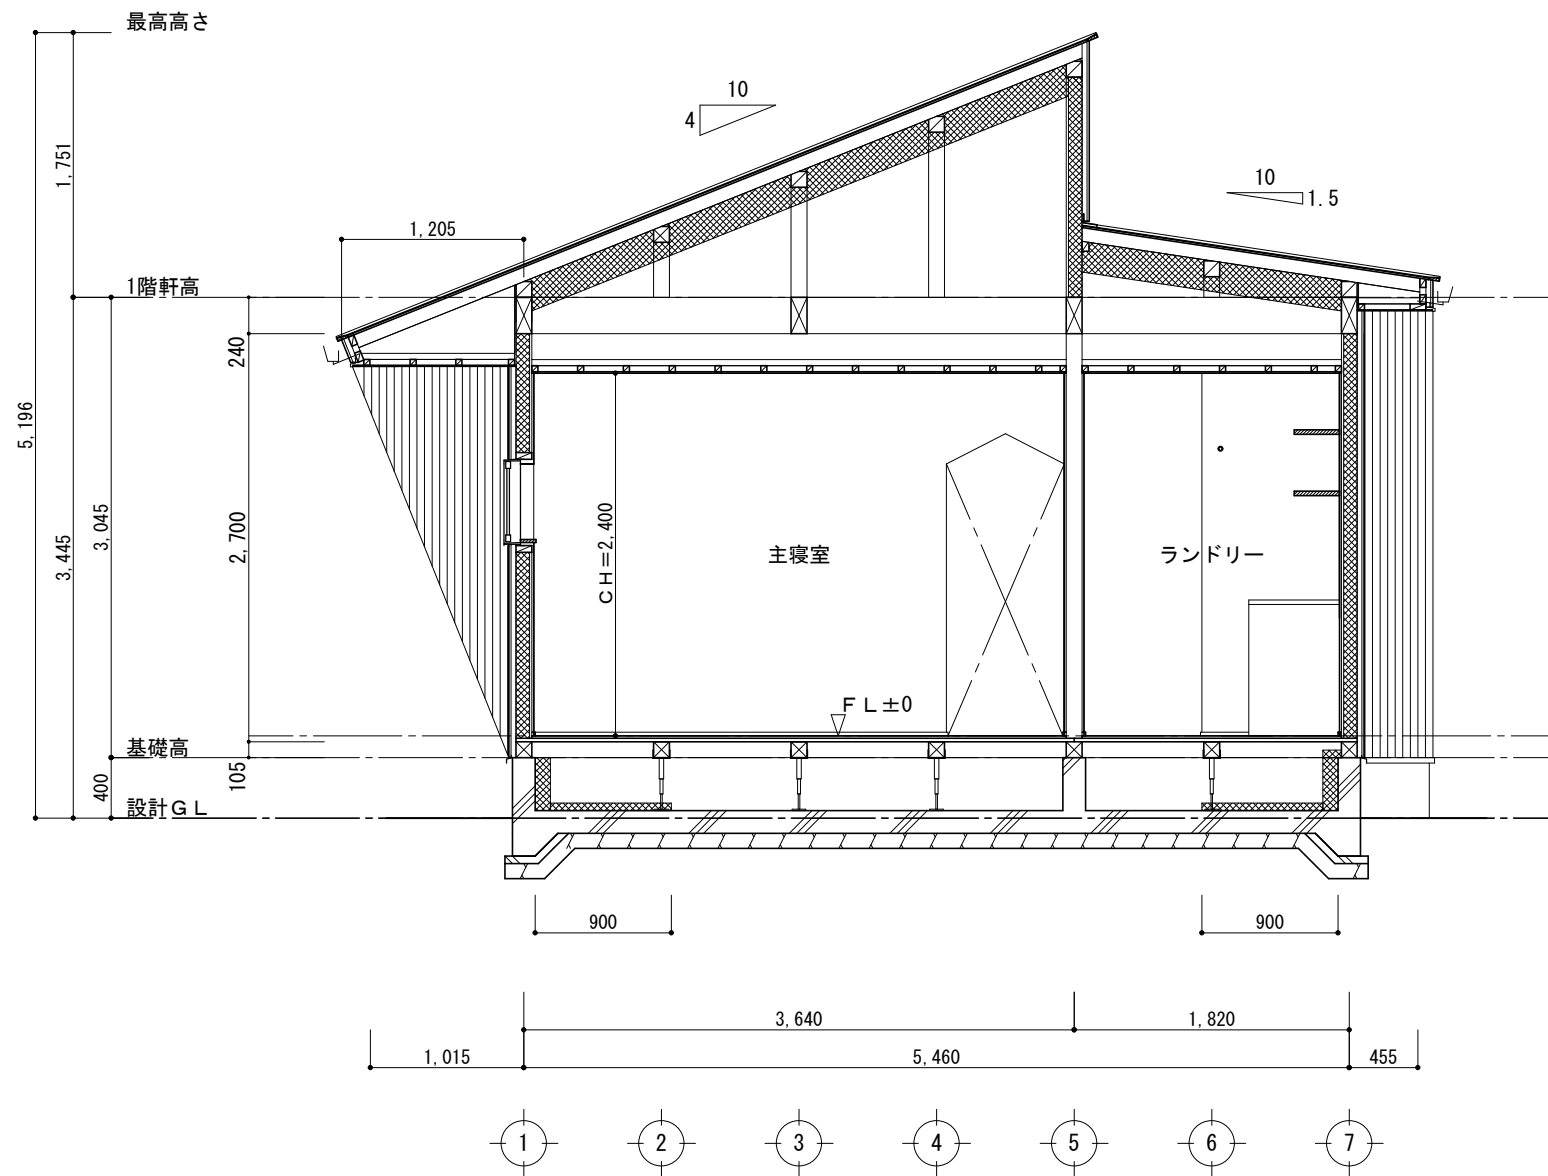

B - B'

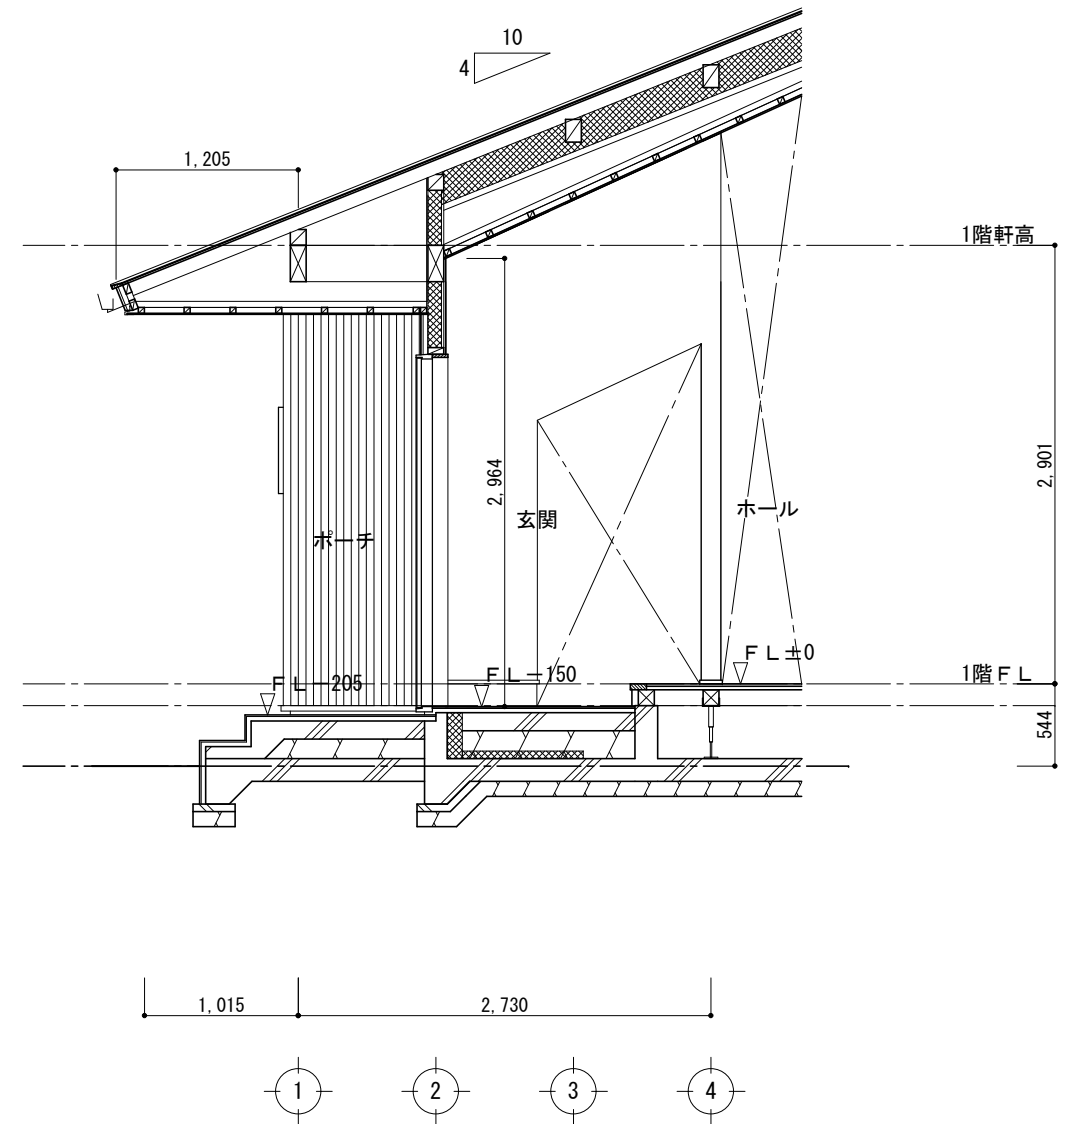

C

井本賢也・明美邸新築工事		2026/01/27
断面詳細図 2	1 / 5 0	A - 1 0 - 2
福山建築		