




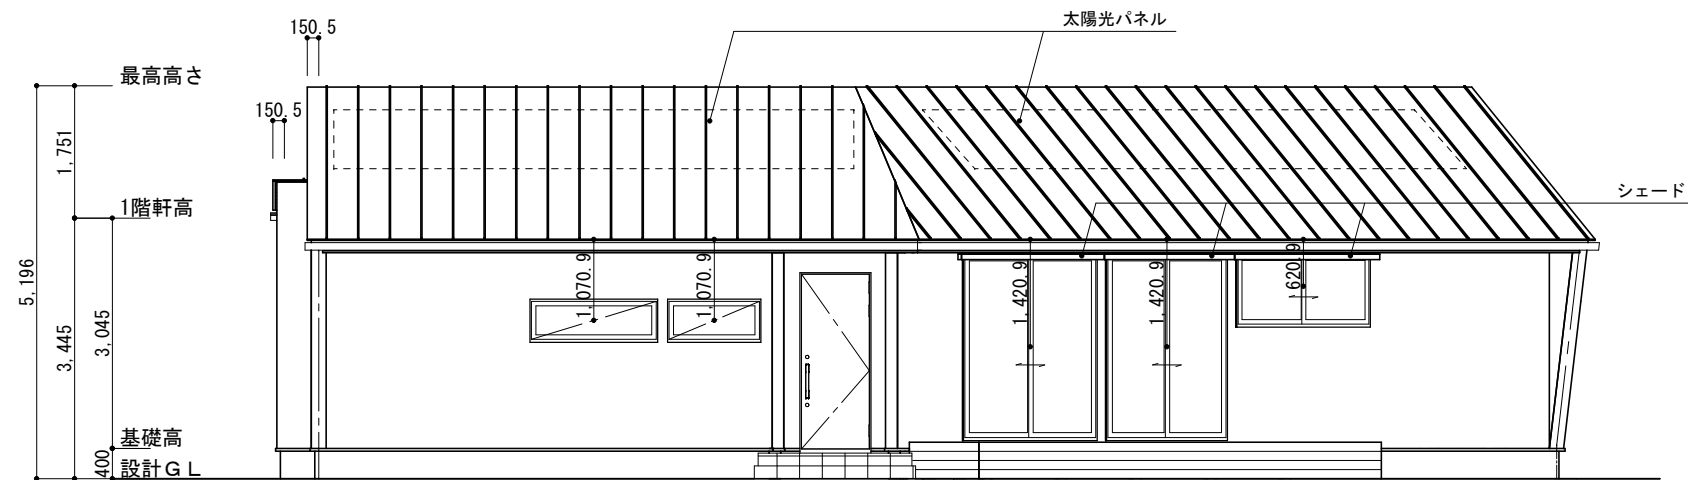


南側 立面図

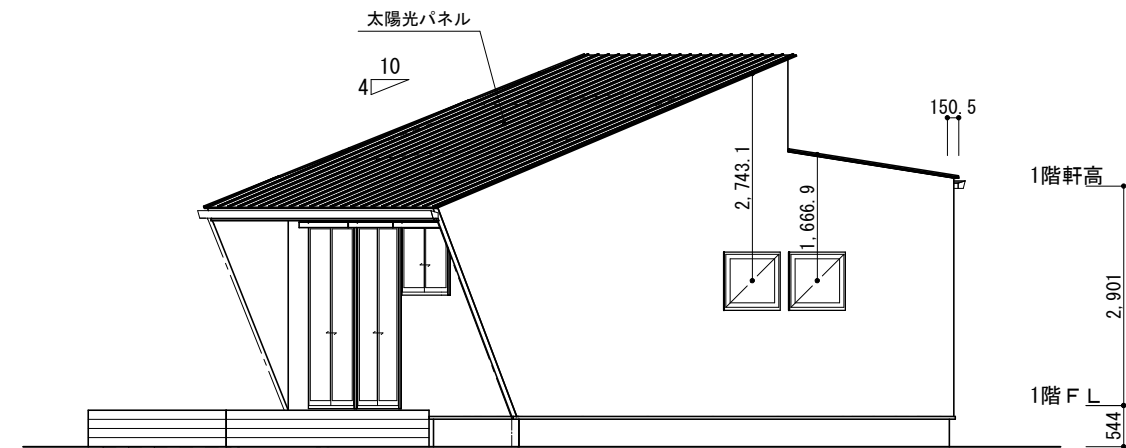

東側 立面図

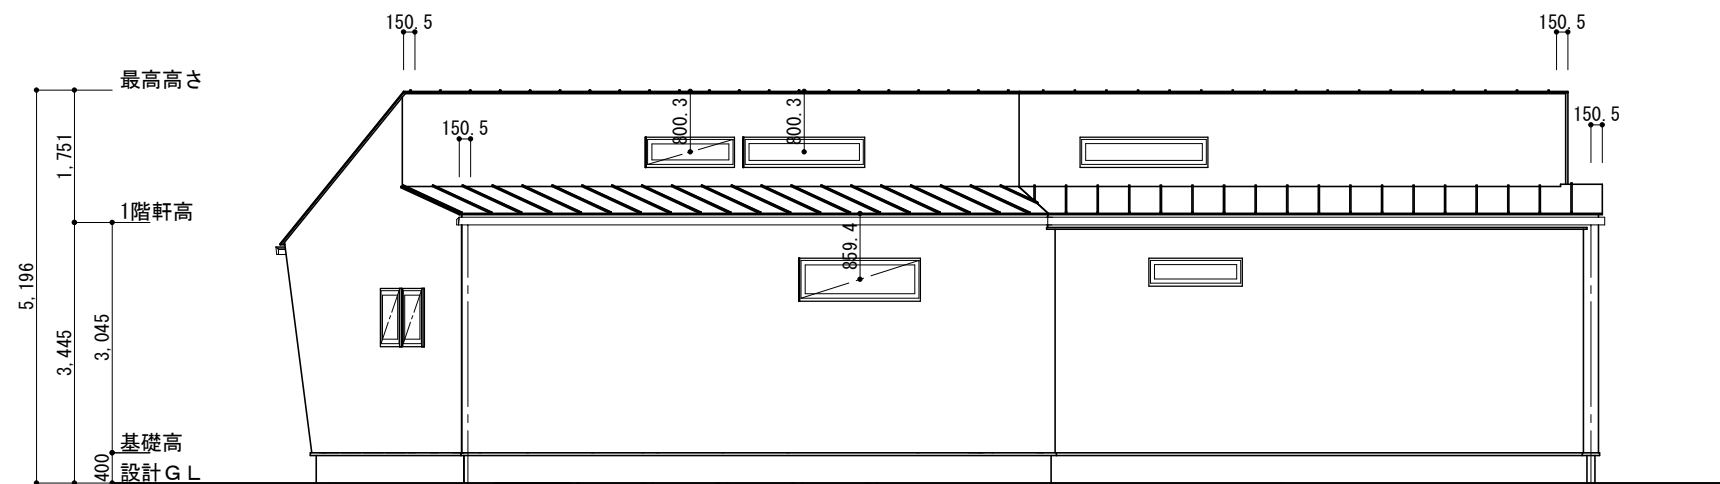

北側 立面図

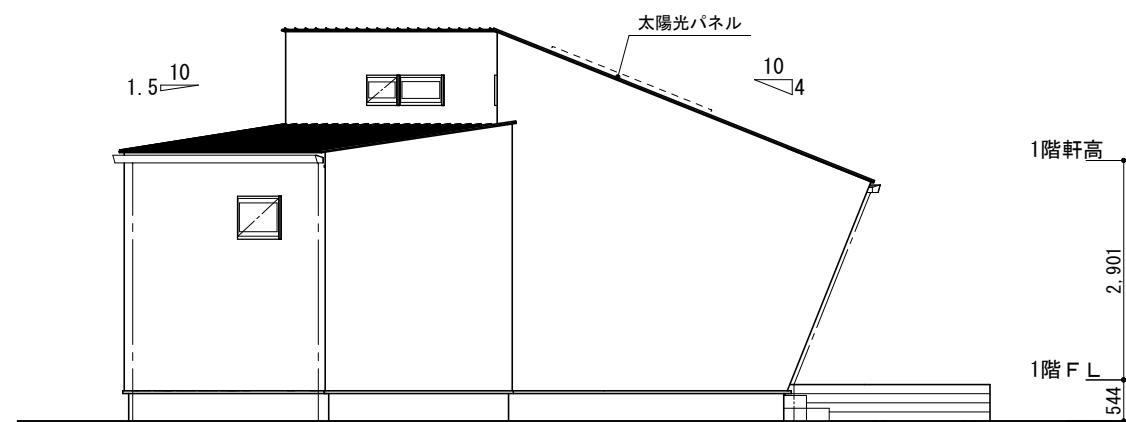

西側 立面図

- 外部仕上げ
- ・屋根：ガルバリウム鋼板タテハゼ葺き
 - ・外壁：ガルバリウム鋼板
 - ・軒裏：ケイ酸カルシウム板
 - ・サッシ外部色：ブラック

井本賢也・明美邸新築工事		2026/01/27
立面図	1 / 100	A - 7
福山建築		