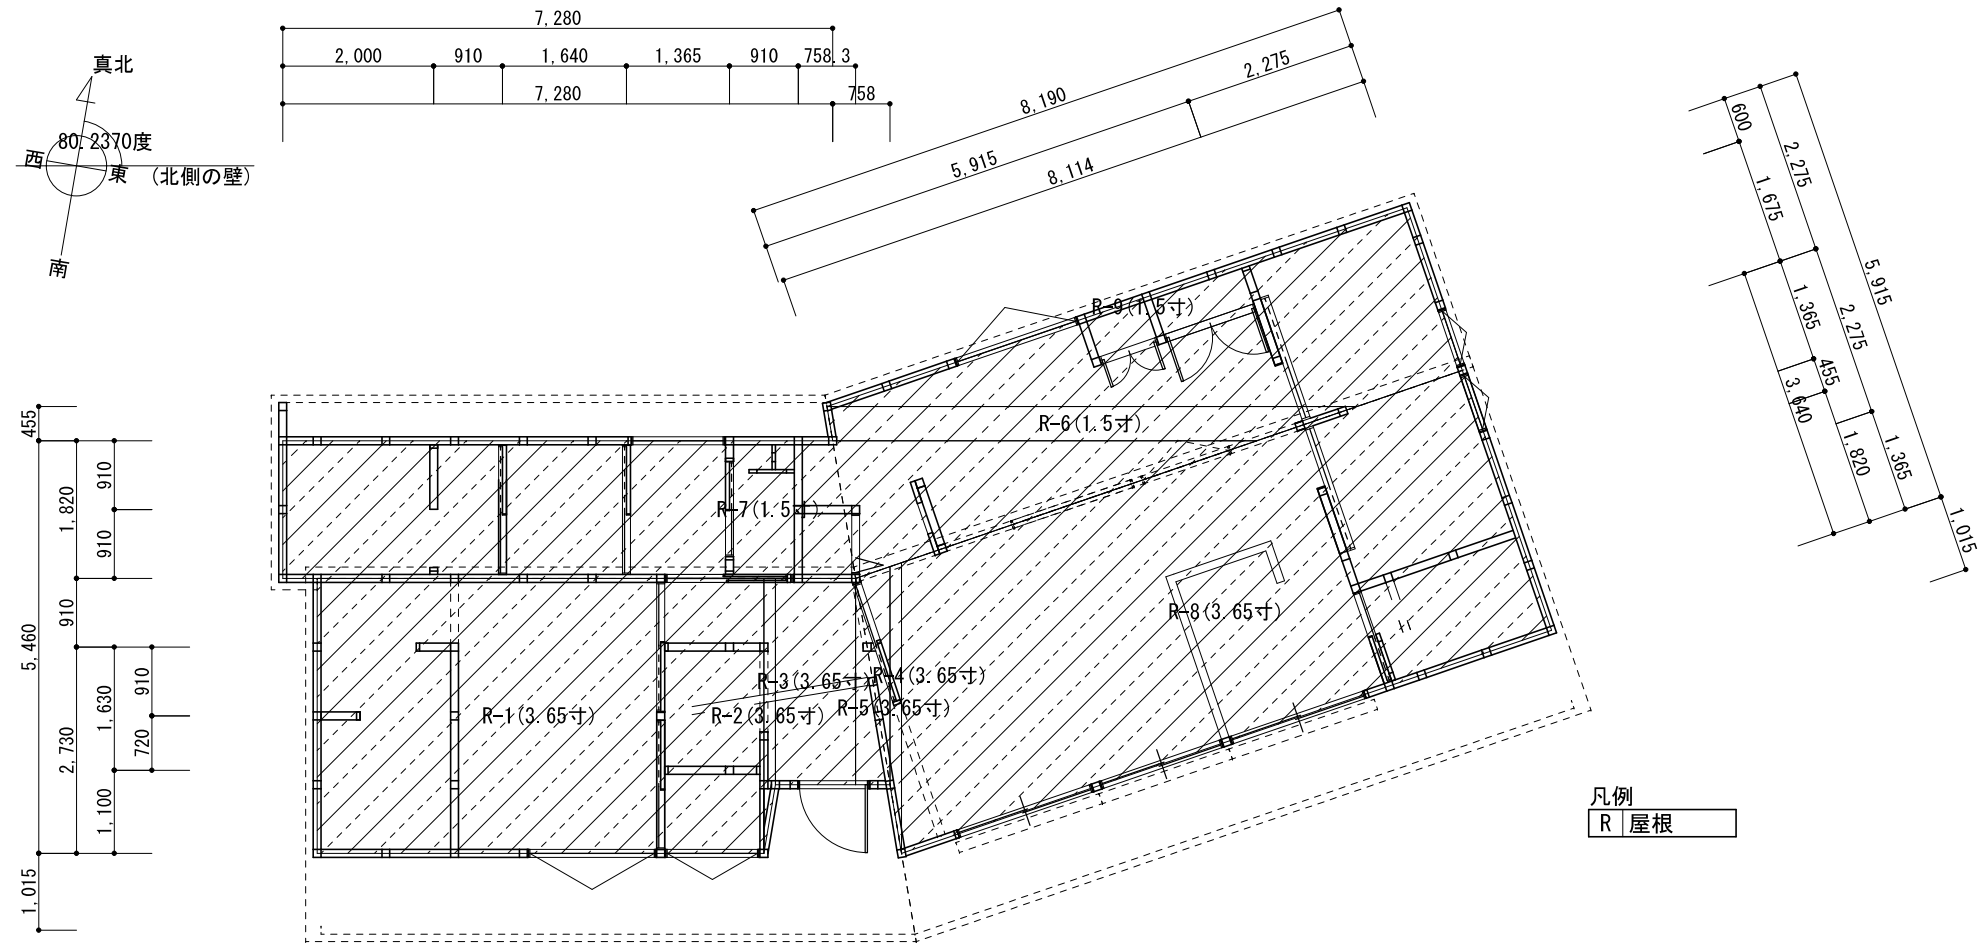


1階屋根図

屋根外皮面積表						
階	部位名	隣接空間	計算式	面積[m ²]	小計[m ²]	仕様
1	R-1	外気	$3.640 \times 5.915 \times \sqrt{(3.65 \times 3.65 + 100)} / 10$	22.920	94.045	屋根(1)
1	R-2		$(2.730 + 3.640) \times 0.151 \div 2.0 \times \sqrt{(3.65 \times 3.65 + 100)} / 10$	0.514		
1	R-3		$1.061 \times 2.730 \times \sqrt{(3.65 \times 3.65 + 100)} / 10$	3.083		
1	R-4		$(2.730 + 2.886) \times 0.455 \div 2.0 \times \sqrt{(3.65 \times 3.65 + 100)} / 10$	1.360		
1	R-5		$(2.886 + 3.848) \times 0.151 \div 2.0 \times \sqrt{(3.65 \times 3.65 + 100)} / 10$	0.544		
1	R-6		$(5.611 + 7.014) \times 0.455 \div 2.0 \times \sqrt{(1.5 \times 1.5 + 100)} / 10$	2.905		
1	R-7		$(7.583 + 12.891) \times 1.820 \div 2.0 \times \sqrt{(1.5 \times 1.5 + 100)} / 10$	18.841		
1	R-8		$(7.852 + 9.100) \times 3.640 \div 2.0 \times \sqrt{(3.65 \times 3.65 + 100)} / 10$	32.844		
1	R-9		$(1.478 + 8.114) \times 2.275 \div 2.0 \times \sqrt{(1.5 \times 1.5 + 100)} / 10$	11.034		
面積合計					94.045	