
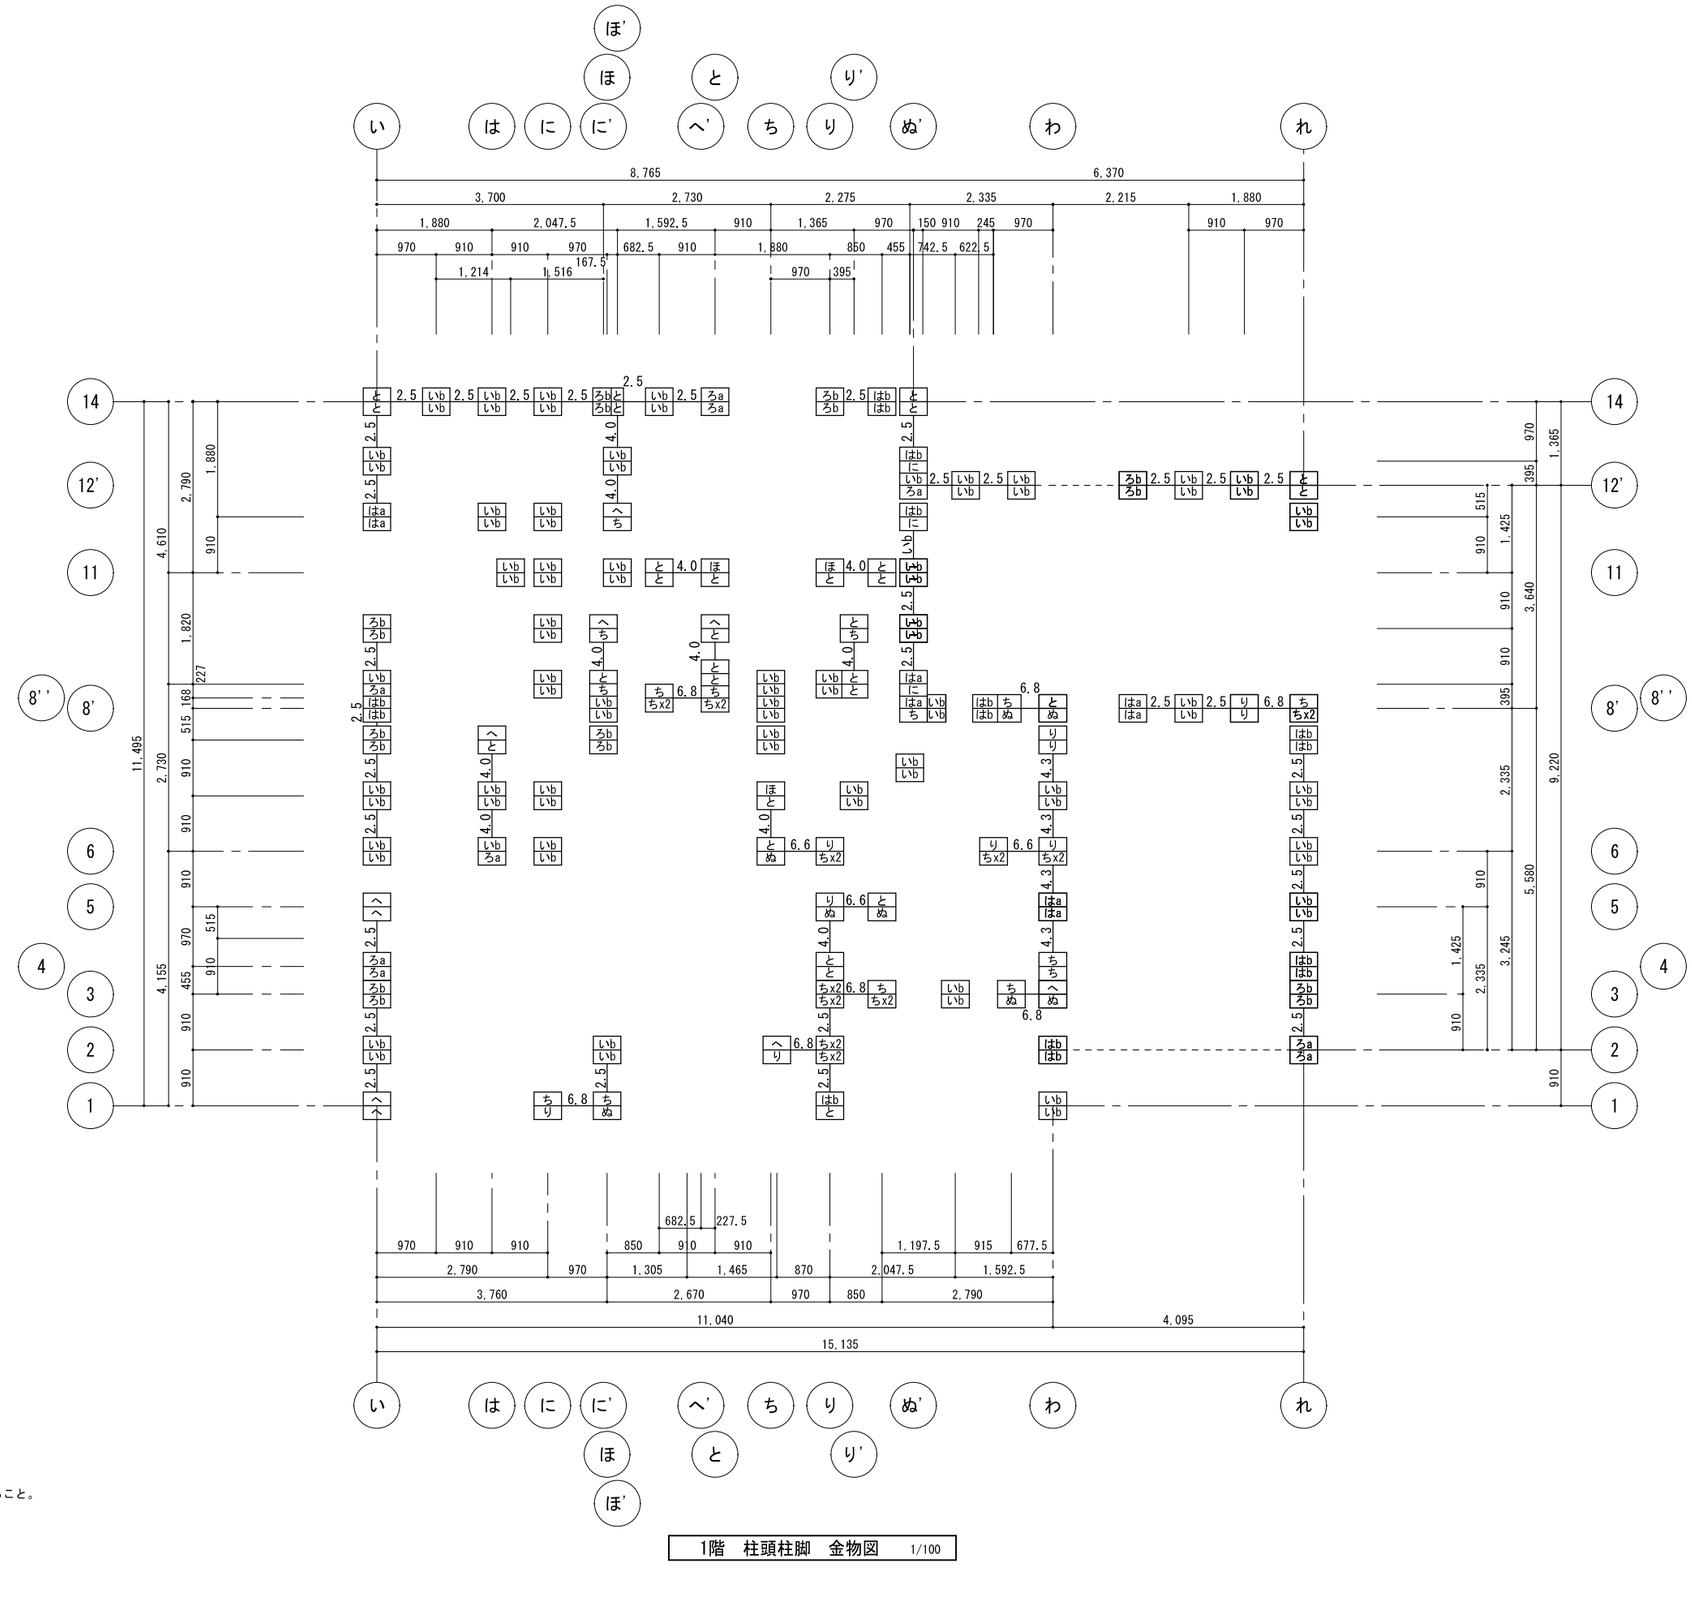


1階　柱頭柱脚　金物図　1/100

株式会社 R-be architects 二級建築士事務所　二級 東京都知事登録　第 16330 号 二級 建築士登録　第 83516 号　渡辺　隆一	工事名称 SEKI HOUSE PROJECT	sign	drawn	checked	date	drawing title 金物図1	scale 1/100		drawing No. S-21

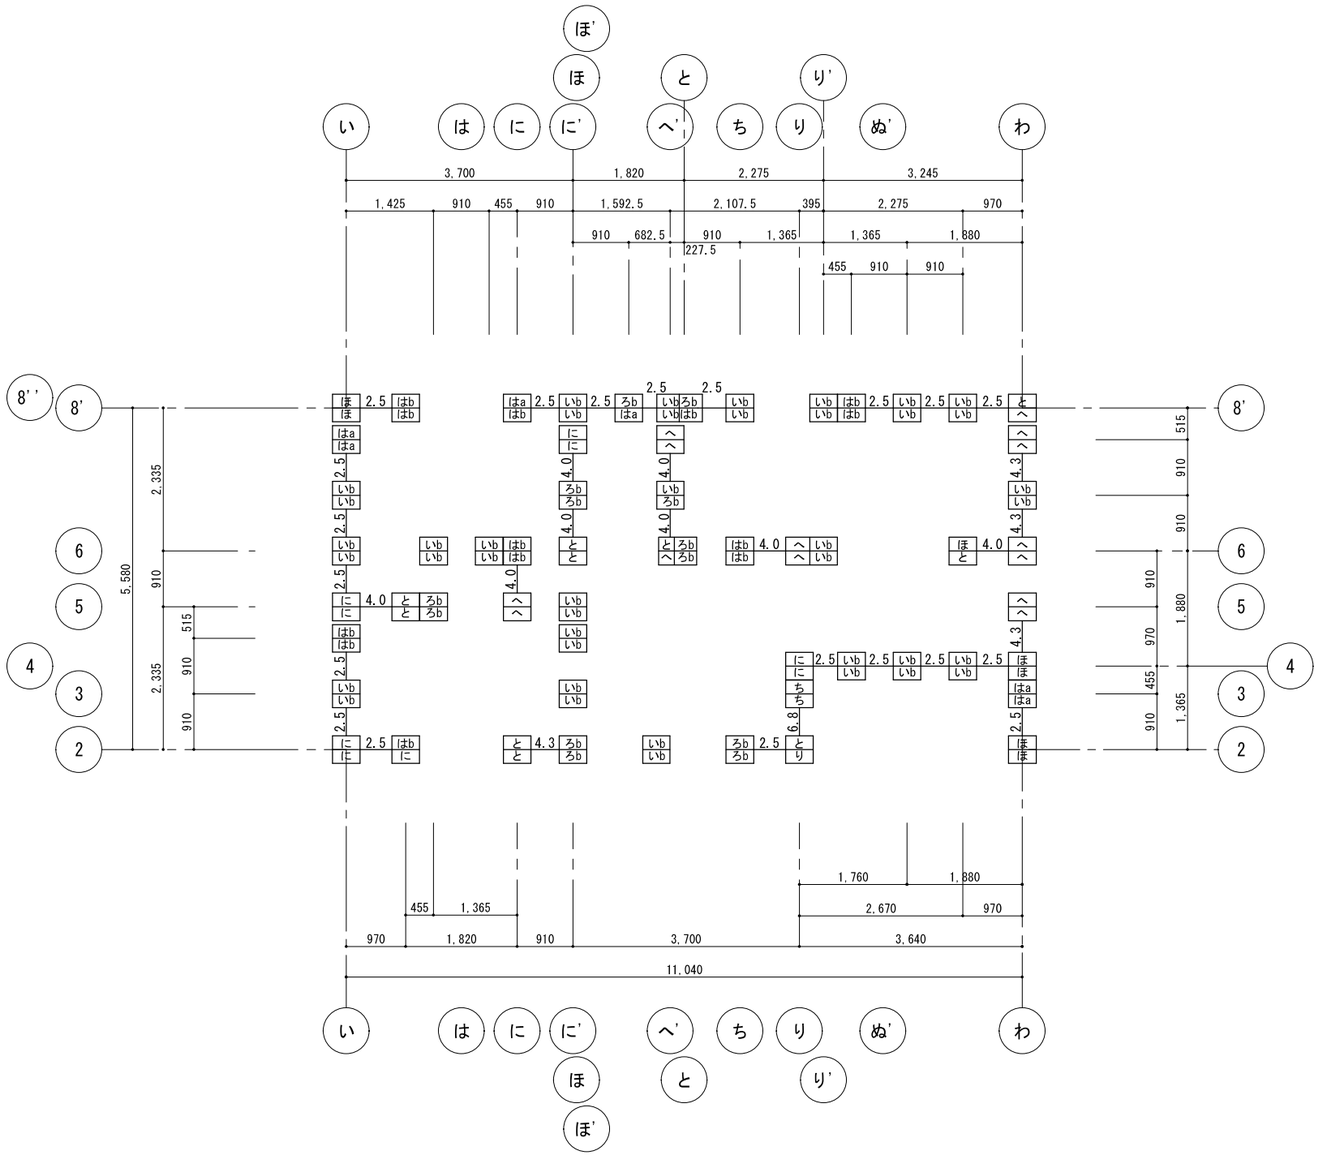

2階　登り1　柱頭柱脚　金物図　1/100

株式会社 R-be architects 二級建築士事務所　二級 東京都知事登録　第 16330 号 二級 建築士登録　第 83516 号　渡辺　隆一	工事名称 SEKI HOUSE PROJECT	sign	drawn	checked	date	drawing title 金物図2	scale 1/100		drawing No. S-22