關様邸　金物図　比較結果

正：２６０２１８關優汰邸 - 金物図．ｐｄｆ（Ｓ - ２１／Ｓ - ２２）

比較：關様邸金物図面０５１２．ｐｄｆ（土台伏図／２階床伏図、印刷日時　２０２６年5月１１日）

確認結果：柱頭・柱脚の大分類記号は、１階では一致。２階の柱脚に７か所の相違。

表中は「柱頭／柱脚」。正図の凡例に従い、上段を柱頭、下段を柱脚として照合。

Ｎｏ.	正図の位置	０５１２図の位置	０５１２図	正図	正図へ合わせる記号修正
1	り－２	り－２	と／ち×２	と／り	柱脚：ち×２　→　り
2	り－３	り－３	ち／ち×２	ち／ち	柱脚：ち×２　→　ち
3	り－６	り－６	へ／り	へ／へ	柱脚：り　→　へ
4	わより９７０mm左－６	を－６	ほ／り	ほ／と	柱脚：り　→　と
5	わ－６	わ－６	へ／り	へ／へ	柱脚：り　→　へ
6	わ－８＇より５１５mm下	わ－８	へ／り	へ／へ	柱脚：り　→　へ
7	わ－８＇	又た又８（青字注記）	と／空欄	と／へ	柱脚：へ　の記載がない

商品表示：Ｎｏ．１・２の０５１２図は柱脚Ｈｉ４３×２。Ｎｏ．３～６は柱脚Ｈｉ２８。Ｎｏ．７は柱脚商品表示も空欄。

照合上の注意


・正図の「いｂ・ろａ・ろｂ・はａ・はｂ」等のａ／ｂ区別は、０５１２図では省略されています。

・正図には記号と商品型番の対応表がないため、商品同等性・必要耐力の判定まではできません。

・０５１２図のＬ８００／Ｌ８５０の両引きボルト、Ｌ５５０の偏心座金付きボルトの追記は、正図にはありません。
　上下階接合の納まりに関わるため、記号を合わせる際に追記をそのまま削除せず、設計者へ確認してください。

後続ページ：０５１２図の１階・２階、続いて正図の１階・２階。２階の相違箇所に共通番号を表示。

これは図面間の表記比較です。金物の取付方向・施工状態や構造計算の妥当性は対象に含みません。

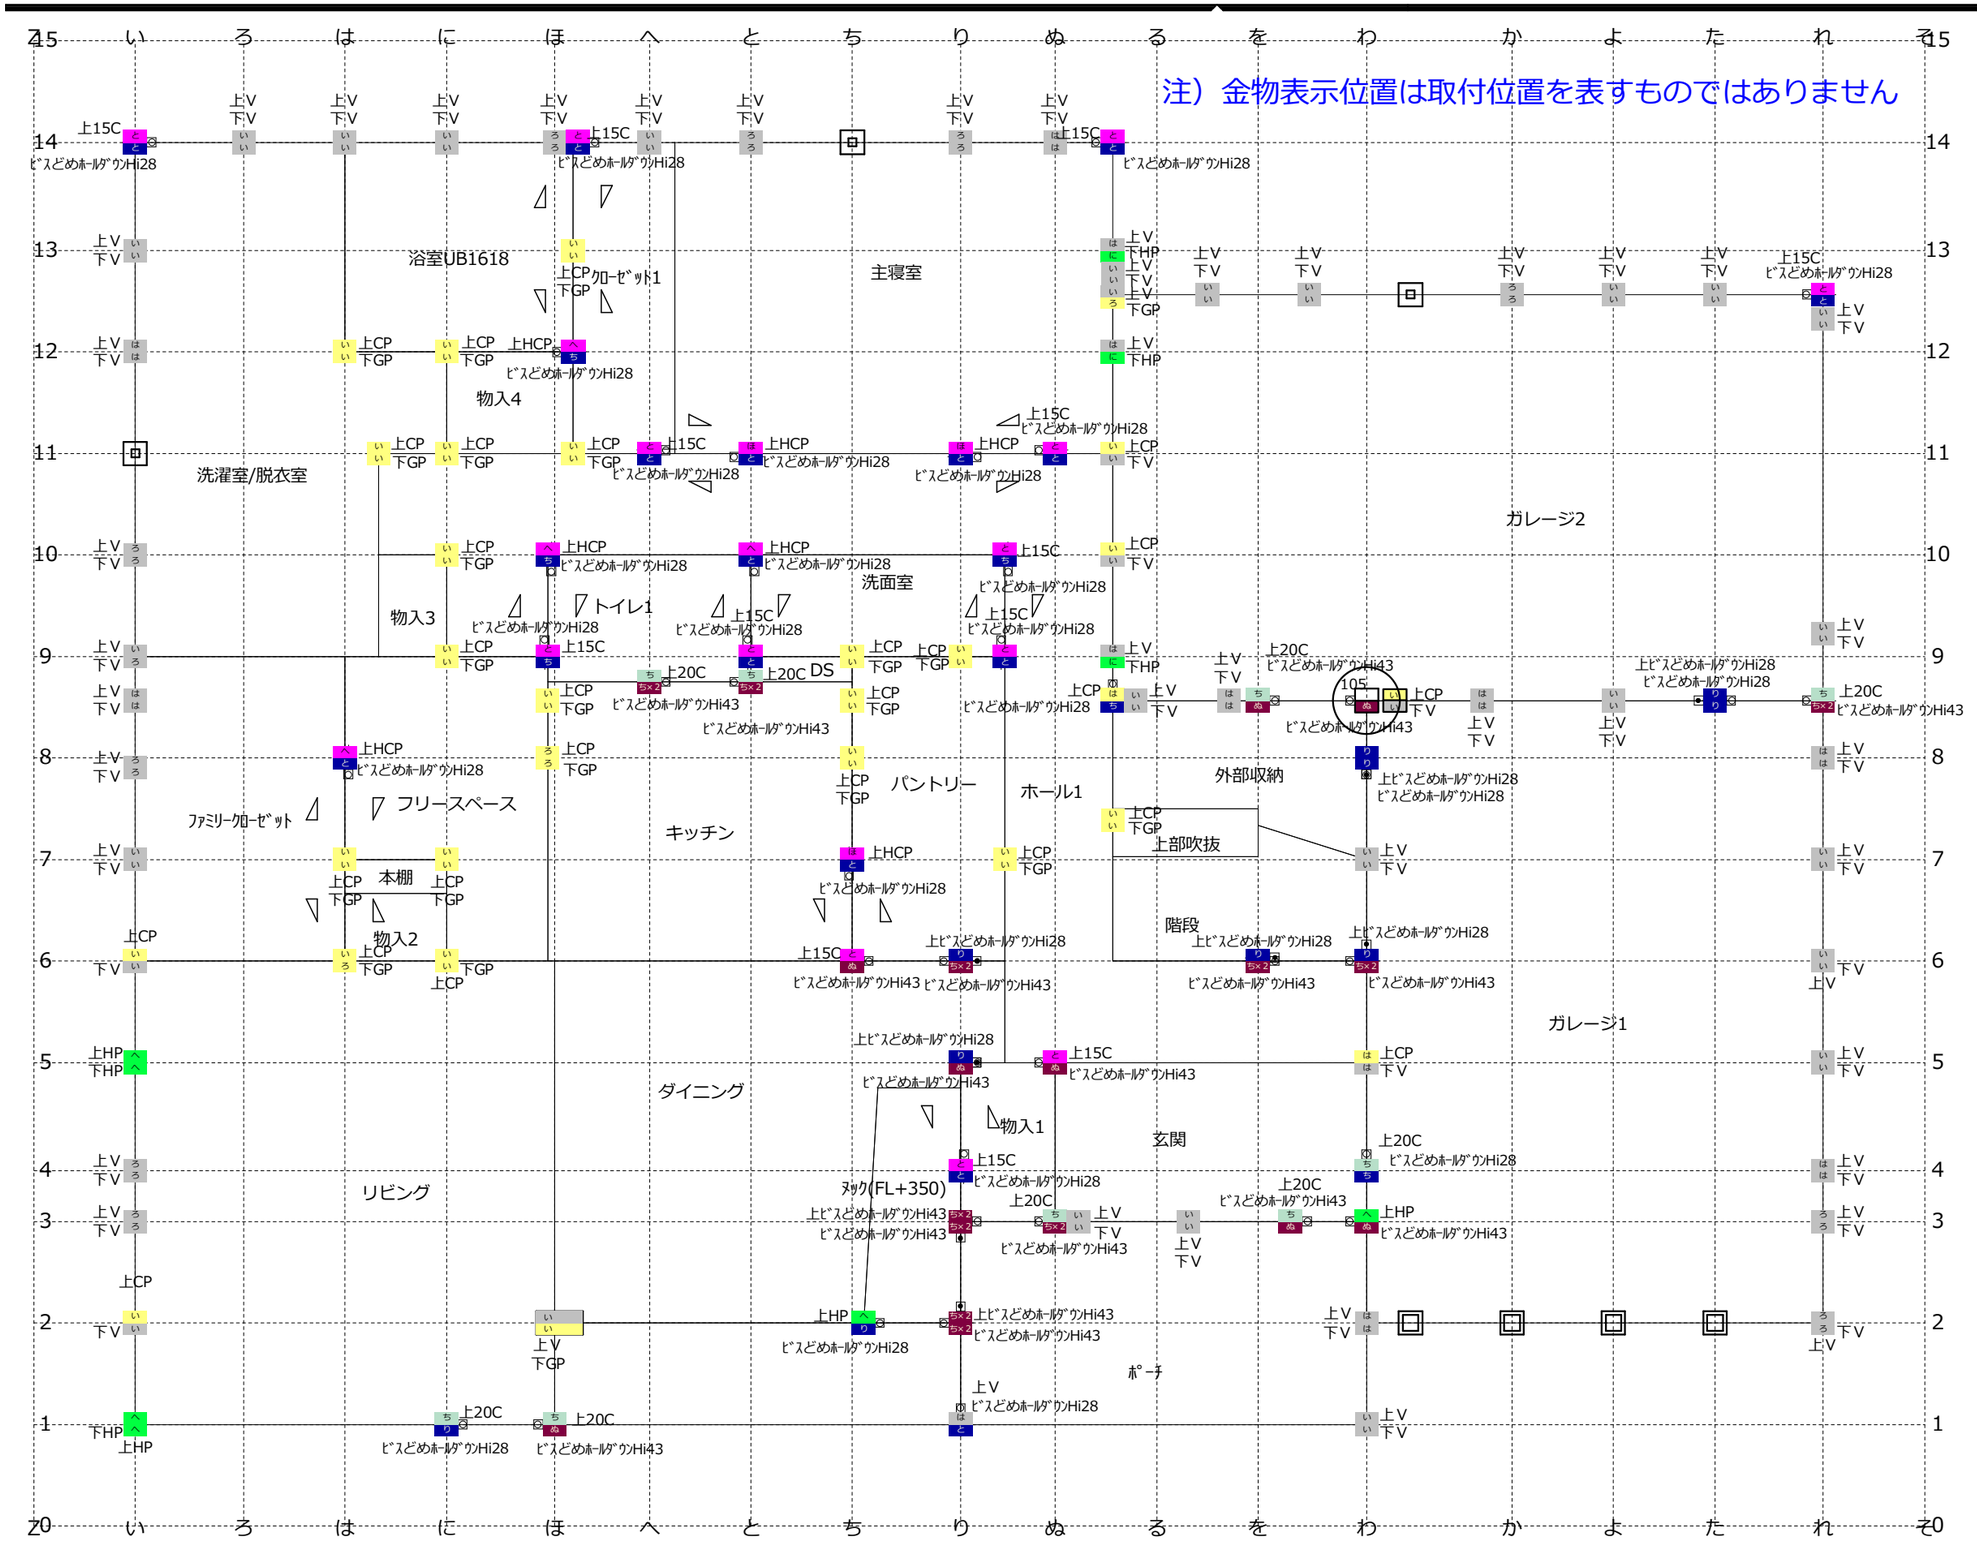

タナカ金物選定システム

い		
	V	ﾌﾗｯﾄﾌﾟﾚｰﾄｽﾘﾑ
	CP	ﾌｯｸｺｰﾅｰ床合板仕様
	GP	ﾌｯｸｺｰﾅｰ床合板仕様
ろ		
	V	ﾌﾗｯﾄﾌﾟﾚｰﾄｽﾘﾑ
	CP	ﾌｯｸｺｰﾅｰ床合板仕様
	GP	ﾌｯｸｺｰﾅｰ床合板仕様
は		
	V	ﾌﾗｯﾄﾌﾟﾚｰﾄｽﾘﾑ
	CP	ﾌｯｸｺｰﾅｰ床合板仕様
	GP	ﾌｯｸｺｰﾅｰ床合板仕様
に		
	HP	ﾒﾀﾞﾌﾟﾚｰﾄSD 10kN
	HCP	ﾒﾀﾞｺｰﾅｰ15kNⅡ床合板仕様
	HGP	ﾒﾀﾞｺｰﾅｰ15kNⅡ床合板仕様
	I外	
	I内	
	PH	
	WP	
	WPH	
ほ	HP	ﾒﾀﾞﾌﾟﾚｰﾄSD 10kN
	HCP	ﾒﾀﾞｺｰﾅｰ15kNⅡ床合板仕様
	HGP	ﾒﾀﾞｺｰﾅｰ15kNⅡ床合板仕様
	I外	
	I内	
	PH	
	WP	
	WPH	
へ	HP	ﾒﾀﾞﾌﾟﾚｰﾄSD 10kN
	HCP	ﾒﾀﾞｺｰﾅｰ15kNⅡ床合板仕様
	HGP	ﾒﾀﾞｺｰﾅｰ15kNⅡ床合板仕様
と	15C	ﾒﾀﾞｺｰﾅｰ15kNⅡ床合板仕様
	15G	ﾒﾀﾞｺｰﾅｰ15kNⅡ床合板仕様
		ﾋﾞｽどめﾎｰﾙﾀﾞｳﾝHi28
ち	20C	ﾒﾀﾞｺｰﾅｰ20kN用床合板仕様
	20G	ﾒﾀﾞｺｰﾅｰ20kN用床合板仕様
		ﾋﾞｽどめﾎｰﾙﾀﾞｳﾝHi28
り		ﾋﾞｽどめﾎｰﾙﾀﾞｳﾝHi28
ぬ		ﾋﾞｽどめﾎｰﾙﾀﾞｳﾝHi43
ち×2		ﾋﾞｽどめﾎｰﾙﾀﾞｳﾝHi43

○	通　柱	◎	ﾎｰﾙﾀﾞｳﾝﾎﾞﾙﾄ 柱　脚
□	管　柱	◉	ﾎｰﾙﾀﾞｳﾝﾎﾞﾙﾄ 柱　頭
×	下階柱	⊙	羽子板ﾎﾞﾙﾄ 柱　脚
○	小屋束	●	羽子板ﾎﾞﾙﾄ 柱　頭
▨	耐力壁	▬	短ざく金物
◺	筋かい		


〒

TEL　　FAX

検図	設計	製図

モジュール	910		工法	在来工法		
階　高	1F	2940	2F	2730	3F	
屋根勾配	1F	1.5	2F	1.5	3F	

工事名称	關様邸（福山建築）金物図面	図面名称	土台伏図
印刷日時	2026年 5月11日 14:59	縮尺	1/55
		物件番号	25-46829

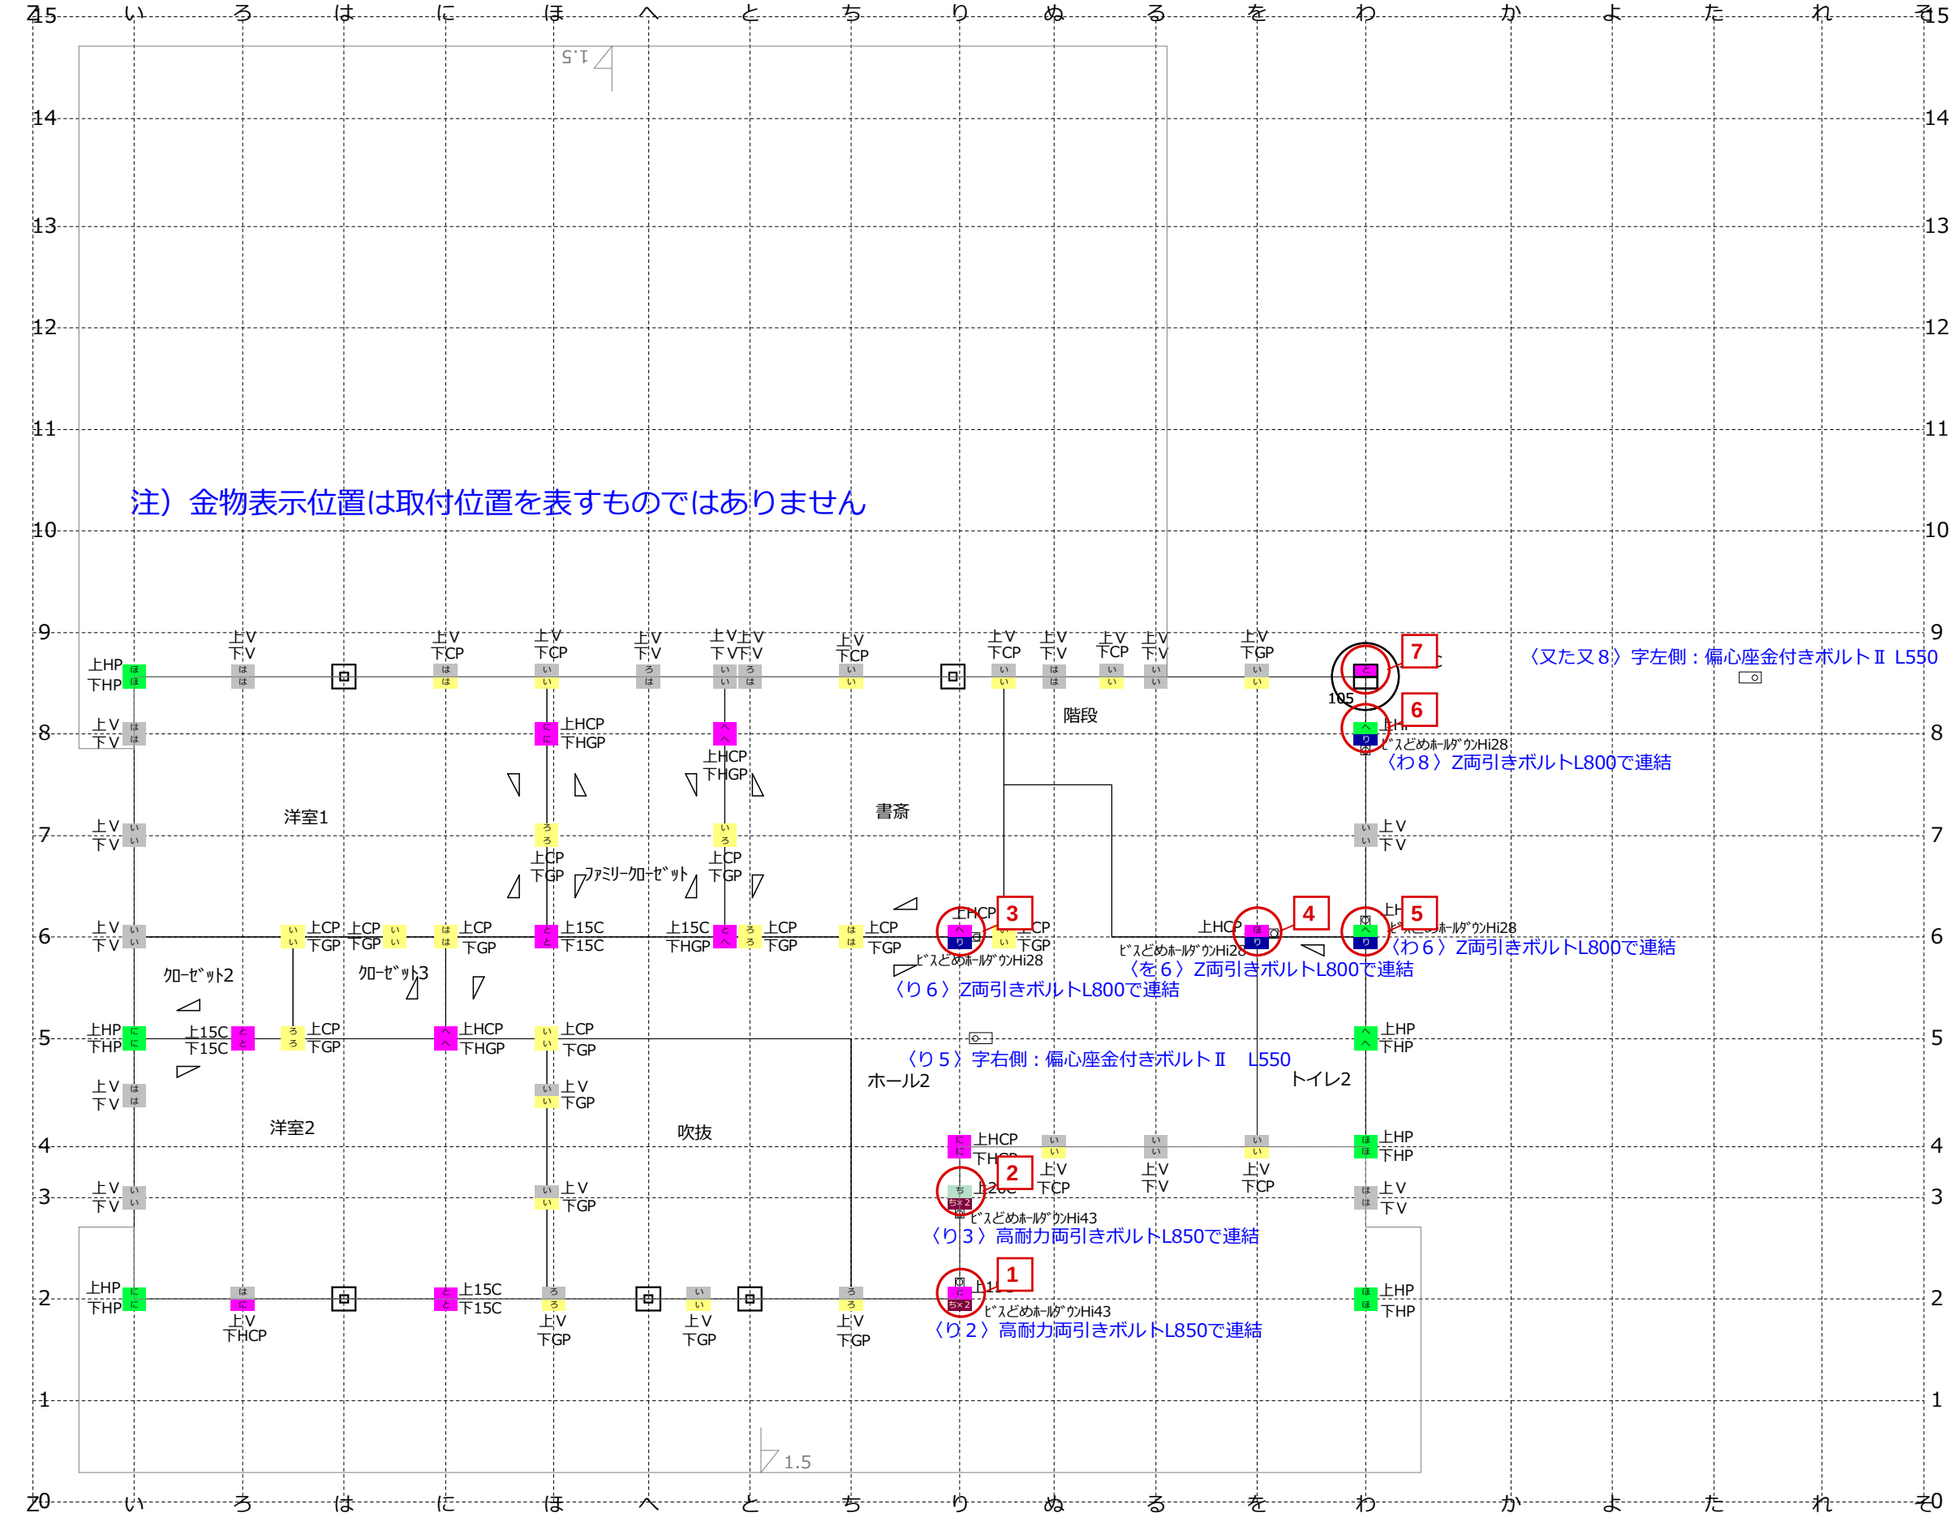

タナカ金物選定システム

い		
	V	ﾌﾗｯﾄﾌﾟﾚｰﾄｽﾘﾑ
	CP	ﾌｯｸｺｰﾅｰ床合板仕様
	GP	ﾌｯｸｺｰﾅｰ床合板仕様
ろ		
	V	ﾌﾗｯﾄﾌﾟﾚｰﾄｽﾘﾑ
	CP	ﾌｯｸｺｰﾅｰ床合板仕様
	GP	ﾌｯｸｺｰﾅｰ床合板仕様
は		
	V	ﾌﾗｯﾄﾌﾟﾚｰﾄｽﾘﾑ
	CP	ﾌｯｸｺｰﾅｰ床合板仕様
	GP	ﾌｯｸｺｰﾅｰ床合板仕様
に		
	HP	ﾒｶﾞﾌﾟﾚｰﾄSD 10kN
	HCP	ﾒｶﾞｺｰﾅｰ15kNⅡ床合板仕様
	HGP	ﾒｶﾞｺｰﾅｰ15kNⅡ床合板仕様
	Ⅰ外	
	Ⅰ内	
	PH	
	WP	
	WPH	
ほ	HP	ﾒｶﾞﾌﾟﾚｰﾄSD 10kN
	HCP	ﾒｶﾞｺｰﾅｰ15kNⅡ床合板仕様
	HGP	ﾒｶﾞｺｰﾅｰ15kNⅡ床合板仕様
	Ⅰ外	
	Ⅰ内	
	PH	
	WP	
	WPH	
へ	HP	ﾒｶﾞﾌﾟﾚｰﾄSD 10kN
	HCP	ﾒｶﾞｺｰﾅｰ15kNⅡ床合板仕様
	HGP	ﾒｶﾞｺｰﾅｰ15kNⅡ床合板仕様
と	15C	ﾒｶﾞｺｰﾅｰ15kNⅡ床合板仕様
	15G	ﾒｶﾞｺｰﾅｰ15kNⅡ床合板仕様
		ﾋﾞｽどめﾎｰﾙﾀﾞｳﾝHi28
ち	20C	ﾒｶﾞｺｰﾅｰ20kN用床合板仕様
	20G	ﾒｶﾞｺｰﾅｰ20kN用床合板仕様
		ﾋﾞｽどめﾎｰﾙﾀﾞｳﾝHi28
り		ﾋﾞｽどめﾎｰﾙﾀﾞｳﾝHi28
ぬ		ﾋﾞｽどめﾎｰﾙﾀﾞｳﾝHi43
ち×２		ﾋﾞｽどめﾎｰﾙﾀﾞｳﾝHi43

□	通　柱	□	ﾎｰﾙﾀﾞｳﾝﾎﾞﾙﾄ 柱　脚
□	管　柱	◉	ﾎｰﾙﾀﾞｳﾝﾎﾞﾙﾄ 柱　頭
×	下階柱	⏀	羽子板ボルト 柱　脚
○	小屋束	●	羽子板ボルト 柱　頭
▨	耐力壁	▬	短ざく金物
◺	筋かい		

〒


TEL　　FAX

検図	設計	製図

モジュール	910		工法	在来工法		
階　高	1F	2940	2F	2730	3F	
屋根勾配	1F	1.5	2F	1.5	3F	

工事名称	關様邸（福山建築）金物図面	図面名称	２階床伏図
印刷日時	2026年 5月11日 14:59	縮尺	1/55
		物件番号	25-46829


正図 / 1F

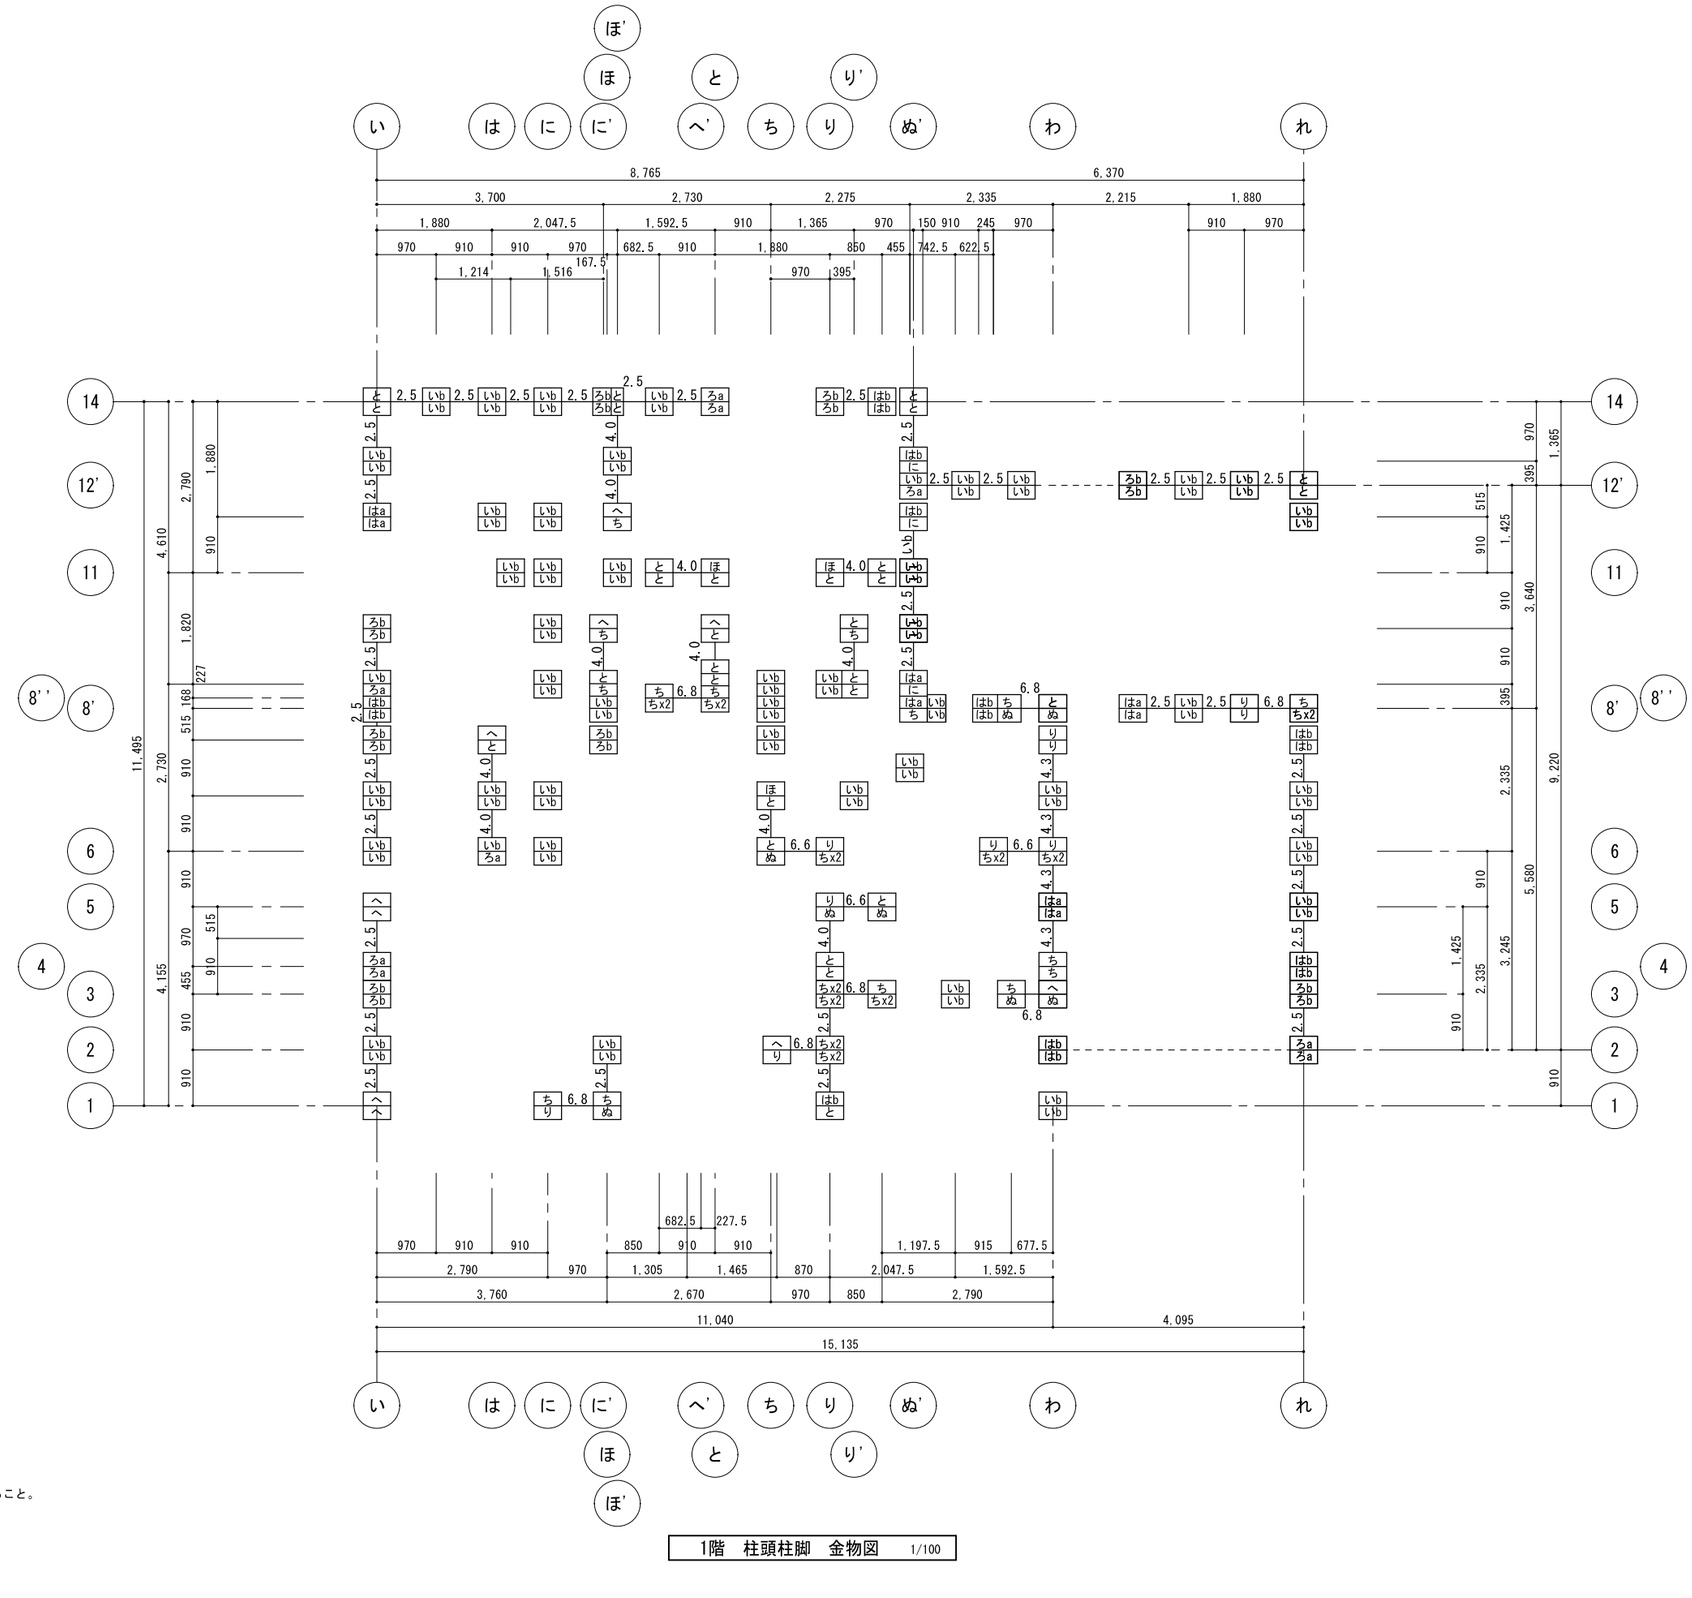

1階　柱頭柱脚　金物図　1/100

株式会社 R-be architects 二級建築士事務所　二級 東京都知事登録　第 16330 号 二級 建築士登録　第 83516 号　渡辺　隆一	工事名称 SEKI HOUSE PROJECT	sign	drawn	checked	date	drawing title 金物図1	scale 1/100		drawing No. S-21

正図　/　２Ｆ　-　赤番号は比較表に対応

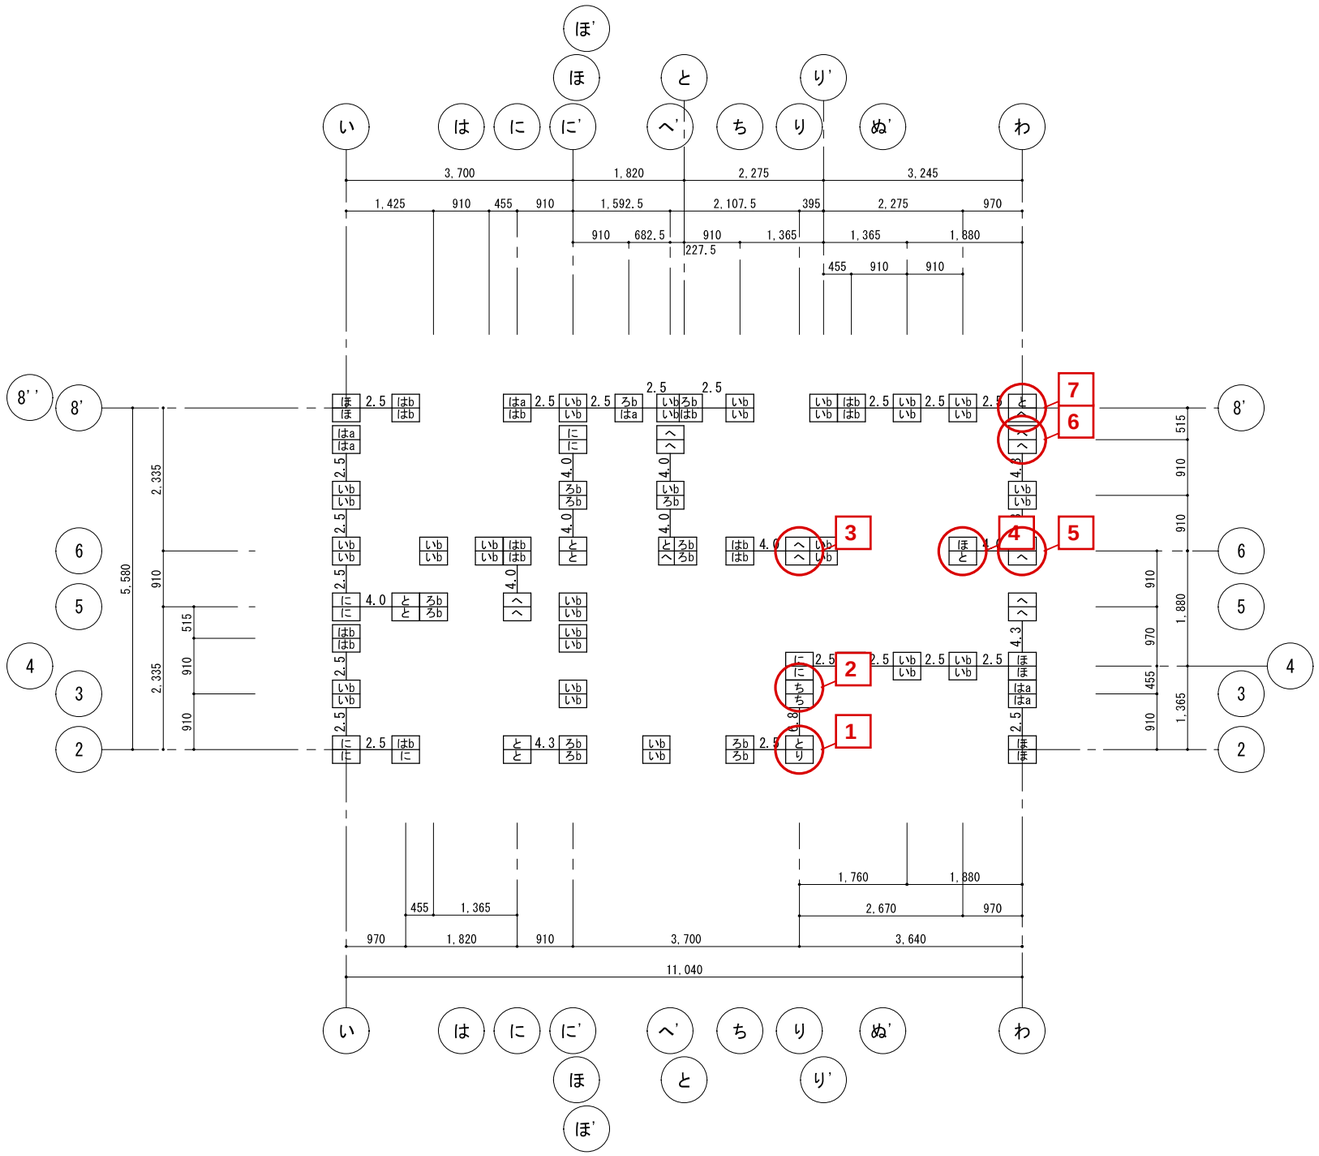

凡例）

上段は柱頭を示す。
下段は柱脚を示す。

2階　登り1　柱頭柱脚　金物図　1/100

株式会社 R-be architects 二級建築士事務所　二級 東京都知事登録　第 16330 号 二級 建築士登録　第 83516 号　渡辺　隆一	工事名称 SEKI HOUSE PROJECT	sign	drawn	checked	date	drawing title 金物図2	scale 1/100		drawing No. S-22