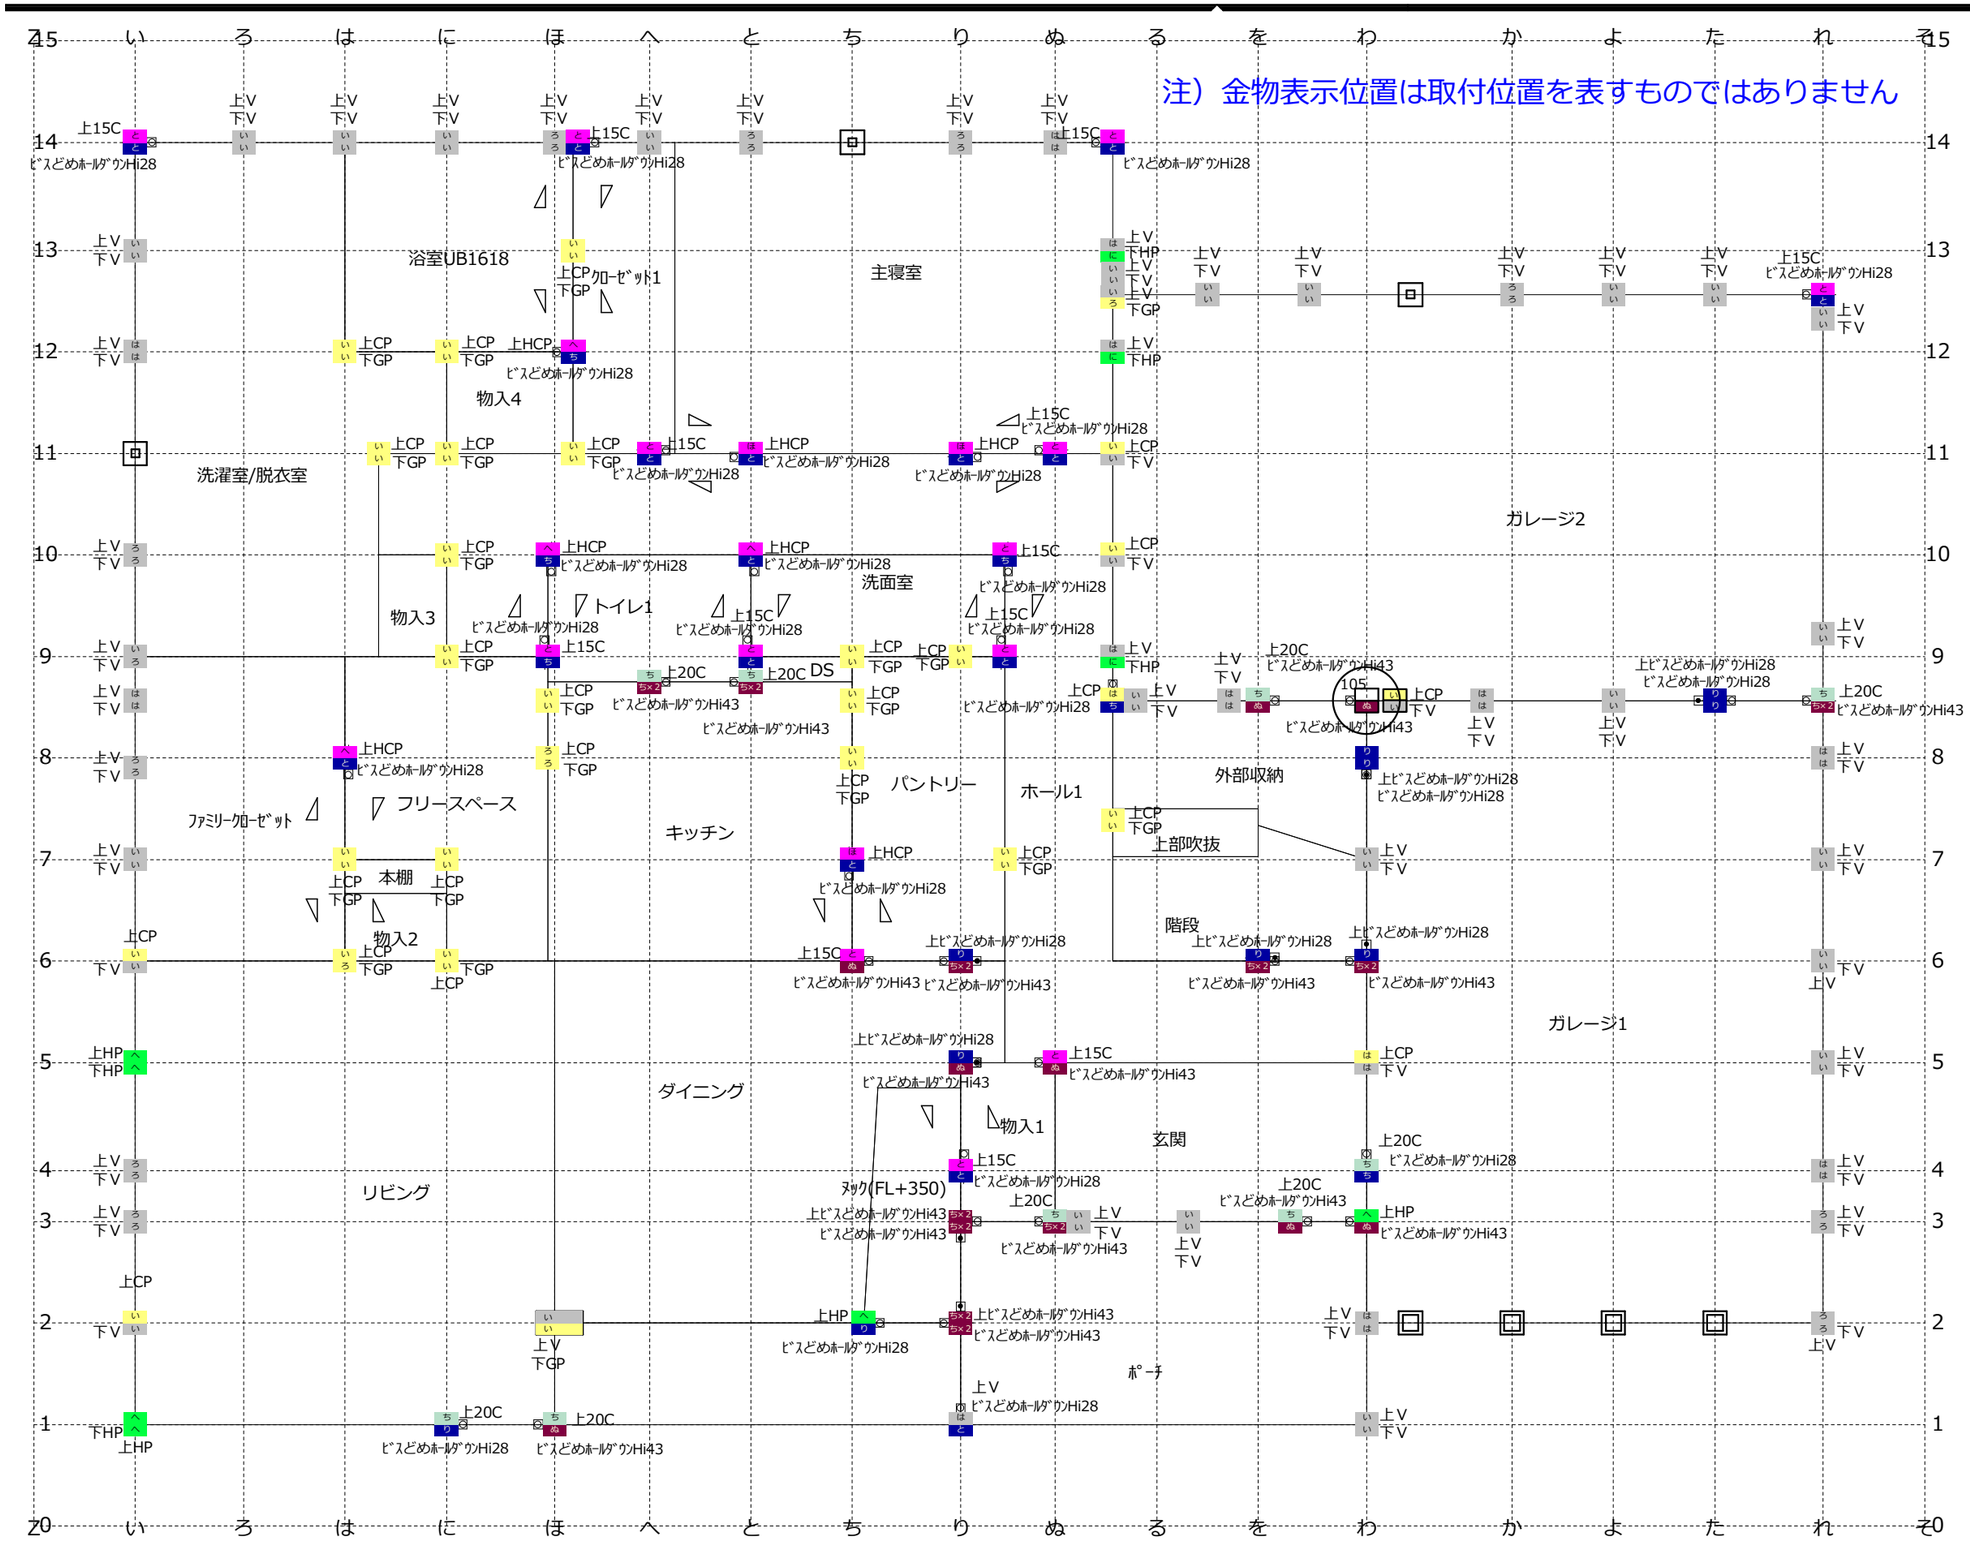


タナカ金物選定システム

い		
	V	ﾌﾗｯﾄﾌﾟﾚｰﾄｽﾘﾑ
	CP	ﾌｯｸｺｰﾅｰ床合板仕様
	GP	ﾌｯｸｺｰﾅｰ床合板仕様
ろ		
	V	ﾌﾗｯﾄﾌﾟﾚｰﾄｽﾘﾑ
	CP	ﾌｯｸｺｰﾅｰ床合板仕様
	GP	ﾌｯｸｺｰﾅｰ床合板仕様
は		
	V	ﾌﾗｯﾄﾌﾟﾚｰﾄｽﾘﾑ
	CP	ﾌｯｸｺｰﾅｰ床合板仕様
	GP	ﾌｯｸｺｰﾅｰ床合板仕様
に		
	HP	ﾒｶﾞﾌﾟﾚｰﾄSD 10kN
	HCP	ﾒｶﾞｺｰﾅｰ15kNⅡ床合板仕様
	HGP	ﾒｶﾞｺｰﾅｰ15kNⅡ床合板仕様
	Ⅰ外	
	Ⅰ内	
	PH	
	WP	
	WPH	
ほ	HP	ﾒｶﾞﾌﾟﾚｰﾄSD 10kN
	HCP	ﾒｶﾞｺｰﾅｰ15kNⅡ床合板仕様
	HGP	ﾒｶﾞｺｰﾅｰ15kNⅡ床合板仕様
	Ⅰ外	
	Ⅰ内	
	PH	
	WP	
	WPH	
へ	HP	ﾒｶﾞﾌﾟﾚｰﾄSD 10kN
	HCP	ﾒｶﾞｺｰﾅｰ15kNⅡ床合板仕様
	HGP	ﾒｶﾞｺｰﾅｰ15kNⅡ床合板仕様
と	15C	ﾒｶﾞｺｰﾅｰ15kNⅡ床合板仕様
	15G	ﾒｶﾞｺｰﾅｰ15kNⅡ床合板仕様
		ﾋﾞｽどめﾎｰﾙﾀﾞｳﾝHi28
ち	20C	ﾒｶﾞｺｰﾅｰ20kN用床合板仕様
	20G	ﾒｶﾞｺｰﾅｰ20kN用床合板仕様
		ﾋﾞｽどめﾎｰﾙﾀﾞｳﾝHi28
り		ﾋﾞｽどめﾎｰﾙﾀﾞｳﾝHi28
ぬ		ﾋﾞｽどめﾎｰﾙﾀﾞｳﾝHi43
ち×2		ﾋﾞｽどめﾎｰﾙﾀﾞｳﾝHi43

□	通　柱	◘	ﾎｰﾙﾀﾞｳﾝﾎﾞﾙﾄ 柱　脚
□	管　柱	◉	ﾎｰﾙﾀﾞｳﾝﾎﾞﾙﾄ 柱　頭
×	下階柱	⌀	羽子板ボルト 柱　脚
○	小屋束	●	羽子板ボルト 柱　頭
▨	耐力壁	▬	短ざく金物
◺	筋かい		


〒

TEL　　FAX

検図	設計	製図

モジュール	910		工法	在来工法		
階　高	1F	2940	2F	2730	3F	
屋根勾配	1F	1.5	2F	1.5	3F	

工事名称	關様邸（福山建築）金物図面	図面名称	土台伏図
印刷日時	2026年 5月11日 14:59	縮尺	1/55
		物件番号	25-46829

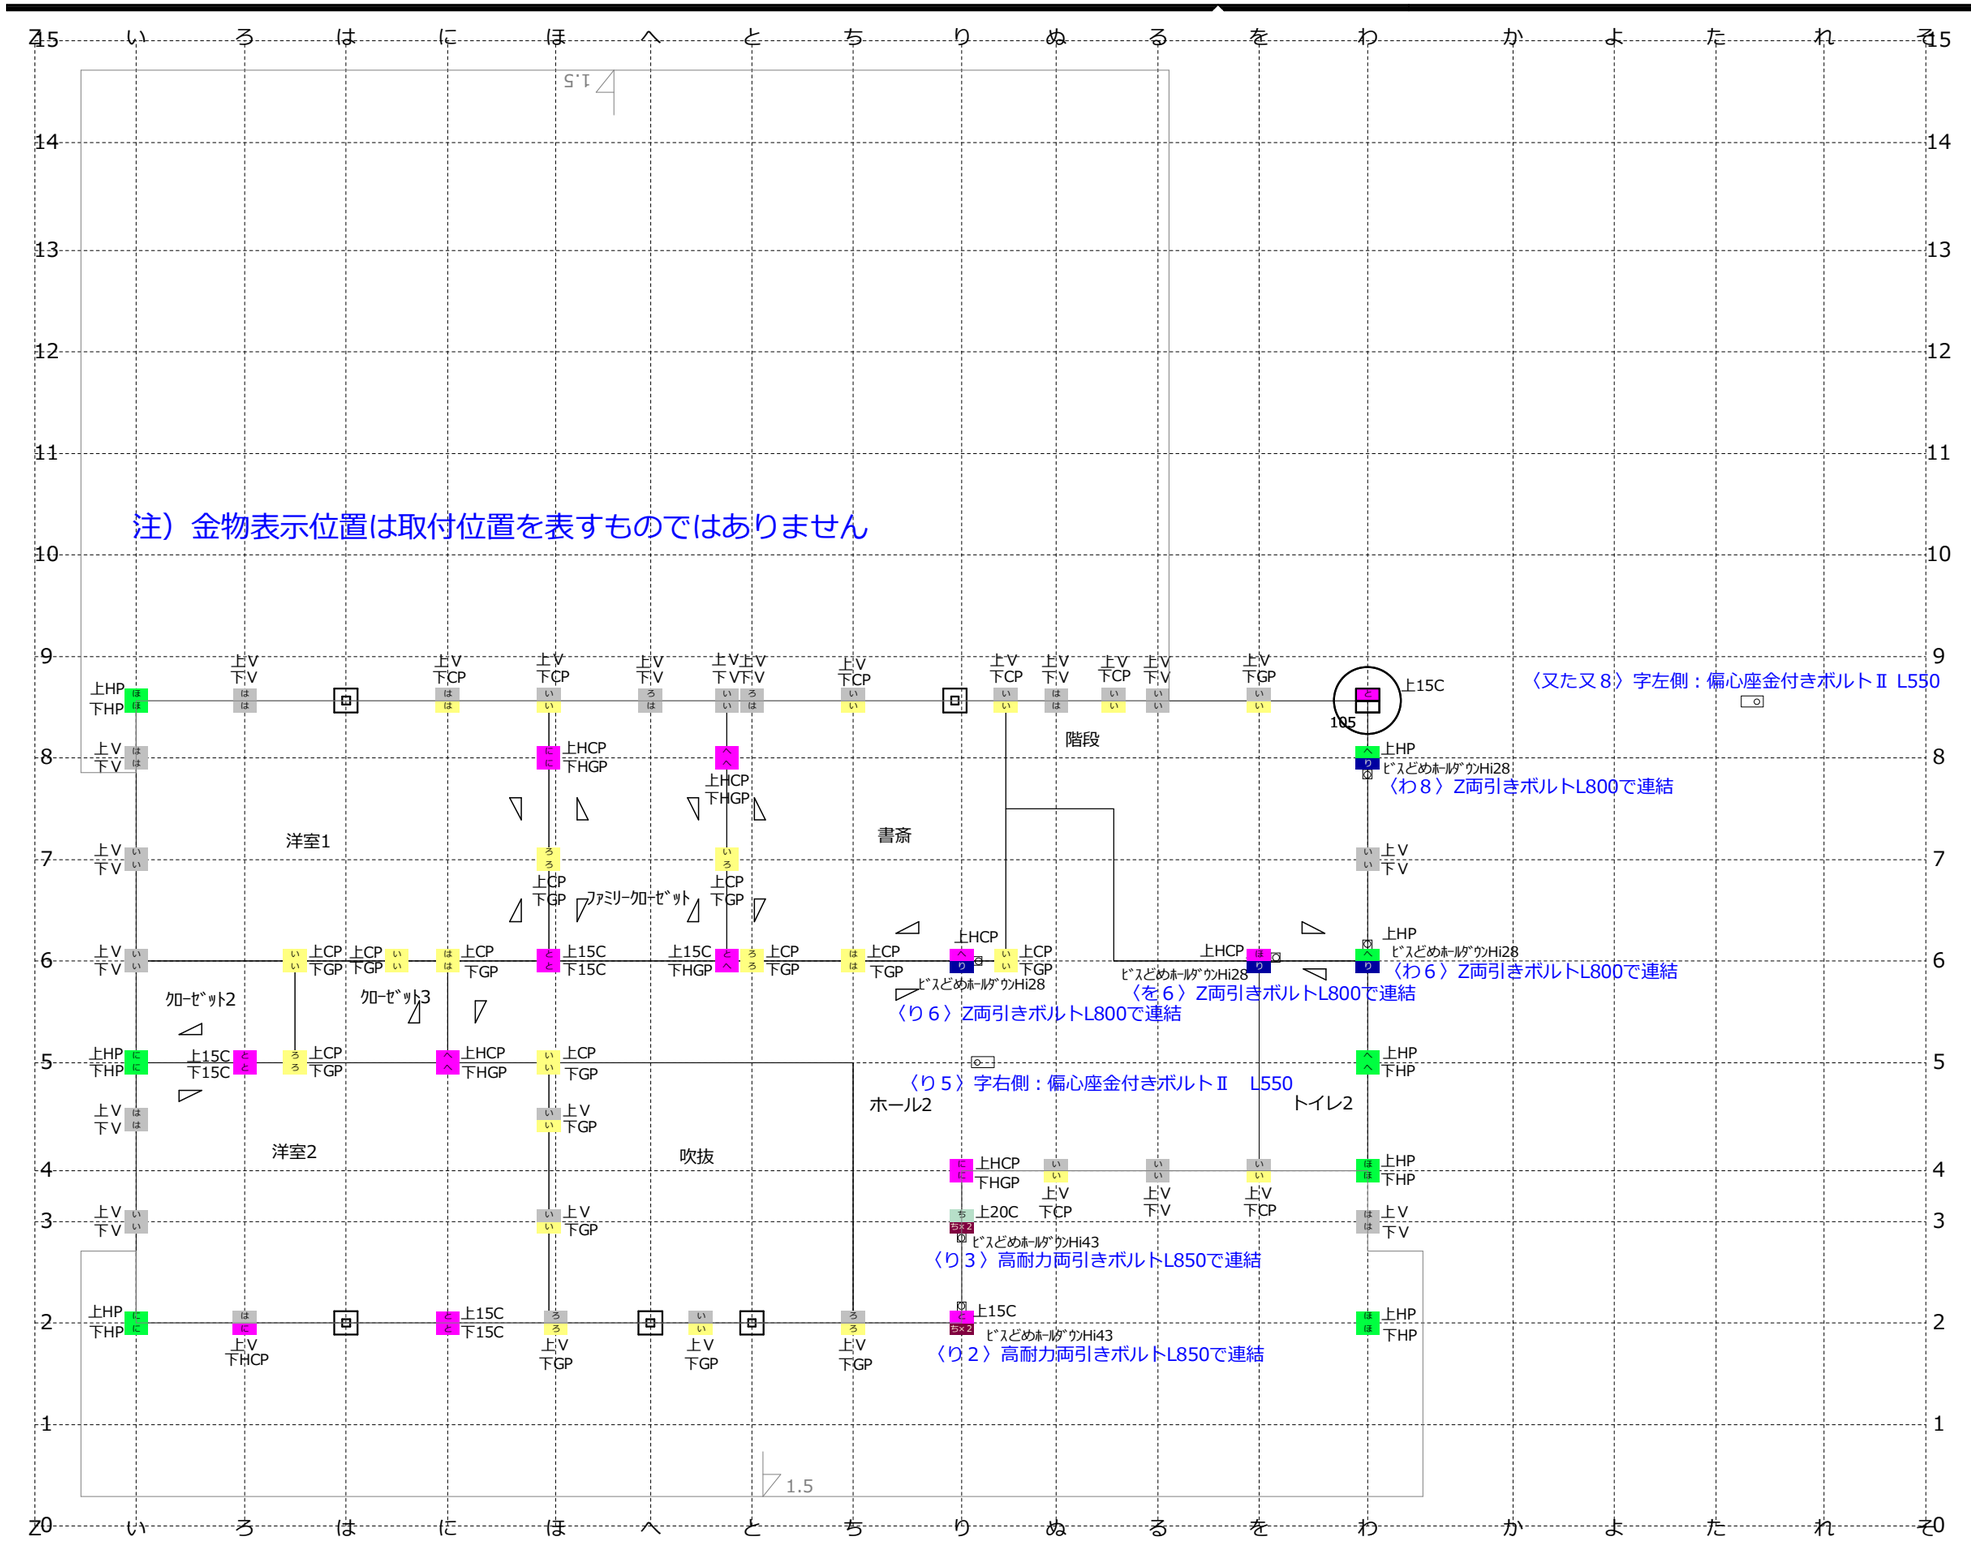

タナカ金物選定システム

い		
	V	ﾌﾗｯﾄﾌﾟﾚｰﾄｽﾘﾑ
	CP	ﾌｯｸｺｰﾅｰ床合板仕様
	GP	ﾌｯｸｺｰﾅｰ床合板仕様
ろ		
	V	ﾌﾗｯﾄﾌﾟﾚｰﾄｽﾘﾑ
	CP	ﾌｯｸｺｰﾅｰ床合板仕様
	GP	ﾌｯｸｺｰﾅｰ床合板仕様
は		
	V	ﾌﾗｯﾄﾌﾟﾚｰﾄｽﾘﾑ
	CP	ﾌｯｸｺｰﾅｰ床合板仕様
	GP	ﾌｯｸｺｰﾅｰ床合板仕様
に		
	HP	ﾒｶﾞﾌﾟﾚｰﾄSD 10kN
	HCP	ﾒｶﾞｺｰﾅｰ15kNⅡ床合板仕様
	HGP	ﾒｶﾞｺｰﾅｰ15kNⅡ床合板仕様
	Ⅰ外	
	Ⅰ内	
	PH	
	WP	
	WPH	
ほ	HP	ﾒｶﾞﾌﾟﾚｰﾄSD 10kN
	HCP	ﾒｶﾞｺｰﾅｰ15kNⅡ床合板仕様
	HGP	ﾒｶﾞｺｰﾅｰ15kNⅡ床合板仕様
	Ⅰ外	
	Ⅰ内	
	PH	
	WP	
	WPH	
へ	HP	ﾒｶﾞﾌﾟﾚｰﾄSD 10kN
	HCP	ﾒｶﾞｺｰﾅｰ15kNⅡ床合板仕様
	HGP	ﾒｶﾞｺｰﾅｰ15kNⅡ床合板仕様
と	15C	ﾒｶﾞｺｰﾅｰ15kNⅡ床合板仕様
	15G	ﾒｶﾞｺｰﾅｰ15kNⅡ床合板仕様
		ﾋﾞｽどめﾎｰﾙﾀﾞｳﾝHi28
ち	20C	ﾒｶﾞｺｰﾅｰ20kN用床合板仕様
	20G	ﾒｶﾞｺｰﾅｰ20kN用床合板仕様
		ﾋﾞｽどめﾎｰﾙﾀﾞｳﾝHi28
り		ﾋﾞｽどめﾎｰﾙﾀﾞｳﾝHi28
ぬ		ﾋﾞｽどめﾎｰﾙﾀﾞｳﾝHi43
ち×２		ﾋﾞｽどめﾎｰﾙﾀﾞｳﾝHi43

□	通　柱	□	ﾎｰﾙﾀﾞｳﾝﾎﾞﾙﾄ 柱　脚
□	管　柱	◉	ﾎｰﾙﾀﾞｳﾝﾎﾞﾙﾄ 柱　頭
×	下階柱	⏀	羽子板ボルト 柱　脚
○	小屋束	●	羽子板ボルト 柱　頭
▨	耐力壁	▬	短ざく金物
◺	筋かい		

〒

TEL　　FAX

検図	設計	製図

モジュール	910		工法	在来工法		
階　高	1F	2940	2F	2730	3F	
屋根勾配	1F	1.5	2F	1.5	3F	

工事名称	關様邸（福山建築）金物図面	図面名称	２階床伏図
印刷日時	2026年 5月11日 14:59	縮尺	1/55
		物件番号	25-46829