


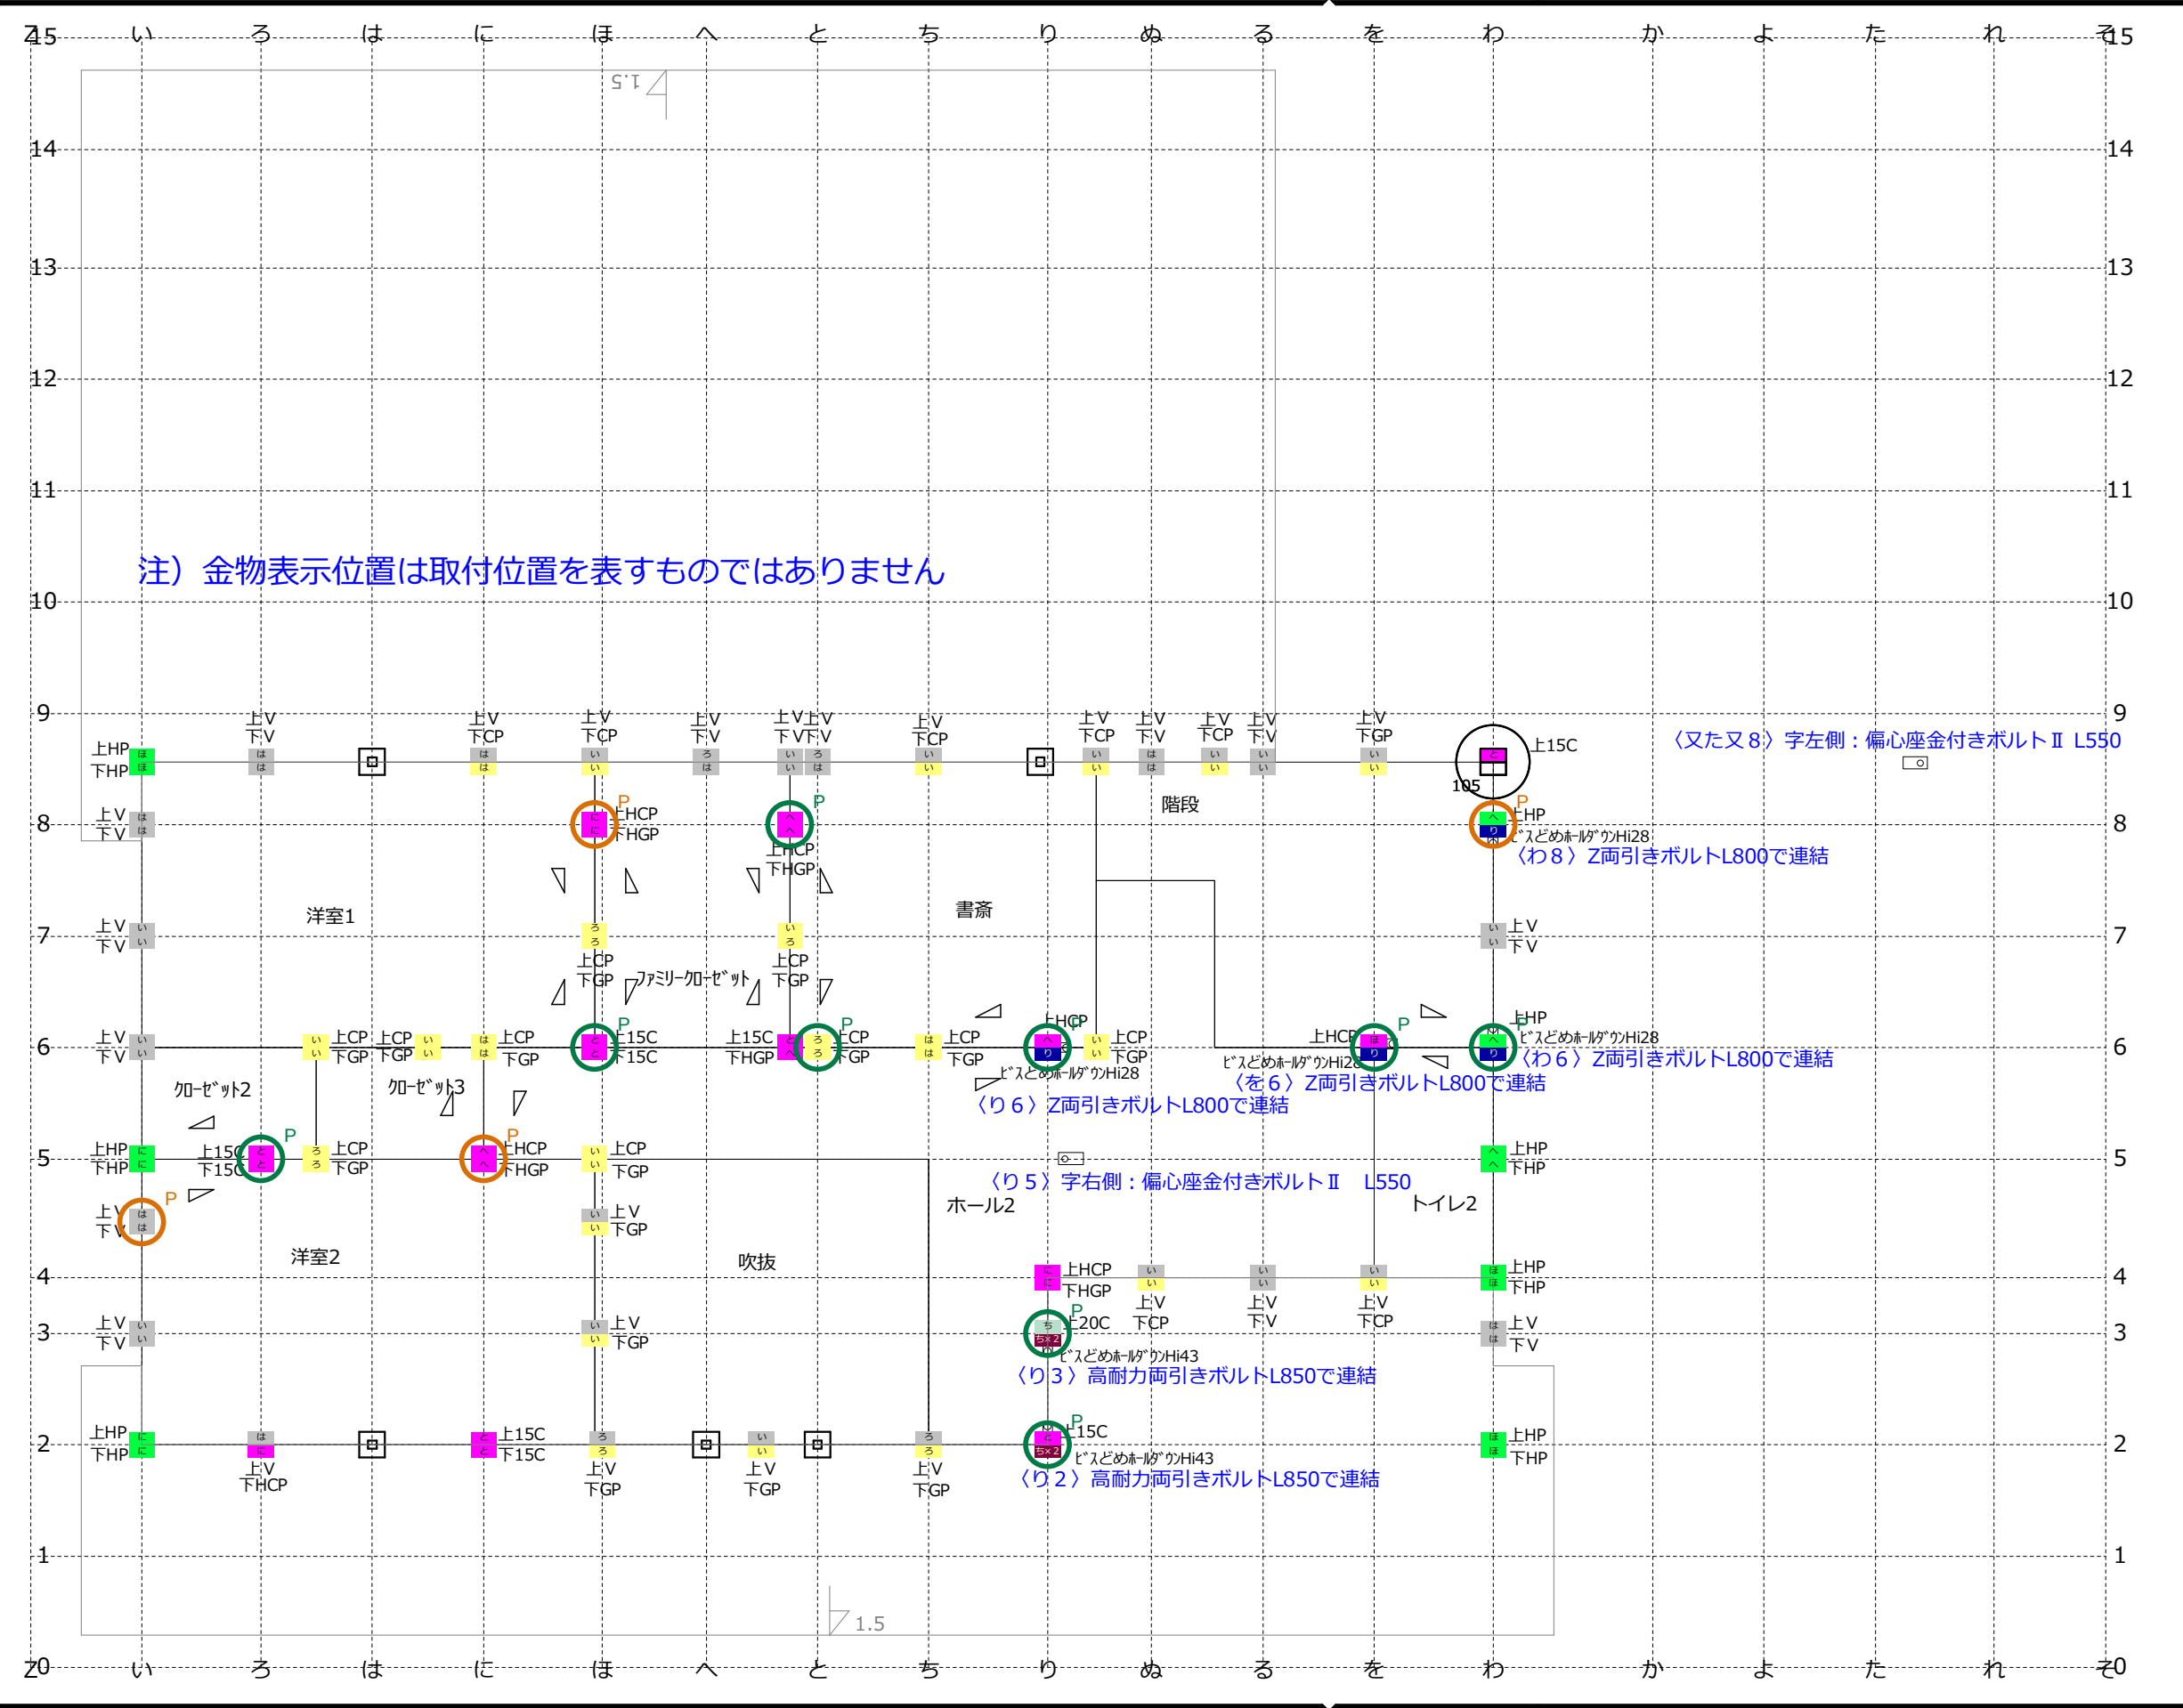

タナカ金物選定システム			
い	V	フラットプレートリム	
	CP	フックコーナー床合板仕様	
	GP	フックコーナー床合板仕様	
ろ	V	フラットプレートリム	
	CP	フックコーナー床合板仕様	
	GP	フックコーナー床合板仕様	
は	V	フラットプレートリム	
	CP	フックコーナー床合板仕様	
	GP	フックコーナー床合板仕様	
に	HP	わがプレートSD 10kN	
	HCP	わがコーナー15kNⅡ床合板仕様	
	HGP	わがコーナー15kNⅡ床合板仕様	
	I 外		
	I 内		
	PH		
	WP		
	WPH		
	HP	わがプレートSD 10kN	
	HCP	わがコーナー15kNⅡ床合板仕様	
ほ	HGP	わがコーナー15kNⅡ床合板仕様	
	I 外		
	I 内		
	PH		
	WP		
	WPH		
	HP	わがプレートSD 10kN	
へ	HCP	わがコーナー15kNⅡ床合板仕様	
	HGP	わがコーナー15kNⅡ床合板仕様	
と	15C	わがコーナー15kNⅡ床合板仕様	
	15G	わがコーナー15kNⅡ床合板仕様	
		ビスどめホルダウHi28	
ち	20C	わがコーナー20kN用床合板仕様	
	20G	わがコーナー20kN用床合板仕様	
		ビスどめホルダウHi28	
り		ビスどめホルダウHi28	
ぬ		ビスどめホルダウHi43	
ち×2		ビスどめホルダウHi43	
⊖	通 柱	⊖	ホルダウホルト柱 脚
□	管 柱	⊖	ホルダウホルト柱 頭
×	下階柱	⊖	羽子板ボルト柱 脚
○	小屋束	⊖	羽子板ボルト柱 頭
////	耐力壁	■	短ざく金物
△	筋かい		

〒	TEL	FAX	検図	設計	製図	モジュール		910		工法	在来工法		工事名称	關様邸（福山建築）金物図面		図面名称	2 階床伏図						
						階 高	1F	2940	2F		2730	3F		印刷日時	2026年 5月11日 14:59		縮尺	1/55		物件番号	25-46829		
						屋根勾配	1F	1.5	2F		1.5	3F											

写真マークの凡例・照合記録

対象：ANDPAD「關優太様邸／金物全種」の共有スクリーンショット4画面。重複を除く139枚のうち「×」13枚は対象外、番付付き126枚。

階表示あり42枚（1F 25枚・2F 17枚）。階未記載84枚は1F 58枚・2F 25枚・未割当1枚に暫定整理。

未割当：112/139「り3・柱脚」。両階ともHi43指定のため、この写真単独では階を確定できず、どちらの階の根拠にも追加していません。

「又」の番付は写真メモを保持し、図面の追加柱・金物の組み合わせに対応づけています。軸線名とは一致しない位置があります。

紫印の「ち2／又ち2」は複数番付を含む写真です。正確な撮影対象位置を確認してください。

「い1」は座金写真、「い又4」はボルト・座金接合部写真です。指定金物全体の撮影を確認した印ではありません。

丸印は元図面の金物表示を囲んでいます。元図面にも記載のとおり、金物表示位置は実際の取付位置そのものではありません。

緑：階明記または拡大写真による階確認。橙：図面・金物・同番付写真からの推定。印なしの箇所は未確認であり、未施工を意味しません。

1F 写真メモとマーク一覧

写真メモの番付	判定
い14	写真あり・階確認
又ほ14	写真あり・階推定
又ぬ14	写真あり・階確認
又ぬ13	写真あり・階推定
又ほ12	写真あり・階推定
又ぬ12	写真あり・階推定
へ11	写真あり・階推定
と11	写真あり・階推定
り11	写真あり・階確認
ぬ11	写真あり・階推定
又に10	写真あり・階推定
と10	写真あり・階推定
又り10	写真あり・階推定
又に9	写真あり・階推定
と9	写真あり・階推定
又り9	写真あり・階推定
ぬ9	写真あり・階推定
へ又8	写真あり・階推定
と又8	写真あり・階推定
又ぬ又8	写真あり・階推定
を又8	写真あり・階確認
又わ又8	写真あり・階推定
た又8	写真あり・階確認
れ又8	写真あり・階確認
は8	写真あり・階推定
わ8	写真あり・階確認
ち7	写真あり・階推定
ち6	写真あり・階確認
り6	写真あり・階推定
を6	写真あり・階確認
わ6	写真あり・階推定
わ4	写真あり・階確認
り3	写真あり・階確認
ぬ3	写真あり・階確認
又を3	写真あり・階確認
わ3	写真あり・階確認
ち2 / 又ち2	写真あり・位置要確認
り2	写真あり・階推定
い1 [座金]	写真あり・階確認
に1	写真あり・階推定
ほ1	写真あり・階推定
れ又12	写真あり・階確認

2F 写真メモとマーク一覧

写真メモの番付	判定
又に8	写真あり・階推定
又へ8	写真あり・階確認
わ8	写真あり・階推定
又に6	写真あり・階確認
と6	写真あり・階確認
り6	写真あり・階確認
を6	写真あり・階確認
わ6	写真あり・階確認
ろ5	写真あり・階確認
に5	写真あり・階推定
い又4	写真あり・階推定
り3	写真あり・階確認
り2	写真あり・階確認

拡大確認した写真番号

80～82：わ8 → 2F推定（柱頭HP／柱脚Hi28）

98・99：わ8 → 1F（基礎・地面・1F表示）

112：り3・柱脚 → 階未割当

113：り2・柱頭 → 1F指定に対応

114：り2・柱脚 → 113番と合わせて1F推定

120：い又4 → 2F推定（柱位置の対応）

原図：關様邸金物図面0512.pdf（2枚）

このPDFは原図への写真照合マークの追記版です。

ANDPADの写真メモ・フォルダは変更していません。